



LS ELECTRIC 천안 R-Center 구축설계

- 실시설계 도서 -
[통신]

2024.05

(주)가운종합건축사사무소

PROJECT TITLE

LS Electric
R-Center 구축

PROJECT NUMBER

624001

DESIGN CONSULTANT

가운 건축

GAUN | Architects & Engineers

서울시 강남구 언주로 141길 6. 5층 (논현동, 백암빌딩)
Tel:82-2-3443-7799 Fax:82-2-3443-3807
www.gaun.co.kr

NOTES

KEY PLAN

△

△

△

△

△

△

△

△

NO.

DESCRIPTION

DATE

ISSUES & REVISIONS

BUILDING NAME

DRAWING TITLE

정보통신용 도면 목록표

DRAWN

CHECK 1

CHECK 2

APPR

SCALE

DATE

2024.04

A3 : 1/NONE

A3 : 1/NONE

DRAWING NO.

ET-00-001

NO	도면번호	도 면 명	축척		비 고
			A1	A3	
일 반 사 항					
1	ET-00-001	정보통신용 도면 목록표	NONE	NONE	
2	ET-00-002	정보통신용 범례 및 주기사항	NONE	NONE	
3	ET-00-003	옥외 정보통신 인입 배치도	1/500	1/1000	
정 보 통 신 설 비					
4	ET-01-001	정보통신설비 계통도	NONE	NONE	
5	ET-01-002	PIT층 정보통신설비 평면도	1/200	1/400	
6	ET-01-003	지상1층 정보통신설비 평면도	1/200	1/400	
7	ET-01-004	지상2층 정보통신설비 평면도	1/200	1/400	
8	ET-01-005	사무동 지하1층 정보통신 설비 평면도	1/150	1/300	
9	ET-01-006	사무동 지상1층 정보통신 설비 평면도	1/150	1/300	
10	ET-01-007	사무동 지상2층 정보통신 설비 평면도	1/150	1/300	
방 송 설 비					
11	ET-02-001	방송설비 계통도	NONE	NONE	
12	ET-02-002	PIT층 방송 설비 평면도	1/200	1/400	
13	ET-02-003	지상1층 방송 설비 평면도	1/200	1/400	
14	ET-02-004	지상2층 방송 설비 평면도	1/200	1/400	
15	ET-02-005	사무동 지하1층 방송 설비 평면도	1/150	1/300	
16	ET-02-006	사무동 지상1층 방송 설비 평면도	1/150	1/300	
BLOCK DIAGRAM 및 상 세 도					
17	ET-03-001	통합배선설비 구성도	NONE	NONE	
18	ET-03-002	통합배선설비 상세도	NONE	NONE	

정보통신용 도면 목록표

축척:A1 : 1/NONE
A3 : 1/NONE

전력시설물종합설계업 제서울 E-1-055호
엔지니어링 활동주체 제06-378호
전기·정보통신 설계·감리 및 소방설계
JM(주) 정 명 기 술 단
대표 · 기술사 이 정 환

엔지니어링활동주체신고증 신고번호제 06-378호
기술무류:통신·정보처리,전문분야:정보통신
JM(주) 정 명 기 술 단
통신선로산업기사 김 근 식

[illegible]

전력시설종합설계업 제서울 E-1-055호
엔지니어링 활동주체 제06-378호
전기·정보통신 설계·감리 및 소방설계
JM(주) 정 명 기 술 단
대표·기술사 이 정 환

맨지니어링활동주체신고증 신고번호:제 06-378호
기술부분:통신 정보처리,전문분야:정보통신
JM (주) 정 명 기 술 단
통신선로산업기사 김 근 식

PROJECT TITLE

LS Electric
R-Center 구축

PROJECT NUMBER

624001

DESIGN CONSULTANT

가운 건축
GAUN | Architects & Engineers

서울시 강남구 언주로 141길 6.5층 (논현동, 백암빌딩)
Tel: 82-2-3443-7799 Fax: 82-2-3443-3807
www.gaun.co.kr

NOTES

KEY PLAN

NO.	DESCRIPTION	DATE
		

ISSUES & REVISIONS

BUILDING NAME

DRAWING TITLE

정보통신용 범례 및 주기사항

DRAWN	SCALE
CHECK 1 안 동 식	A3 : 1/NONE A3 : 1/NONE
CHECK 2 이 은 진	DATE
APPR 정 용 재	2024.04

DRAWING NO.

ET-00-002

CABLE SCHEDULE

NO	CABLE & CONDUIT SIZE
(T)	28C (UTP 0.5mm/25Px1, CAT.5e)
(T1)	16C (UTP 0.5mm/4Px1, CAT.5e)
(T2)	16C (UTP 0.5mm/4Px2, CAT.5e)
(T3)	22C (UTP 0.5mm/4Px3, CAT.5e)
(T4)	22C (UTP 0.5mm/4Px4, CAT.5e)
(T5)	28C (UTP 0.5mm/4Px5, CAT.5e)
(T6)	28C (UTP 0.5mm/4Px6, CAT.5e)
(F)	ELP 100Ø (F/O CABLE S.M 12CORE)
(F1)	F/O CABLE S.M 2CORE
(F2)	F/O CABLE S.M 4CORE
(F3)	F/O CABLE S.M 8CORE
(F4)	F/O CABLE S.M 12CORE
(E1)	28C (EMPTY CONDUIT)
(E2)	36C (EMPTY CONDUIT)
(G1)	16C (F-GV 1 - 6sq)
(G2)	22C (F-GV 1 - 16sq)

주기사항

- 충간 방화 구획 처리.
- CABLE TRAY내 배관,배선시 전선관을 제외한 CABLE만 포설한다.
- CABLE TRAY내 공통 접지선은 1-GV 16sq로 한다.
- CABLE TRAY 통신용과 공용임
- 방화구획을 관통하는 부위에는 불연재의 방화재로 완전 방화구획이 되도록 차폐한다.
- SYMBOL
凸 : LAN OUTLET 2PORT
⏏ : LAN OUTLET 1PORT
⏏T : LAN OUTLET(TEL) 1PORT
□ : 전화 단자함(Intermediate Terminal Board)
□ : 광 OUTLET
■ : SYSTEM BOX(LAN) 2PORT
■ : SYSTEM BOX(LAN) 1PORT, (광) 1PORT
⊕ : 무선 AP

LS Electric
R-Center 구축

PROJECT NUMBER
624001

DESIGN CONSULTANT
가운 건축
GAUN | Architects & Engineers

서울시 강남구 언주로 141길 6. 5층 (논현동, 벅함빌딩)
Tel:82-2-3443-7799 Fax:82-2-3443-3807
www.gaun.co.kr

NOTES

REF PLAN

NO

DESCRIPTION

DATE

ISSUES & REVISIONS

BUILDING NAME

DRAWING TITLE

정보통신설비 계통도

DRAWN

CHECK 1

CHECK 2

APPR

DATE

정 용 재

2024.04

DRAWING NO.

ET-01-001

▼ 지붕층 F.L

▼ 2층 F.L

▼ 1층 F.L




▼ PIT층 F.L

정보통신설비 계통도

축척:A1 : 1/NONE
A3 : 1/NONE

전력시설물종합설계업 제서울 E-1-055호
엔지니어링 활동주체 제06-378호
전기·정보통신 설계·감리 및 소방설계
JM(주) 정명기술단
대표·기술사 이 정 환

엔지니어링활동주체신고증 신고번호제 06-378호
기술부문:통신·정보처리,전문분야:정보통신
JM(주) 정명기술단
통신전선산업기사 김 근 식

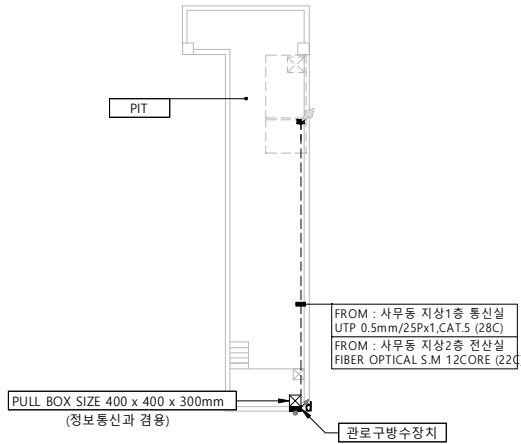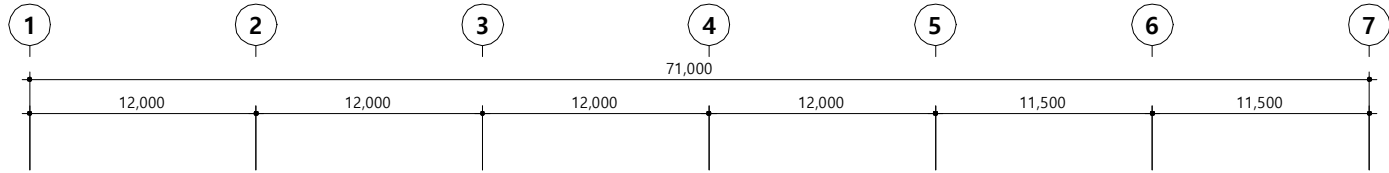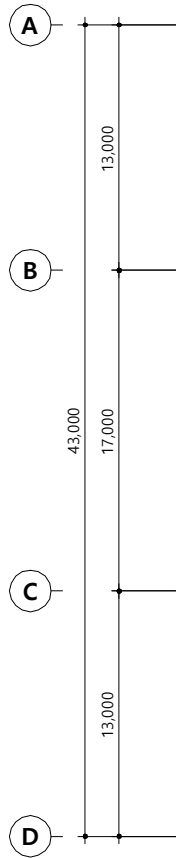

주기사항

1. 배관, 배선
—— 슬라브 매입 배관 배선
- - - - 노출 배관 배선
- · - · 바닥 은폐 및 지중 매설 배관 배선
- · · - DUCT 및 TRAY내 배선

2. 통신용 배관, 배선
- T — / - : 16C (UTP 0.5mm/4Px2, CAT.5e)
- T — / - : 22C (UTP 0.5mm/4Px3, CAT.5e)
- T — / - : 22C (UTP 0.5mm/4Px4, CAT.5e)
- T — / - : 28C (UTP 0.5mm/4Px6, CAT.5e)
- T — / - : 28C (UTP 0.5mm/4Px8, CAT.5e)
- FO — : 16C (FIBER OPTICAL S.M 2CORE)
- CC — : 16C (FIBER OPTICAL S.M 4CORE)

3. LEGEND
☐ : LAN OUTLET 2PORT
☐ : SYSTEM BOX(LAN) 2PORT
☐ : SYSTEM BOX(LAN) 1PORT, (광) 1PORT
☐ : LAN OUTLET(TEL) 1PORT
☐ : 광 OUTLET
⊙ : 무선 AP
⊙ : CCTV
☐ : 전화 단자함(Intermediate Terminal Board)
☐_a : PULL BOX SIZE 150 x 150 x 100mm
☐_b : PULL BOX SIZE 200 x 200 x 150mm
☐_c : PULL BOX SIZE 300 x 300 x 200mm
☐_d : PULL BOX SIZE 400 x 400 x 300mm

4. CABLE TRAY내 포설시 전선관을 제외한 CABLE만 포설한다.
5. CABLE TRAY 및 노출 배관 배선의 지지행거는 1,500mm마다 설치한다.
6. CABLE TRAY 내 접지선은 F-GV 16sq x 1를 사용한다.
7. 간선 규격 및 기타 사항은 계통도 참조.

LS Electric
R-Center 구축

PROJECT NUMBER
624001

가운 건축
GAUN | Architects & Engineers

서울시 강남구 언주로 141길 6. 5층 (논현동, 역삼빌딩)
Tel:82-2-3443-7799 Fax:82-2-3443-3807
www.gaun.co.kr

NOTES

KEY PLAN

△		
△		
△		
△		
△		
△		
△		
△		
NO.	DESCRIPTION	DATE

ISSUES & REVISIONS

BUILDING NAME

DRAWING TITLE

PIT층
정보통신설비 평면도

DRAWN	SCALE
CHECK 1 안 동 식	A3 : 1/200 A3 : 1/400
CHECK 2 이 은 진	DATE
APPR 정 용 재	2024.04

DRAWING NO.




ET-01-002

PIT층 정보통신설비 평면도

축척:A1 : 1/200
A3 : 1/400

전력시설물종합설계업 제서울 E-1-055호
엔지니어링 활동주체 제06-378호
전기·정보통신 설계·감리 및 소방설계
JM(주) 정 명 기 술 단
대표·기술사 이 정 환

엔지니어링활동주체신고증 신고번호제 06-378호
기술무류:통신·정보처리,전문분야:정보통신
JM(주) 정 명 기 술 단
통신전로산업기사 김 근 식

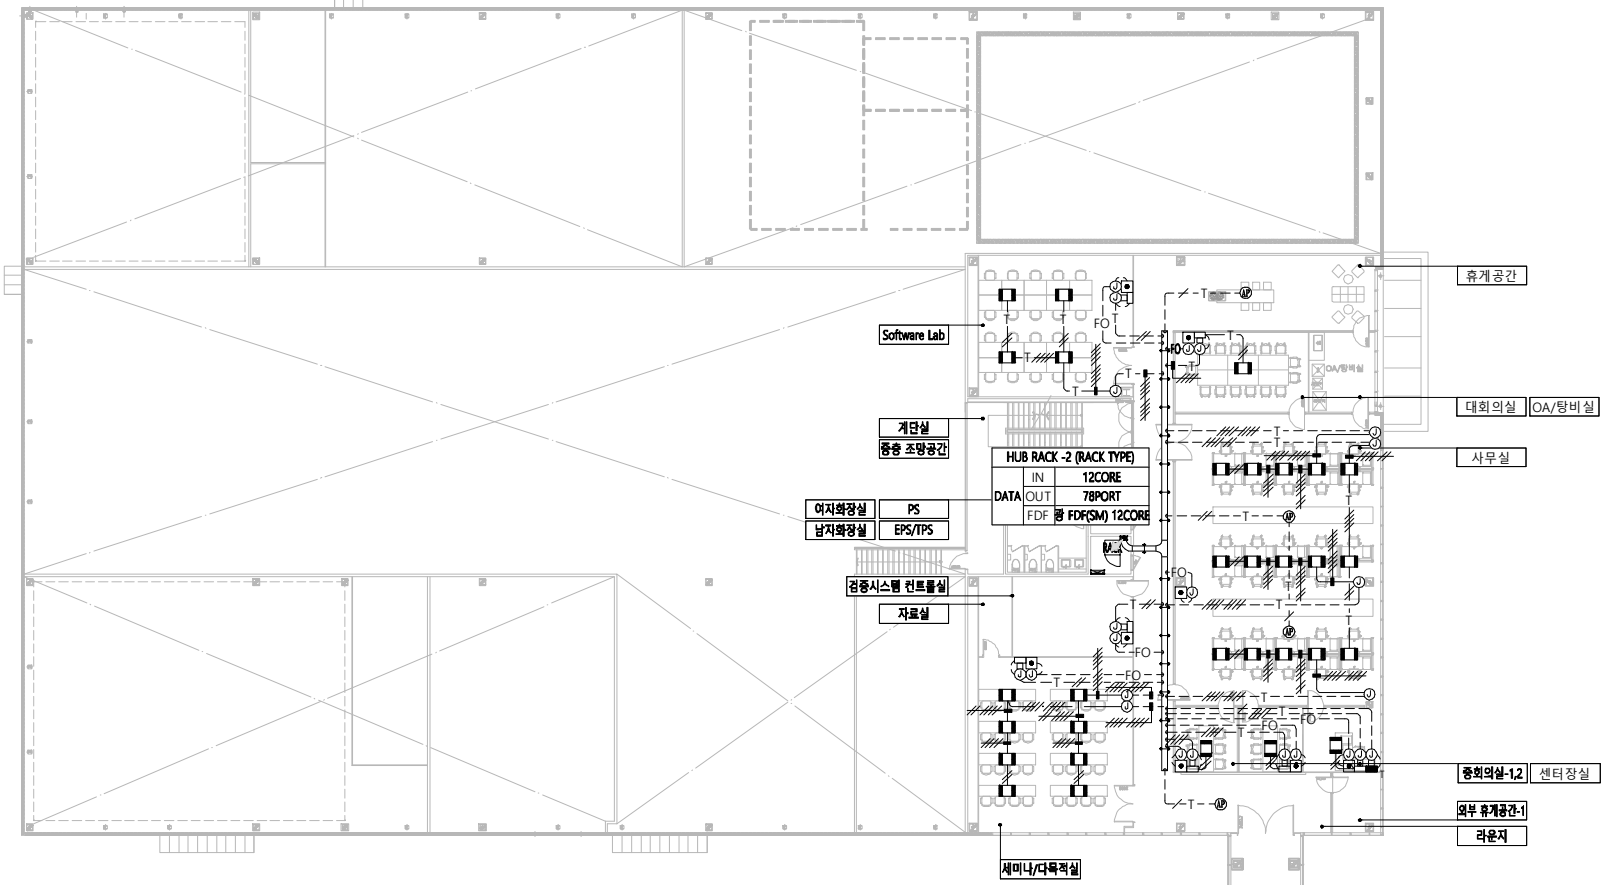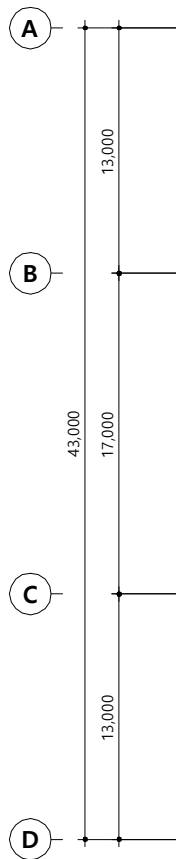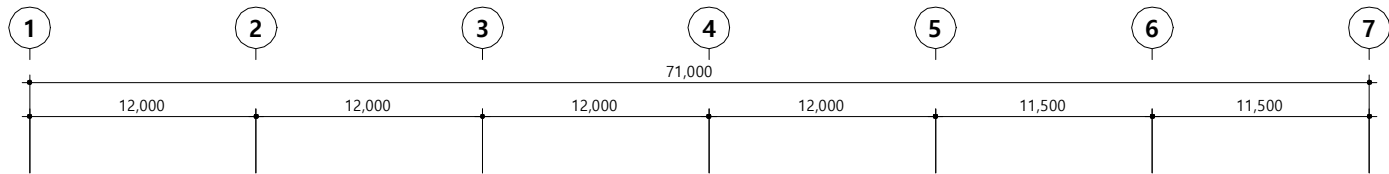

주기사항

1. 배관, 배선
—— 슬라브 매입 배관 배선
- - - - 노출 배관 배선
- · - · 바닥 은폐 및 지중 매설 배관 배선
- · · - DUCT 및 TRAY내 배선

2. 통신용 배관, 배선

- T — — — : 16C (UTP 0.5mm/4Px2, CAT.5e)
- T — — — : 22C (UTP 0.5mm/4Px3, CAT.5e)
- T — — — : 22C (UTP 0.5mm/4Px4, CAT.5e)
- T — — — : 28C (UTP 0.5mm/4Px6, CAT.5e)
- T — — — : 28C (UTP 0.5mm/4Px8, CAT.5e)
— FO — : 16C (FIBER OPTICAL S.M 2CORE)
— CC — : 16C (FIBER OPTICAL S.M 4CORE)

3. LEGEND

- : LAN OUTLET 2PORT
□ : SYSTEM BOX(LAN) 2PORT
□ : SYSTEM BOX(LAN) 1PORT, (광) 1PORT
□ : LAN OUTLET(TEL) 1PORT
□ : 광 OUTLET
⊙ : 무선 AP
⊙ : CCTV
□ : 전화 단자함(Intermediate Terminal Board)
⊠_a : PULL BOX SIZE 150 x 150 x 100mm
⊠_b : PULL BOX SIZE 200 x 200 x 150mm
⊠_c : PULL BOX SIZE 300 x 300 x 200mm
⊠_d : PULL BOX SIZE 400 x 400 x 300mm

4. CABLE TRAY내 포설시 전선관을 제외한 CABLE만 포설한다.
5. CABLE TRAY 및 노출 배관 배선의 지지행거는 1,500mm마다 설치한다.
6. CABLE TRAY 내 접지선은 F-GV 16sq x 1를 사용한다.
7. 간선 규격 및 기타 사항은 계통도 참조.

LS Electric R-Center 구축

PROJECT NUMBER
624001

DESIGN CONSULTANT

가운 건축

GAUN | Architects & Engineers

서울시 강남구 언주로 141길 6. 5층 (논현동, 박향빌딩)
Tel:82-2-3443-7799 Fax:82-2-3443-3807
www.gaun.co.kr

NOTES

REF PLAN

△		
△		
△		
△		
△		
△		
△		
△		
NO.	DESCRIPTION	DATE

ISSUES & REVISIONS

BUILDING NAME

DRAWING TITLE

지상2층 정보통신설비 평면도

DRAWN	SCALE
CHECK 1 안동식	A3 : 1/200 A3 : 1/400
CHECK 2 이은진	DATE
APPR 정용재	2024.04

DRAWING NO.

ET-01-004

지상2층 정보통신설비 평면도

축척:A1 : 1/200
A3 : 1/400

전력시설물종합설계업 제서울 E-1-055호
엔지니어링 활동주체 제06-378호
전기·정보통신 설계·감리 및 소방설계
JM(주) 정명기술단
대표·기술사 이정환

엔지니어링활동주체신고증 신고번호 제 06-378호
기술부문:통신·정보처리,전문분야:정보통신
JM(주) 정명기술단
통신설비산업기사 김근식

LS Electric
R-Center 구축

624001

가운 건축

GAUN | Architects & Engineers

서울시 강남구 언주로 141길 6. 5층 (논현동, 백암빌딩)
Tel: 82-2-3443-7799 Fax: 82-2-3443-3807
www.gaun.co.kr

NOTES

KEY PLAN

NO. DESCRIPTION DATE

ISSUES & REVISIONS


BUILDING NAME

DRAWING TITLE

사무동 지하1층
정보통신 설비 평면도

DRAWN CHECK 1 CHECK 2 APPR. SCALE A3 : 1/150 A3 : 1/300 DATE 2024.04

DRAWING NO. ET-01-005

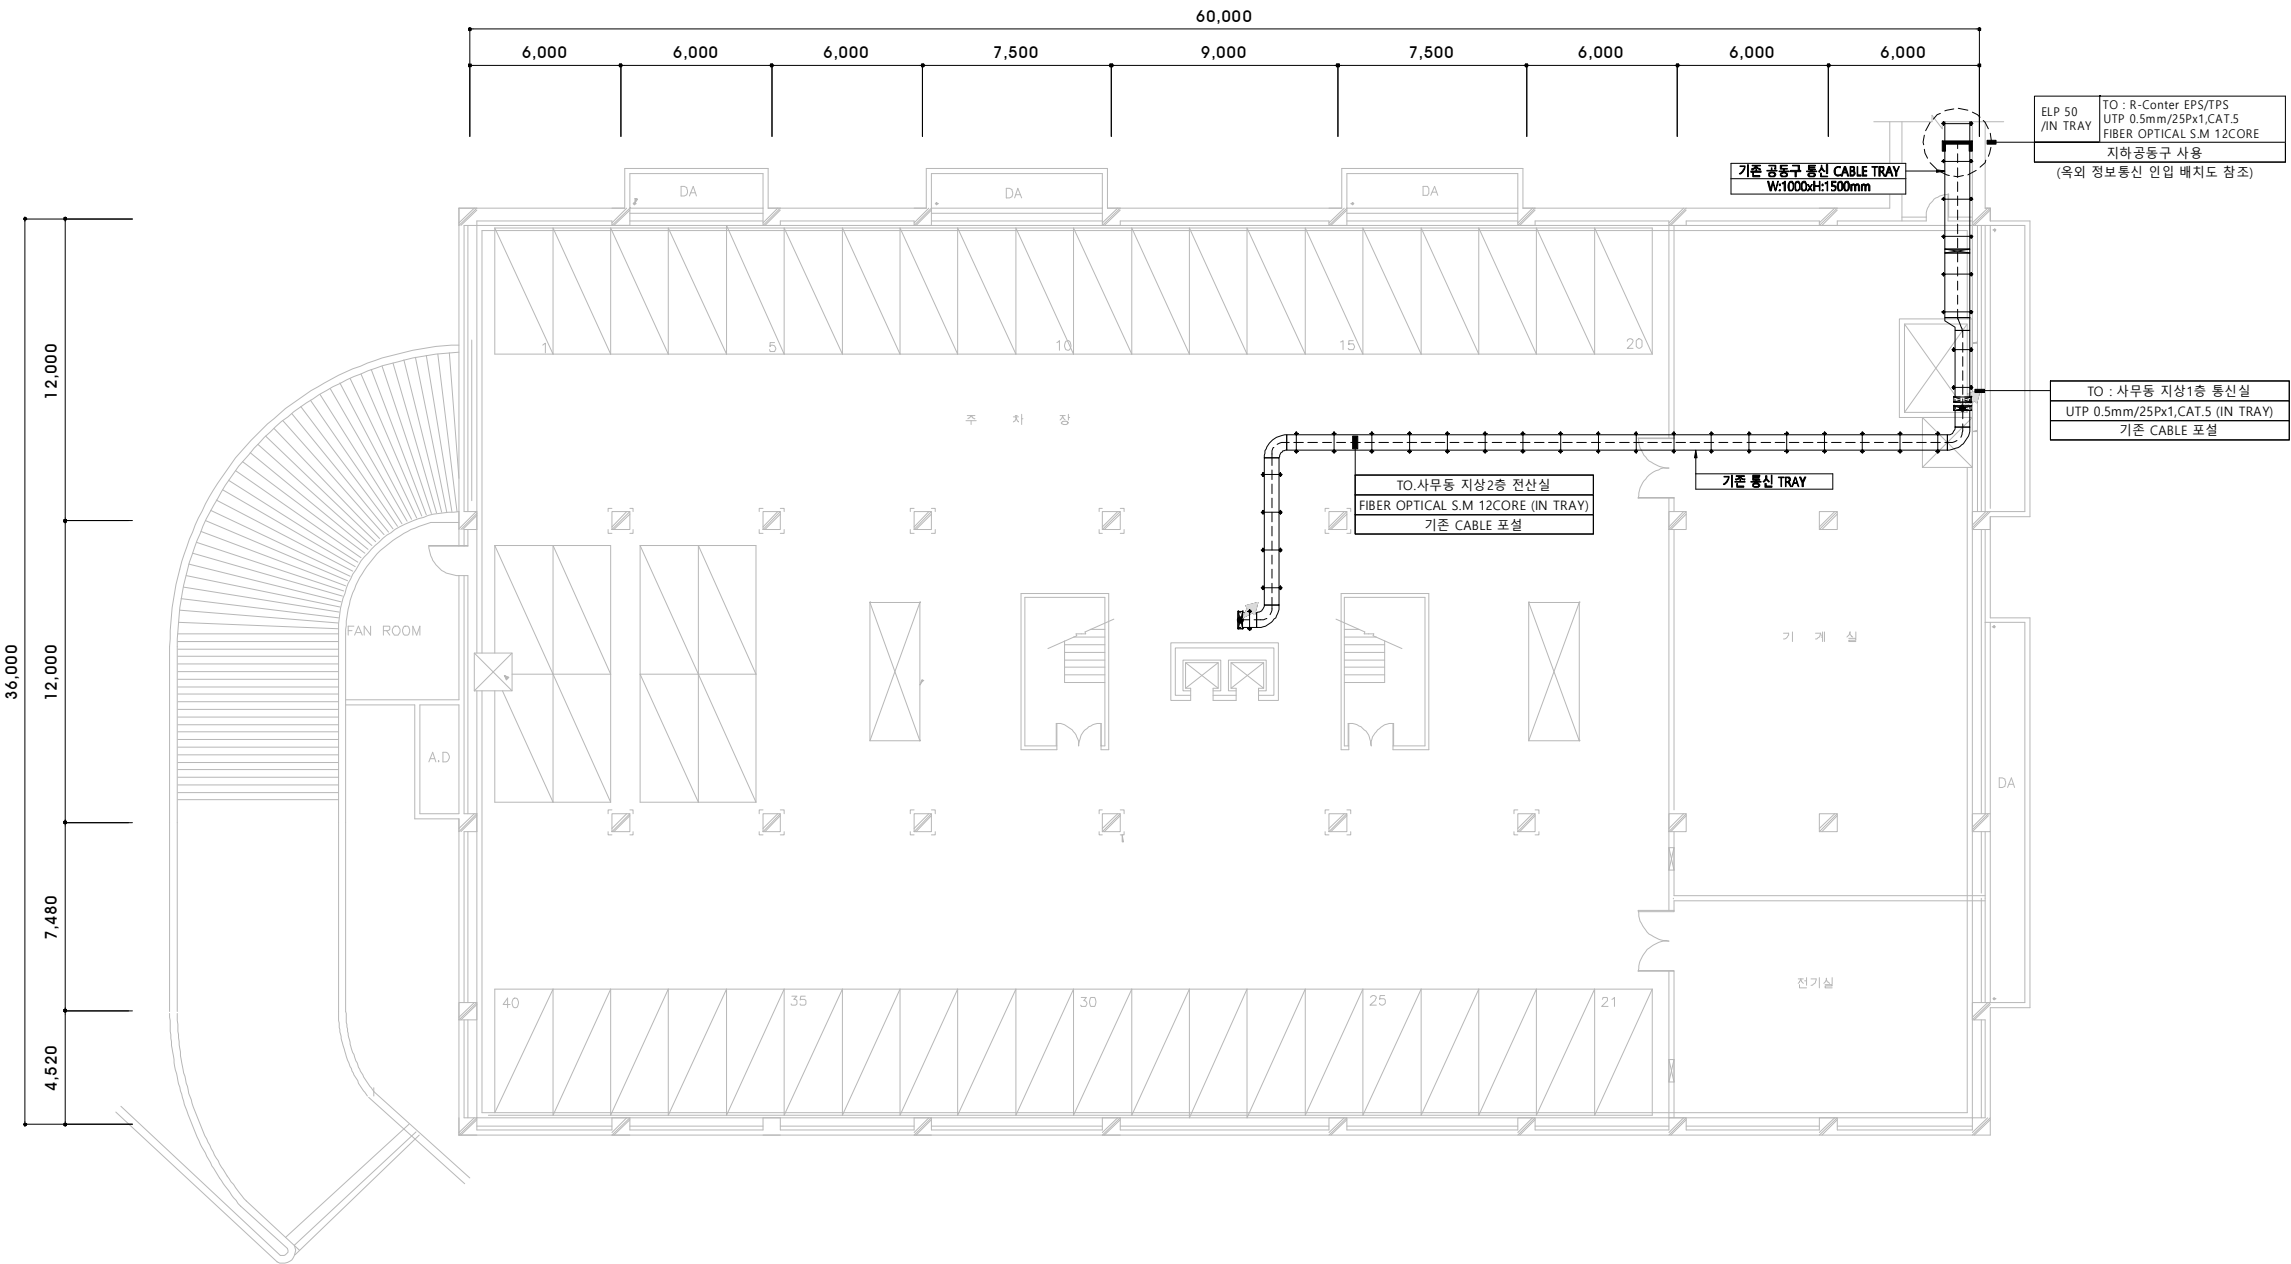

사무동 지하1층 정보통신 설비 평면도

축척: A1 : 1/150
A3 : 1/300

전력시설물종합설계업 제서울 E-1-055호
엔지니어링 활동주체 제06-378호
전기·정보통신 설계·감리 및 소방설계
JM(주) 정명기술단
대표·기술사 이정환

엔지니어링활동주체신고증 신고번호 제 06-378호
기술무류: 통신·정보처리, 전문분야: 정보통신
JM(주) 정명기술단
통신설로산업기사 김근식

LS Electric
R-Center 구축

PROJECT NUMBER
624001

DESIGN CONSULTANT
가운 건축
GAUN | Architects & Engineers

서울시 강남구 언주로 141길 6. 5층 (논현동, 박양빌딩)
Tel: 82-2-3443-7799 Fax: 82-2-3443-3807
www.gaun.co.kr

NOTES

KEY PLAN

△		
△		
△		
△		
△		
△		
△		
△		

NO.	DESCRIPTION	DATE
-----	-------------	------

ISSUES & REVISIONS

BUILDING NAME


DRAWING TITLE

사무동 지상1층
정보통신 설비 평면도

DRAWN	SCALE
CHECK 1 안 동 식	A3 : 1/150 A3 : 1/300
CHECK 2 이 은 진	DATE
APPR 정 용 재	2024.04

DRAWING NO.

ET-01-006

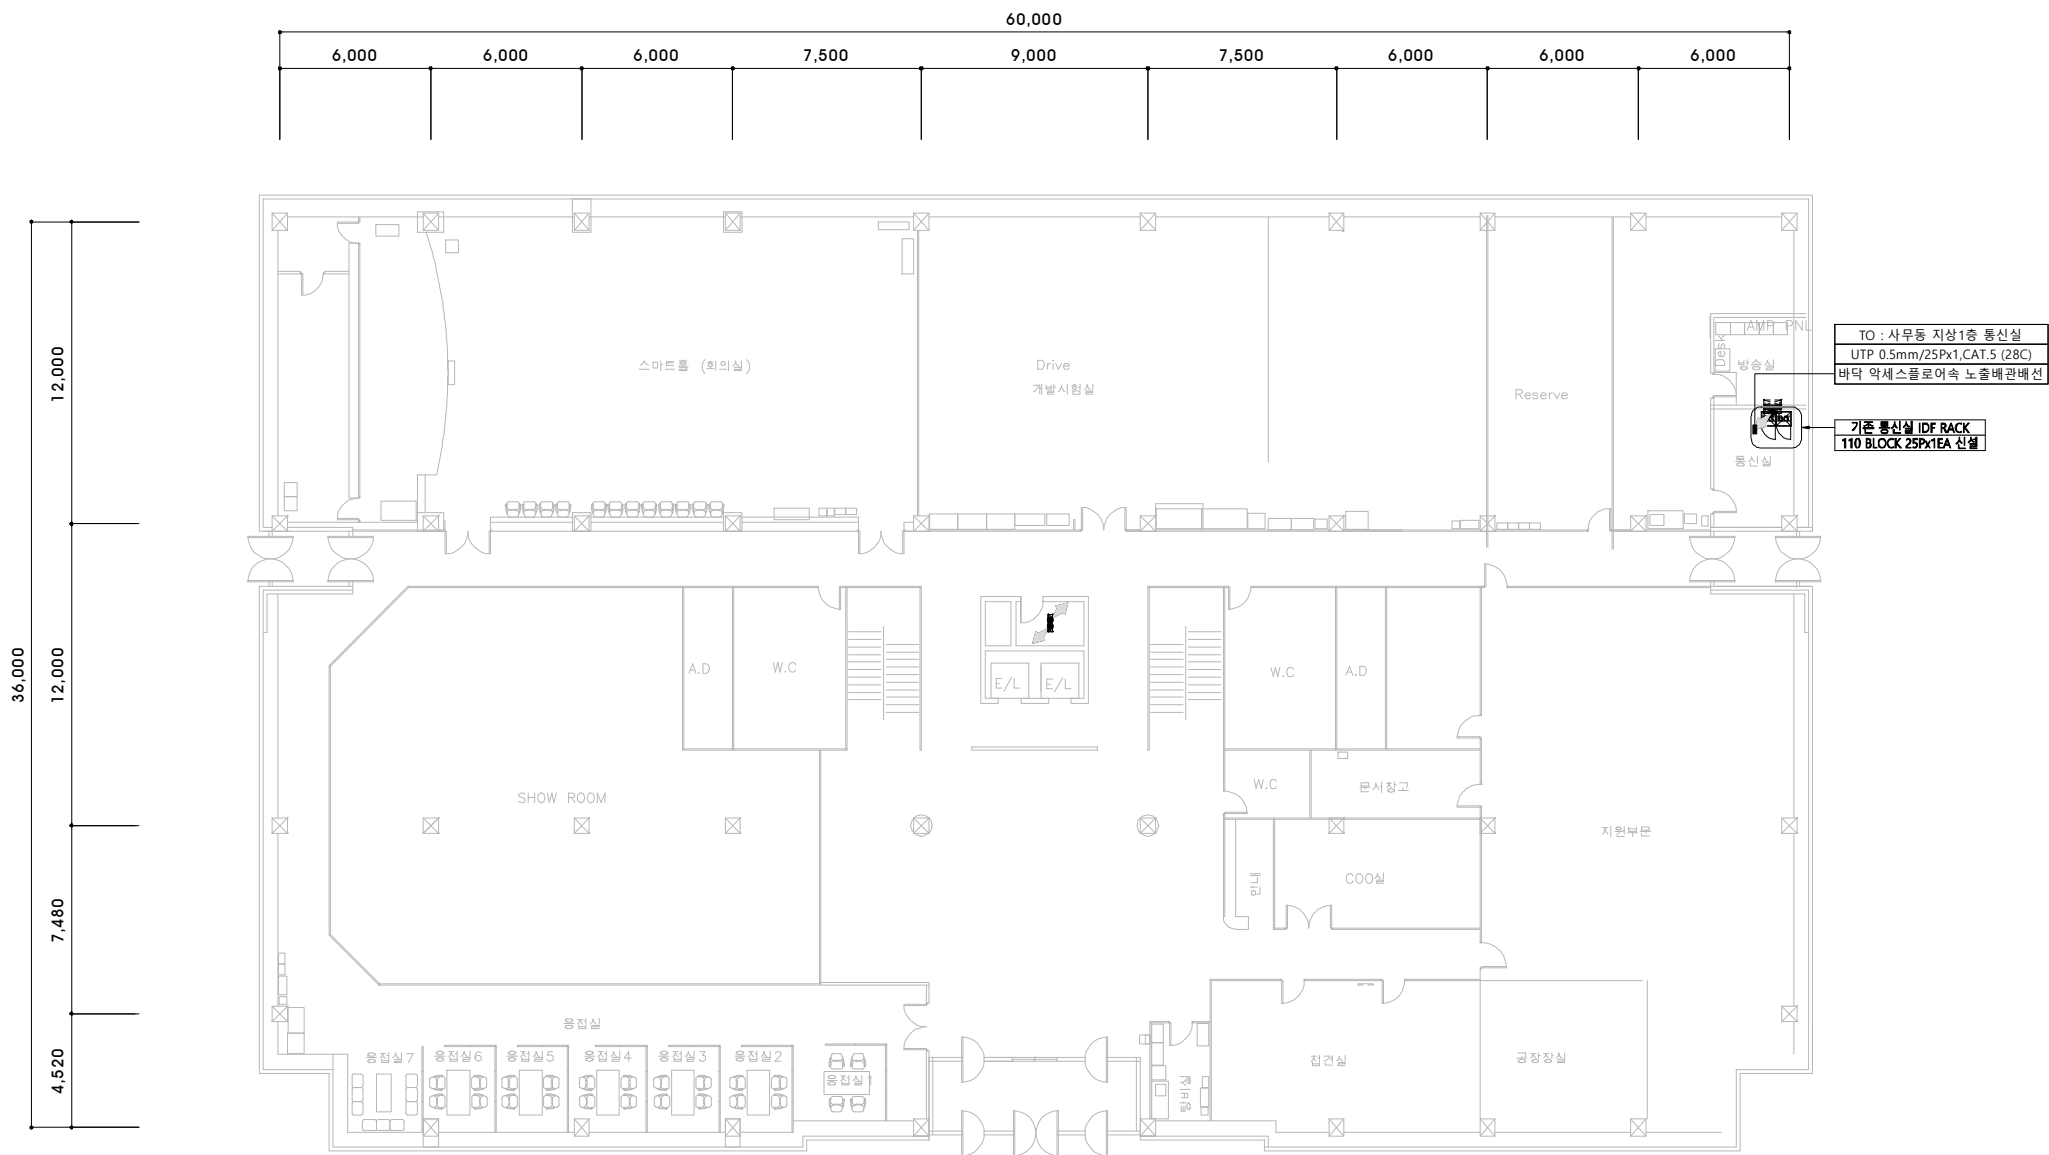

사무동 지상1층 정보통신 설비 평면도

축척: A1 : 1/150
A3 : 1/300

전력시설물종합설계업 제서울 E-1-055호
엔지니어링 활동주체 제06-378호
전기·정보통신 설계·감리 및 소방설계
JM(주) 정명기술단
대표·기술사 이 정 환

엔지니어링활동주체신고증 신고번호 제 06-378호
기술무류: 통신·정보처리, 전문분야: 정보통신
JM(주) 정명기술단
통신설비산업기사 김 근 식

PROJECT TITLE

LS Electric
R-Center 구축

PROJECT NUMBER

624001


DESIGN CONSULTANT

가운 건축

GAUN | Architects & Engineers

GAUN | Architects & Engineers

NOTES

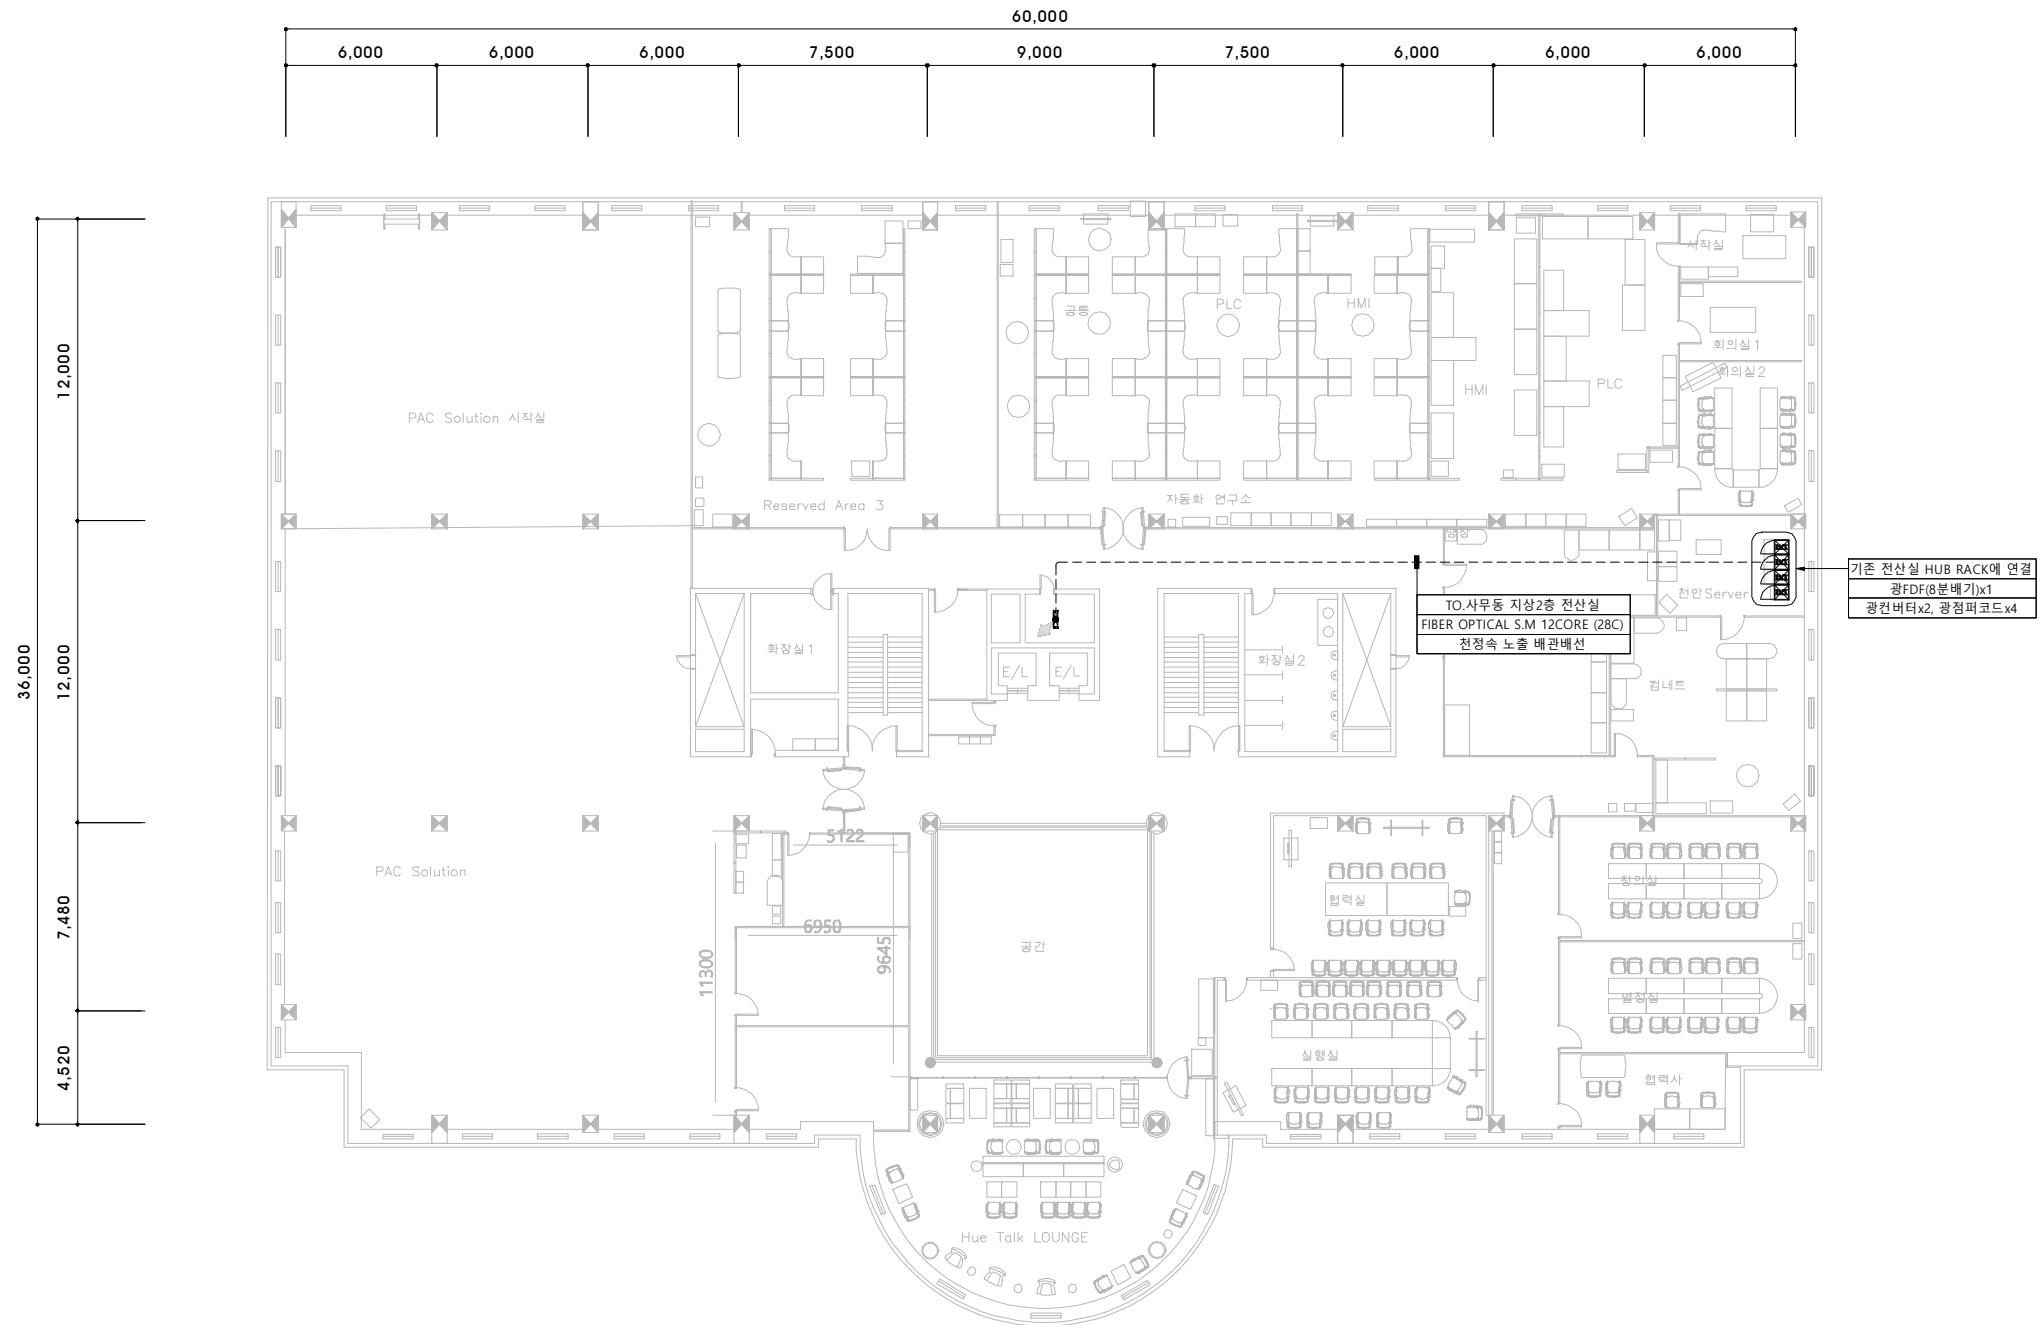

전력시설종합설계업 제서울 E-1-055호
엔지니어링 활동주체 제06-378호
전기·정보통신 설계, 감리 및 소방설계
JM(주) 정명기술단
대표·기술사 이 정 환

전지니어링활동주최신고중 신고번호:제 06-378호
기술부분:통신·정보처리,전문분야:정보통신
JM(주) 정명기술단
통신선로산업기사 김근식

DRAWING TITLE

사무동 지상2층
정보통신 설비 평면도

DRAWN	SCALE
CHECK 1 안 동 식	A3 : 1/150 A3 : 1/300

DRAWING NO.

ET-01-007

DRAWING NO.

ET-01-007

사무동 지상2층 정보통신 설비 평면도

축척:A1 : 1/150
A3 : 1/300

방송용 CABLE SCHEDULE

NO	CABLE & CONDUIT SIZE	REMARKS
(Fa)	28C (F-FR-8 2C/1.5sq)	
(Fb)	28C (F-FR-8 4C/1.5sq)	
(Fc)	28C (F-FR-8 6C/1.5sq)	
(Fd)	28C (F-FR-8 8C/1.5sq)	
(Fe)	36C (F-FR-8 10C/1.5sq)	
(Ff)	36C (F-FR-8 12C/1.5sq)	
(Fg)	36C (F-FR-8 15C/1.5sq)	
(Fh)	42C (F-FR-8 20C/1.5sq)	
(Fi)	54C (F-FR-8 30C/1.5sq)	
(F)	ELP 50Ø(FR-8 10C/2.5sq)	



1.  : 층간 방화 구획 처리.
2. CABLE TRAY내 배관,배선시 전선관을 제외한 CABLE만 포설한다.
3. CABLE TRAY내 공통 접지선은 1-GV 6sq로 한다.
4. CABLE TRAY 통신용과 공용임
5. 방화구획을 관통하는 부위에는 불연재의 방화재로 완전 방화구획이 되도록 차폐한다.

▼ 지붕층 F.L

▼ 2층 F.L

▼ 1층 F.L

▼ PIT층 F.L

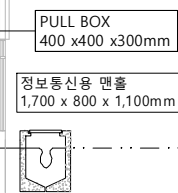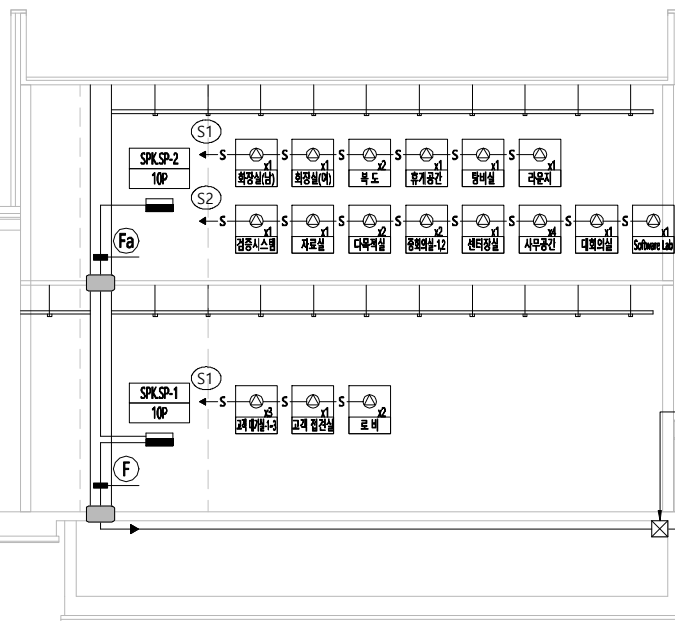

ELP 50 /IN TRAY FROM : 사무동 지상1층 방송실 FR-3 2.5sq / 10C 지하공동구 사용

방송설비 계통도

축척:A1 : 1/NONE
A3 : 1/NONE

전력시설물종합설계업 제서울 E-1-055호
엔지니어링 활동주체 제06-378호
전기·정보통신 설계·감리 및 소방설계
JM(주) 정명기술단
대표·기술사 이 정 환

엔지니어링활동주체신고증 신고번호 제 06-378호
기술부문:통신·정보처리,전문분야:정보통신
JM(주) 정명기술단
통신설비산업기사 김 근 식

PROJECT TITLE

LS Electric
R-Center 구축

PROJECT NUMBER

624001

DESIGN CONSULTANT

가운 건축

GAUN | Architects & Engineers

서울시 강남구 언주로 141길 6. 5층 (논현동, 벅함빌딩)
Tel:82-2-3443-7799 Fax:82-2-3443-3807
www.gaun.co.kr

NOTES

KEY PLAN

NO. DESCRIPTION DATE

ISSUES & REVISIONS

BUILDING NAME

DRAWING TITLE

방송설비 계통도

DRAWN

CHECK 1 안 동 식

CHECK 2 이 은 진

APPR 정 용 재

DRAWING NO.


SCALE

A3 : 1/NONE
A3 : 1/NONE

DATE

2024.04

ET-02-001

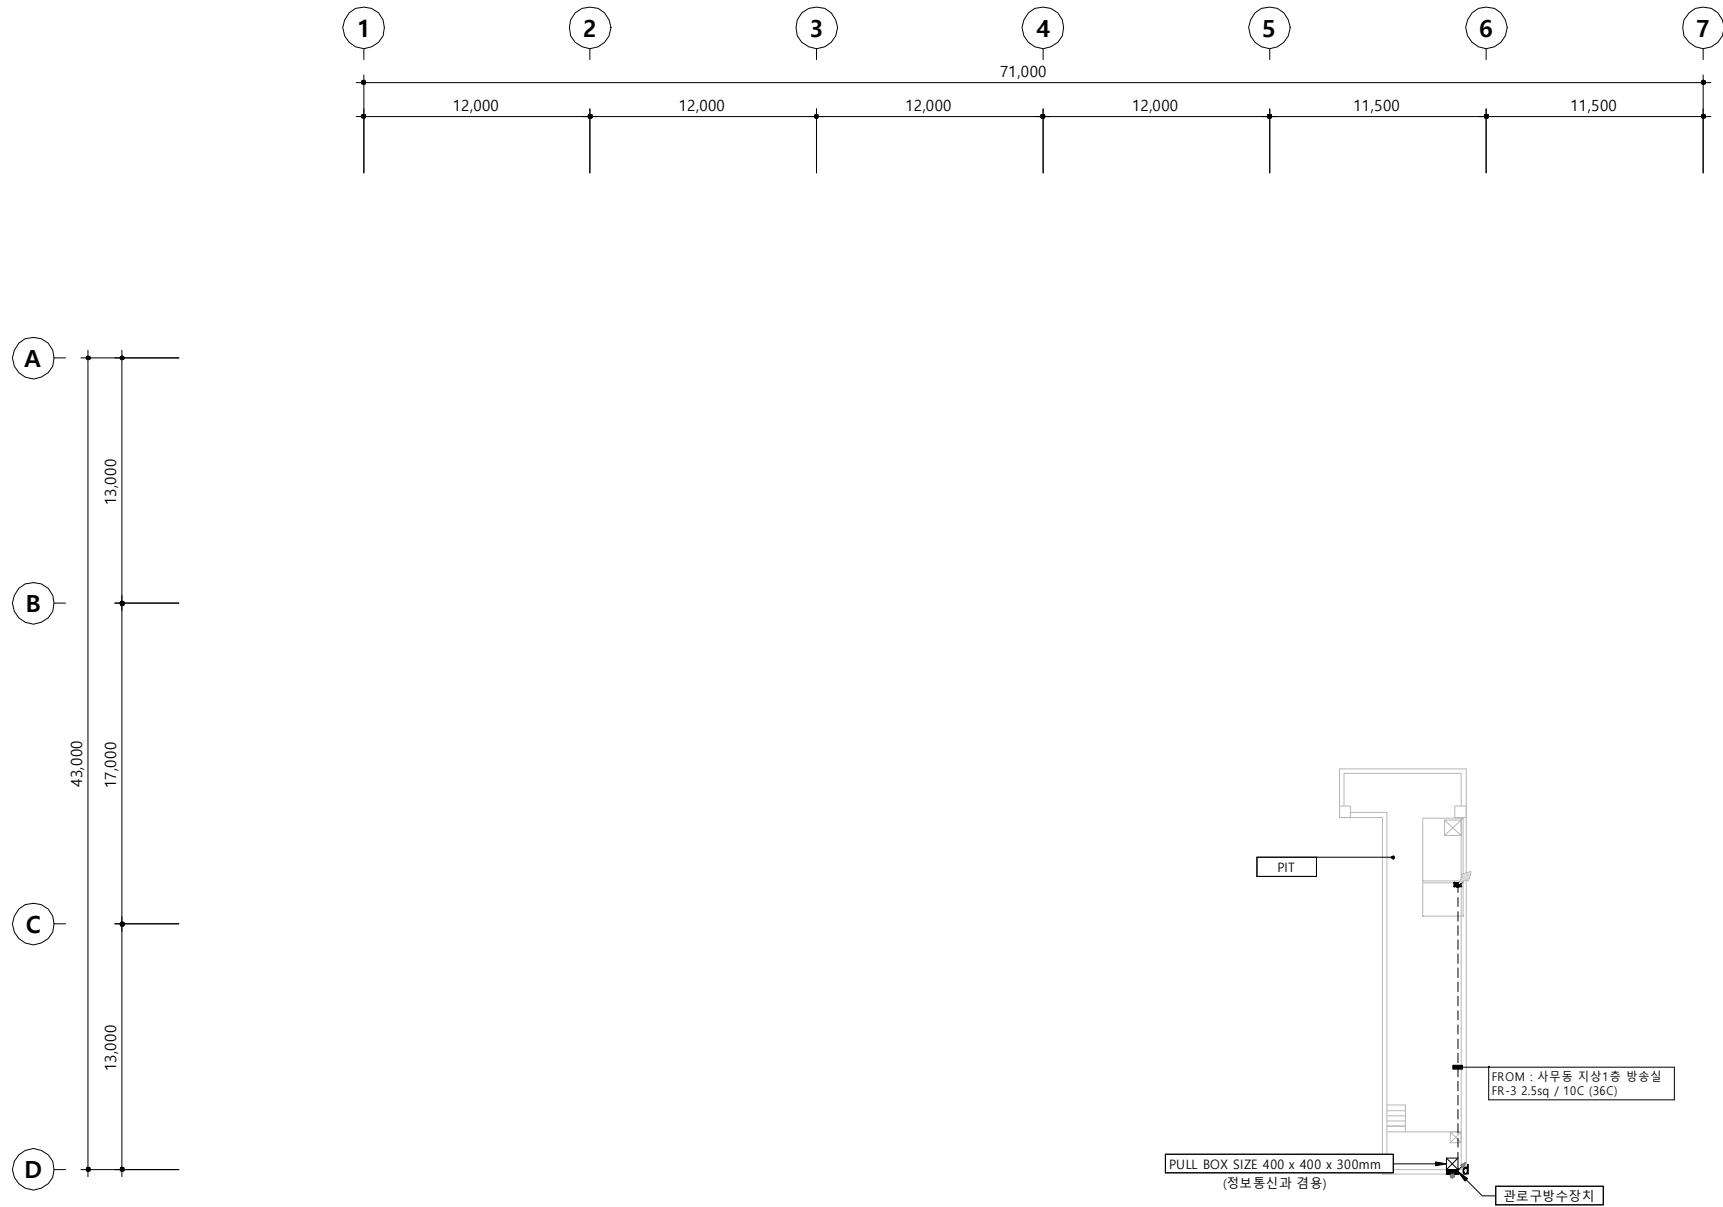

PIT층 방송 설비 평면도

축척:A1 : 1/200
A3 : 1/400

NOTE

1. 배관 배선
——— : 슬라브 매입 배관 배선
- - - - : 노출 배관 배선
——— : 바닥 은폐 및 지중 매설 배관 배선
- - - - : CABLE TRAY내 배선
2. 방송용 배관, 배선
—S— : 16C (HFIX 2-1.5sq)
—S// : 16C (HFIX 3-1.5sq)
—S/// : 16C (HFIX 4-1.5sq)
3. LEGEND
■ : SPEAKER 단자함
⊙ : 스피커 천정형 (3W)
(SPEAKER-CEILING TYPE)
⊙ : 철형형 SPEAKER (3W)
(SPEAKER-WALL BRACKET TYPE)
⊙ : 철형형 SPEAKER (10W)
(SPEAKER-WALL BRACKET TYPE)
☒_a : PULL BOX SIZE 150 x 150 x 100mm
☒_b : PULL BOX SIZE 200 x 200 x 150mm
☒_c : PULL BOX SIZE 300 x 300 x 200mm
☒_d : PULL BOX SIZE 400 x 400 x 300mm
4. 간선 규격 및 기타 사항은 계통도 참조.

LS Electric
R-Center 구축

PROJECT NUMBER
624001

DESIGN CONSULTANT
가운 건축
GAUN | Architects & Engineers

서울시 강남구 언주로 141길 6. 5층 (논현동, 박양빌딩)
Tel:82-2-3443-7799 Fax:82-2-3443-3807
www.gaun.co.kr

NOTES

KEY PLAN

△		
△		
△		
△		
△		
△		
△		
△		
NO.	DESCRIPTION	DATE

ISSUES & REVISIONS

BUILDING NAME

DRAWING TITLE

PIT층 방송 설비 평면도




DRAWN	SCALE
CHECK 1 안 동 식	A3 : 1/200 A3 : 1/400
CHECK 2 이 은 진	DATE
APPR 정 용 재	2024.04

DRAWING NO.

ET-02-002

전력시설물종합설계업 제서울 E-1-055호
엔지니어링 활동주체 제06-378호
전기·정보통신 설계·감리 및 소방설계
JM(주) 정 명 기 술 단
대표·기술사 이 정 환

엔지니어링활동주체신고증 신고번호제 06-378호
기술무류:통신·정보처리,전문분야:정보통신
JM(주) 정 명 기 술 단
통신설로산업기사 김 근 식

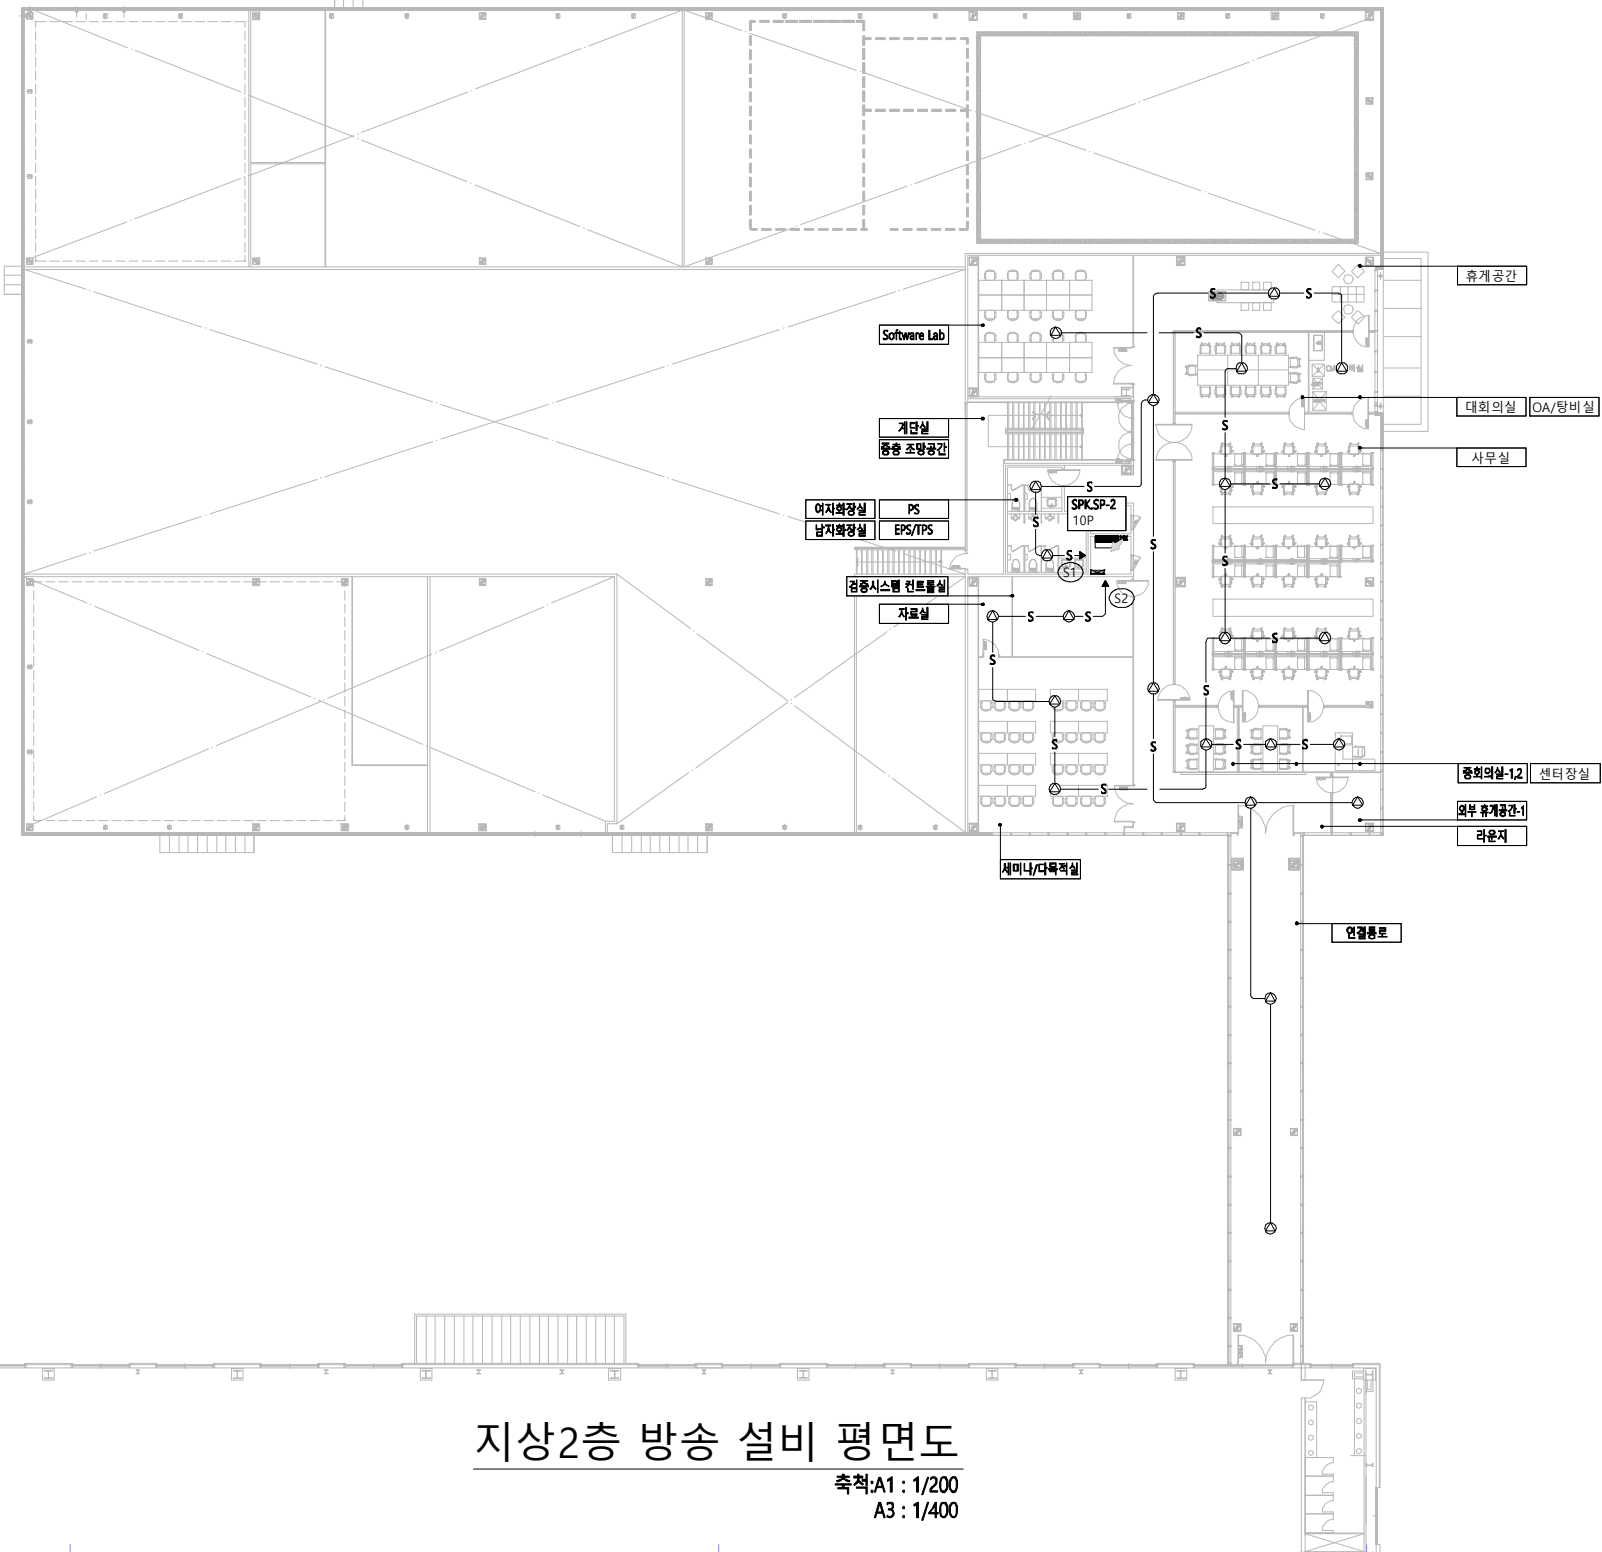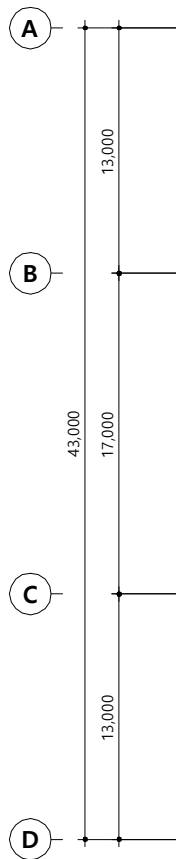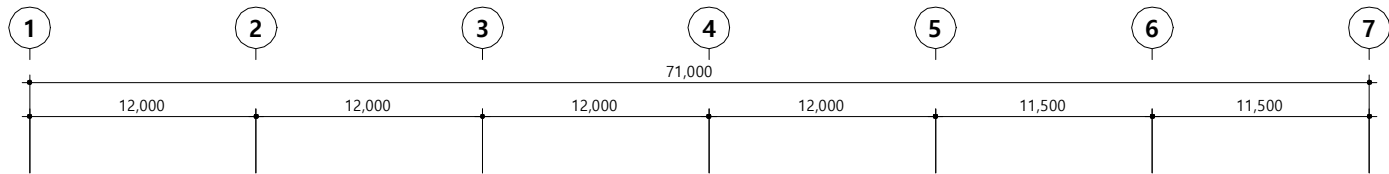

NOTE

1. 배관 배선
——— : 슬라브 매입 배관 배선
- - - - : 노출 배관 배선
——— : 바닥 은폐 및 지중 매설 배관 배선
- - - - : CABLE TRAY내 배선

2. 방송용 배관, 배선
—S— : 16C (HFIX 2-1.5sq)
—S//— : 16C (HFIX 3-1.5sq)
—S///— : 16C (HFIX 4-1.5sq)

3. LEGEND
■ : SPEAKER 단자함
⊙ : 스피커 천정형 (3W)
(SPEAKER-CEILING TYPE)
⊙ : 철형형 SPEAKER (3W)
(SPEAKER-WALL BRACKET TYPE)
⊙ : 철형형 SPEAKER (10W)
(SPEAKER-WALL BRACKET TYPE)
☒_a : PULL BOX SIZE 150 x 150 x 100mm
☒_b : PULL BOX SIZE 200 x 200 x 150mm
☒_c : PULL BOX SIZE 300 x 300 x 200mm
☒_d : PULL BOX SIZE 400 x 400 x 300mm

4. 간선 규격 및 기타 사항은 계통도 참조.

PROJECT TITLE
LS Electric
R-Center 구축

PROJECT NUMBER
624001

DESIGN CONSULTANT
가운 건축
GAUN | Architects & Engineers
서울시 강남구 언주로 141길 6. 5층 (논현동, 벡스코빌딩)
Tel:82-2-3443-7799 Fax:82-2-3443-3807
www.gaun.co.kr

NOTES

KEY PLAN

△		
△		
△		
△		
△		
△		
△		
△		
NO.	DESCRIPTION	DATE

ISSUES & REVISIONS


BUILDING NAME

DRAWING TITLE
지상2층 방송 설비 평면도

DRAWN	SCALE
CHECK 1 안 동 식	A3 : 1/200 A3 : 1/400
CHECK 2 이 은 진	DATE
APPR 정 용 재	2024.04
DRAWING NO.	ET-02-004

전력시설물종합설계업 제서울 E-1-055호
엔지니어링 활동주체 제06-378호
전기·정보통신 설계·감리 및 소방설계
JM(주) 정 명 기 술 단
대표·기술사 이 정 환

엔지니어링활동주체신고증 신고번호제 06-378호
기술무류:통신·정보처리,전문분야:정보통신
JM(주) 정 명 기 술 단
통신선로산업기사 김 근 식

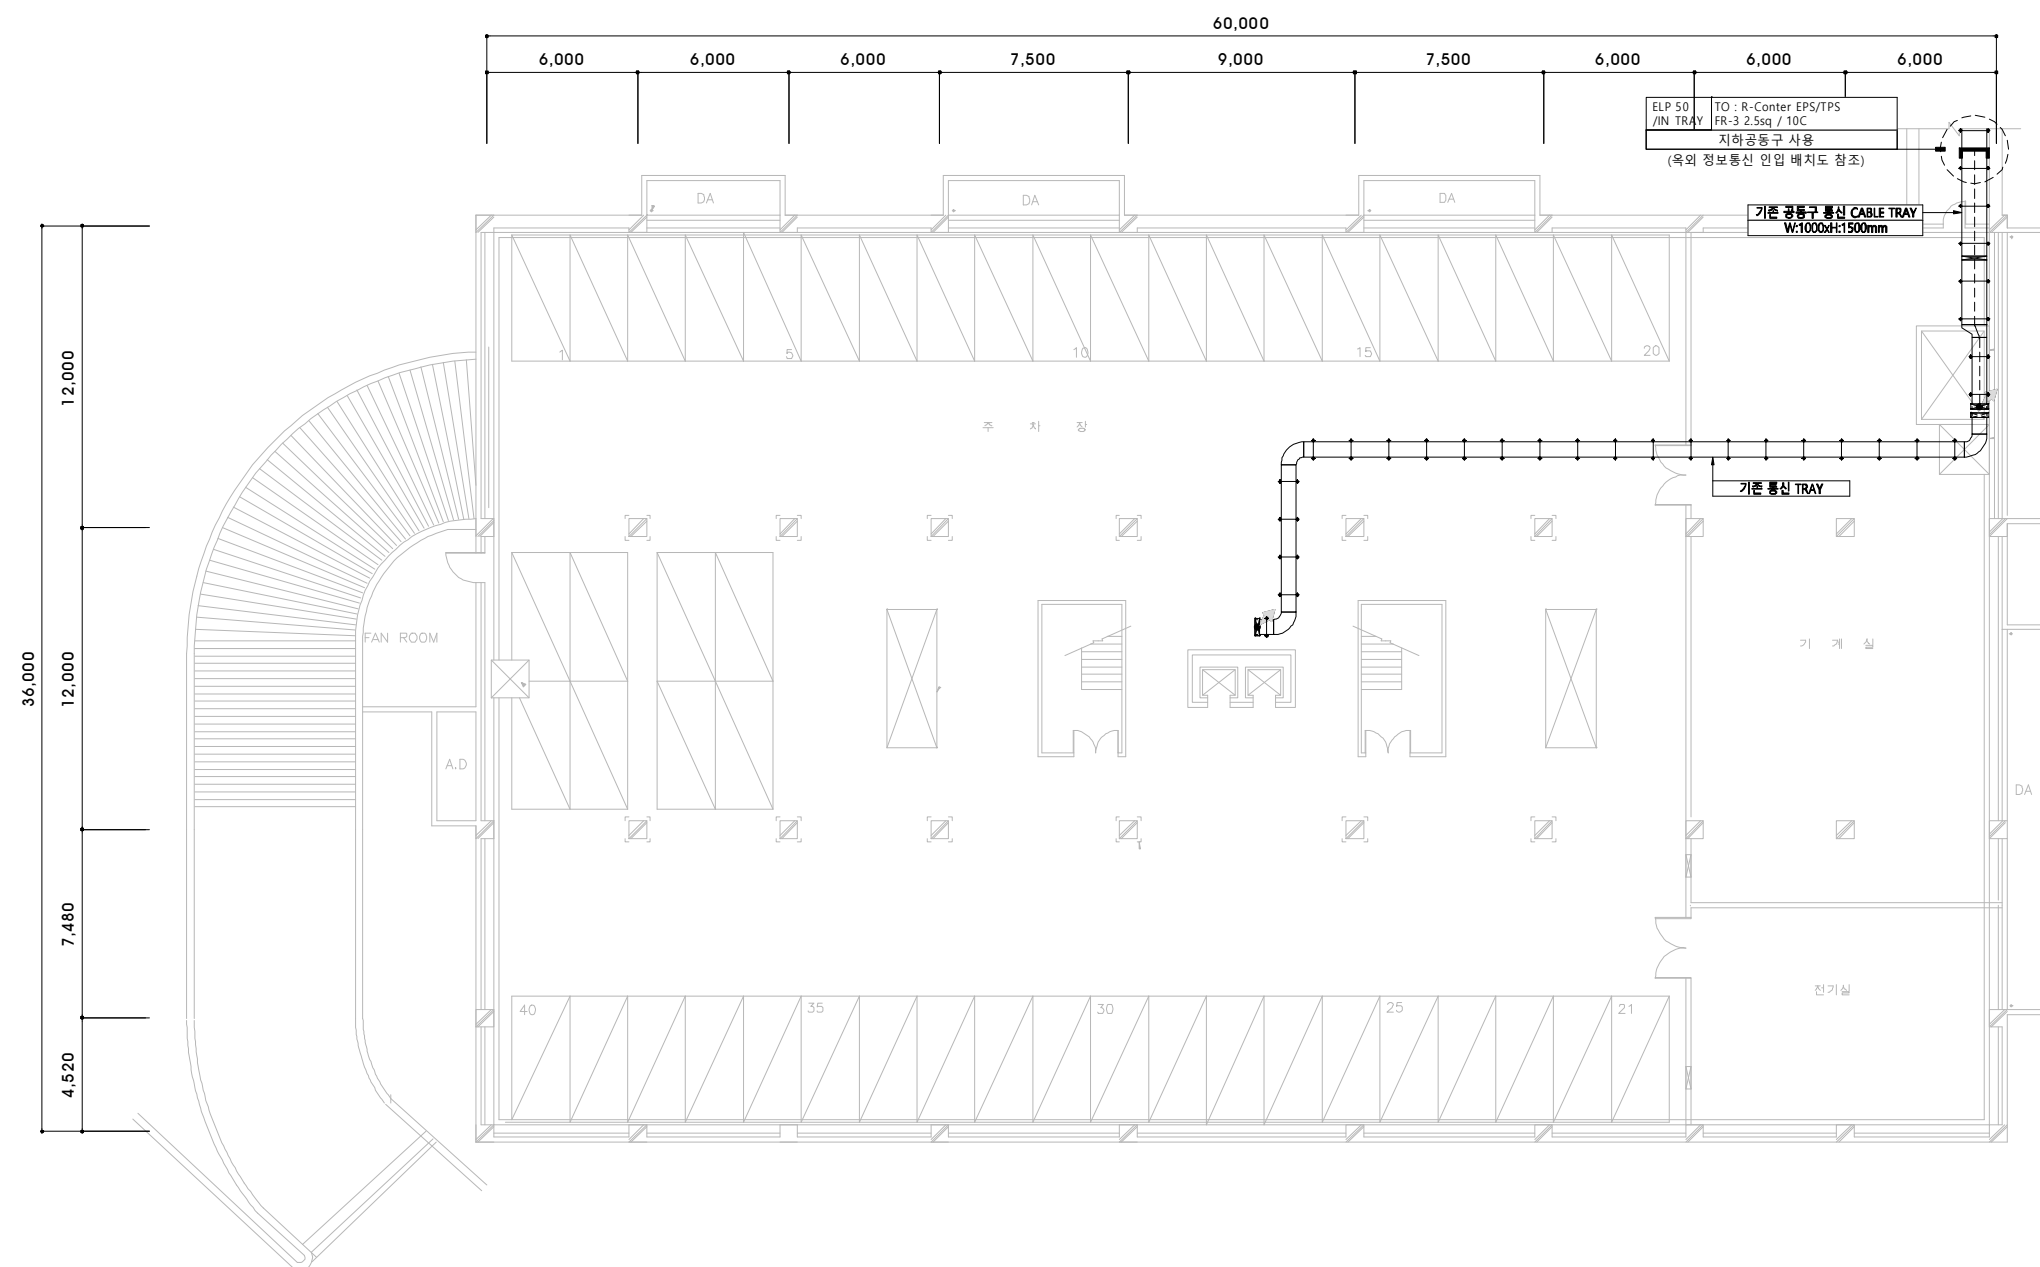

NOTE

1. 배관 배선
 _____ : 슬라브 매입 배관 배선
 ----- : 노출 배관 배선
 : 바닥 은폐 및 지중 매설 배관 배선
 : CABLE TRAY내 배선
2. 방송용 배관, 배선
 — S ——— : 16C (HFIX 2-1.5sq)
 — S /// : 16C (HFIX 3-1.5sq)
 — S /// : 16C (HFIX 4-1.5sq)

3. LEGEND
-  : SPEAKER 단자함
 -  : 스피커 천정형 (3W)
(SPEAKER-CEILING TYPE)
 -  : 컬럼형 SPEAKER (3W)
(SPEAKER-WALL BRACKET TYPE)
 -  : 컬럼형 SPEAKER (10W)
(SPEAKER-WALL BRACKET TYPE)
 - ☒_a : PULL BOX SIZE 150 x 150 x 100mm
 - ☒_b : PULL BOX SIZE 200 x 200 x 150mm
 - ☒_c : PULL BOX SIZE 300 x 300 x 200mm
 - ☒_d : PULL BOX SIZE 400 x 400 x 300mm
4. 간선 규격 및 기타 사항은 계통도 참조.

4. 간선 규격 및 기타 사항은 계통도 참조.

LS Electric
R-Center 구축

PROJECT NUMBER

DESIGN CONSULTANT

가운 건축

GAUN | Architects & Engineers

서울시 강남구 언주로 141길 6.5층 (논현동, 백향빌딩)
Tel:82-2-3443-7799 Fax:82-2-3443-3807
www.gaun.co.kr

NOTES

NO.	DESCRIPTION	DATE
-----	-------------	------

BUILDING NAME

DRAWING TITLE

사무동 지하1층
방송 설비 평면도

DRAWN	SCALE
CHECK 1 안 등 식	A3 : 1/150 A3 : 1/300
CHECK 2 이 은 진	DATE
APPR 정 용 재	2024.04


ET-02-005

전력시설종합설계업 제서울 E-1-055호
엔지니어링 활동주체 제06-378호
전기·정보통신 설계·감리 및 소방설계
JM(주) 정명기술단
대표·기술사 이 정 환

엔지니어링활동주체신고증 신고번호:제 06-378호
기술부분:통신·정보처리,전문분야:정보통신
JM(주) 정명기술단
통신선로산업기사 김근식

사무동 지하1층 방송 설비 평면도

축척: A1 : 1/150
A3 : 1/300

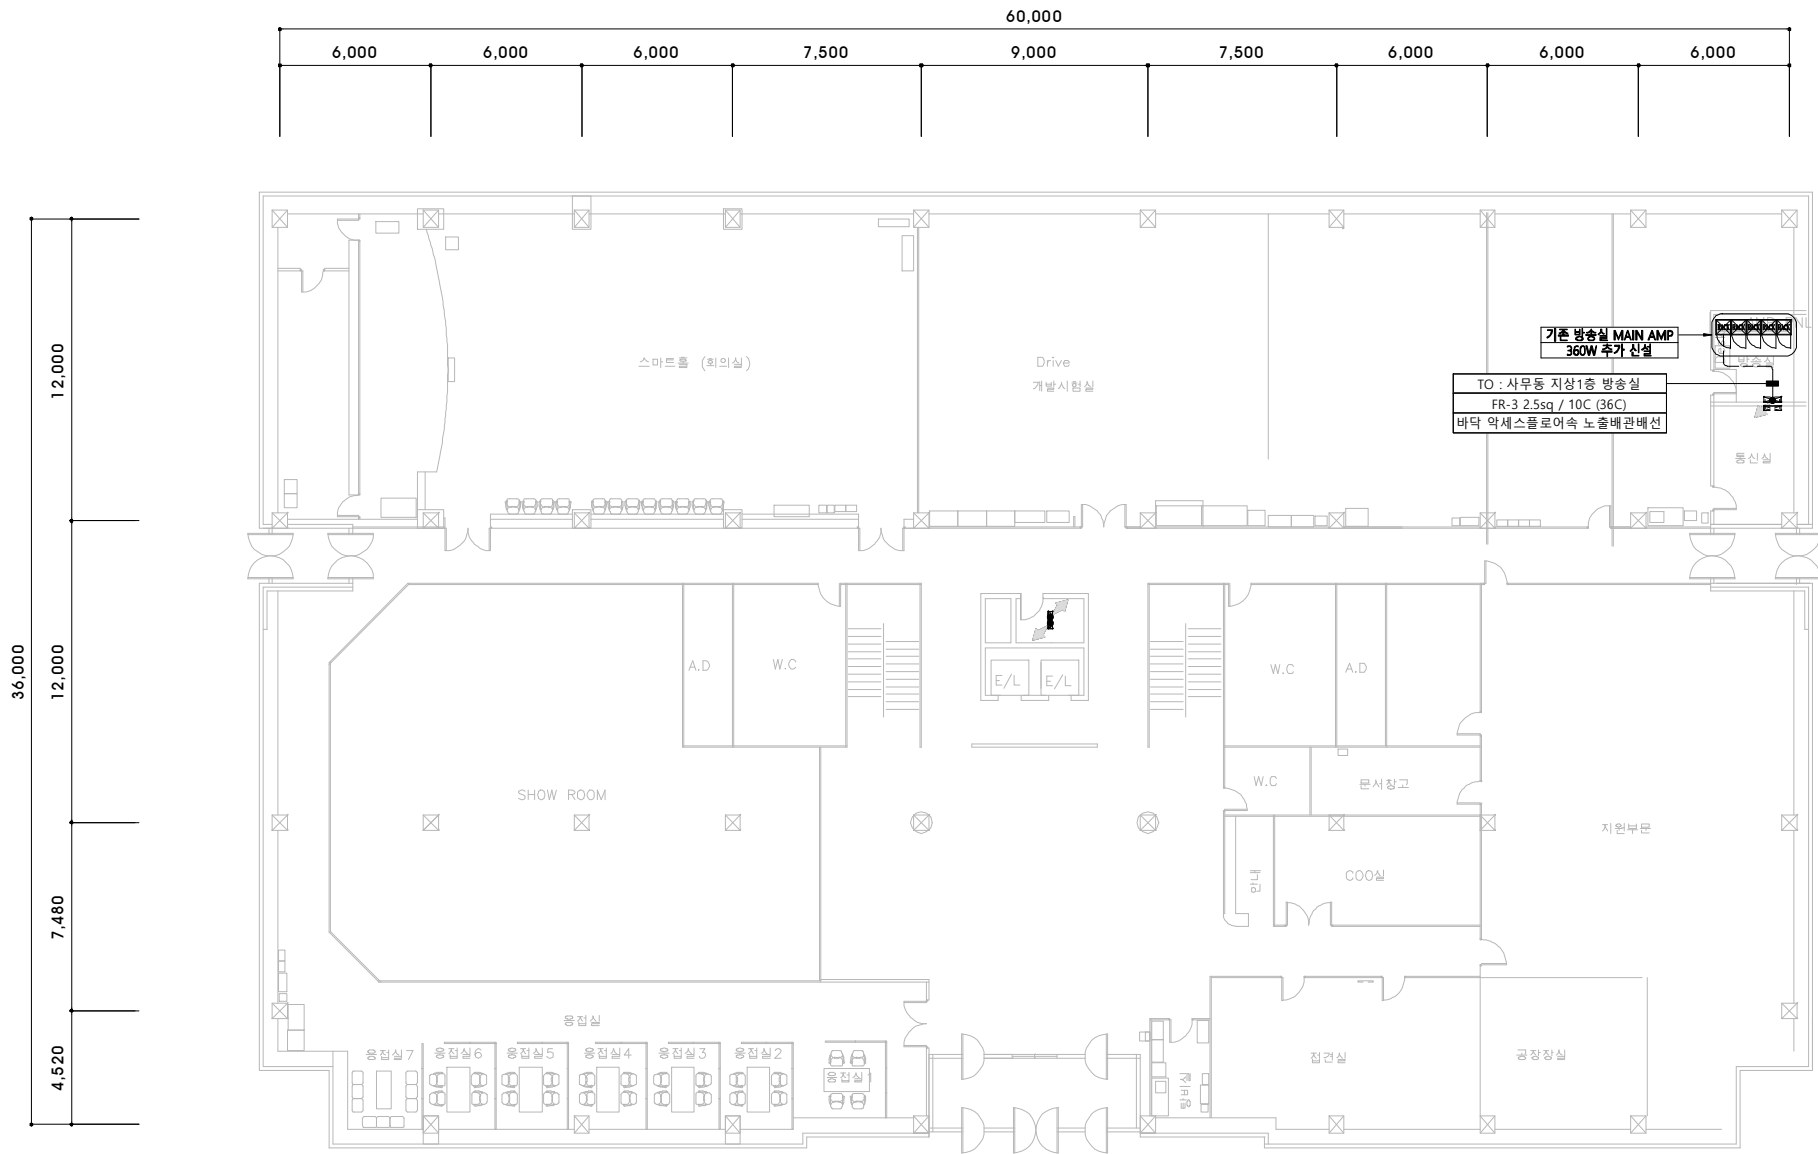

NOTE

1. 배관 배선
—— : 슬라브 매입 배관 배선
----- : 노출 배관 배선
- · - · - : 바닥 은폐 및 지중 매설 배관 배선
- · - · - · - : CABLE TRAY내 배선

2. 방송용 배관, 배선
— S — : 16C (HFIX 2-1.5sq)
— S // : 16C (HFIX 3-1.5sq)
— S /// : 16C (HFIX 4-1.5sq)

3. LEGEND
[Symbol] : SPEAKER 단자함
[Symbol] : 스피커 천정형 (3W)
(SPEAKER-CEILING TYPE)
[Symbol] : 컬럼형 SPEAKER (3W)
(SPEAKER-WALL BRACKET TYPE)
[Symbol] : 컬럼형 SPEAKER (10W)
(SPEAKER-WALL BRACKET TYPE)
[Symbol] a : PULL BOX SIZE 150 x 150 x 100mm
[Symbol] b : PULL BOX SIZE 200 x 200 x 150mm
[Symbol] c : PULL BOX SIZE 300 x 300 x 200mm
[Symbol] d : PULL BOX SIZE 400 x 400 x 300mm

4. 간선 규격 및 기타 사항은 계통도 참조.

사무동 지상1층 방송 설비 평면도

축척:A1 : 1/150
A3 : 1/300

전력시설물종합설계업 제서울 E-1-055호
엔지니어링 활동주체 제06-378호
전기·정보통신 설계·감리 및 소방설계
JM(주) 정명기술단
대표·기술사 이 정 환

엔지니어링활동주체신고증 신고번호 제 06-378호
기술부문:통신·정보처리,전문분야:정보통신
JM(주) 정명기술단
통신선로산업기사 김 근 식

LS Electric
R-Center 구축

PROJECT NUMBER
624001

가운 건축
GAUN | Architects & Engineers

서울시 강남구 언주로 141길 6. 5층 (논현동, 백양빌딩)
Tel:82-2-3443-7799 Fax:82-2-3443-3807
www.gaun.co.kr

NOTES

KEY PLAN

△		
△		
△		
△		
△		
△		
△		
△		
NO.	DESCRIPTION	DATE

ISSUES & REVISIONS

BUILDING NAME

DRAWING TITLE

사무동 지상1층
방송 설비 평면도

DRAWN	SCALE
CHECK 1 안 동 식	A3 : 1/150 A3 : 1/300
CHECK 2 이 은 진	DATE
APPR 정 용 재	2024.04

DRAWING NO.
ET-02-006

LS Electric
R-Center 구축

624001

가운 건축

GAUN | Architects & Engineers

서울시 강남구 언주로 141길 6. 5층 (논현동, 박양빌딩)
Tel:82-2-3443-7799 Fax:82-2-3443-3807
www.gaun.co.kr

NOTES

KEY PLAN

△		
△		
△		
△		
△		
△		
△		
△		
NO.	DESCRIPTION	DATE

ISSUES & REVISIONS

BUILDING NAME


DRAWING TITLE

통합배선설비 구성도

DRAWN	SCALE
CHECK 1 안 동 식	A3 : 1/NONE A3 : 1/NONE
CHECK 2 이 은 진	DATE
APPR 정 용 재	2024.04

DRAWING NO.

ET-03-001

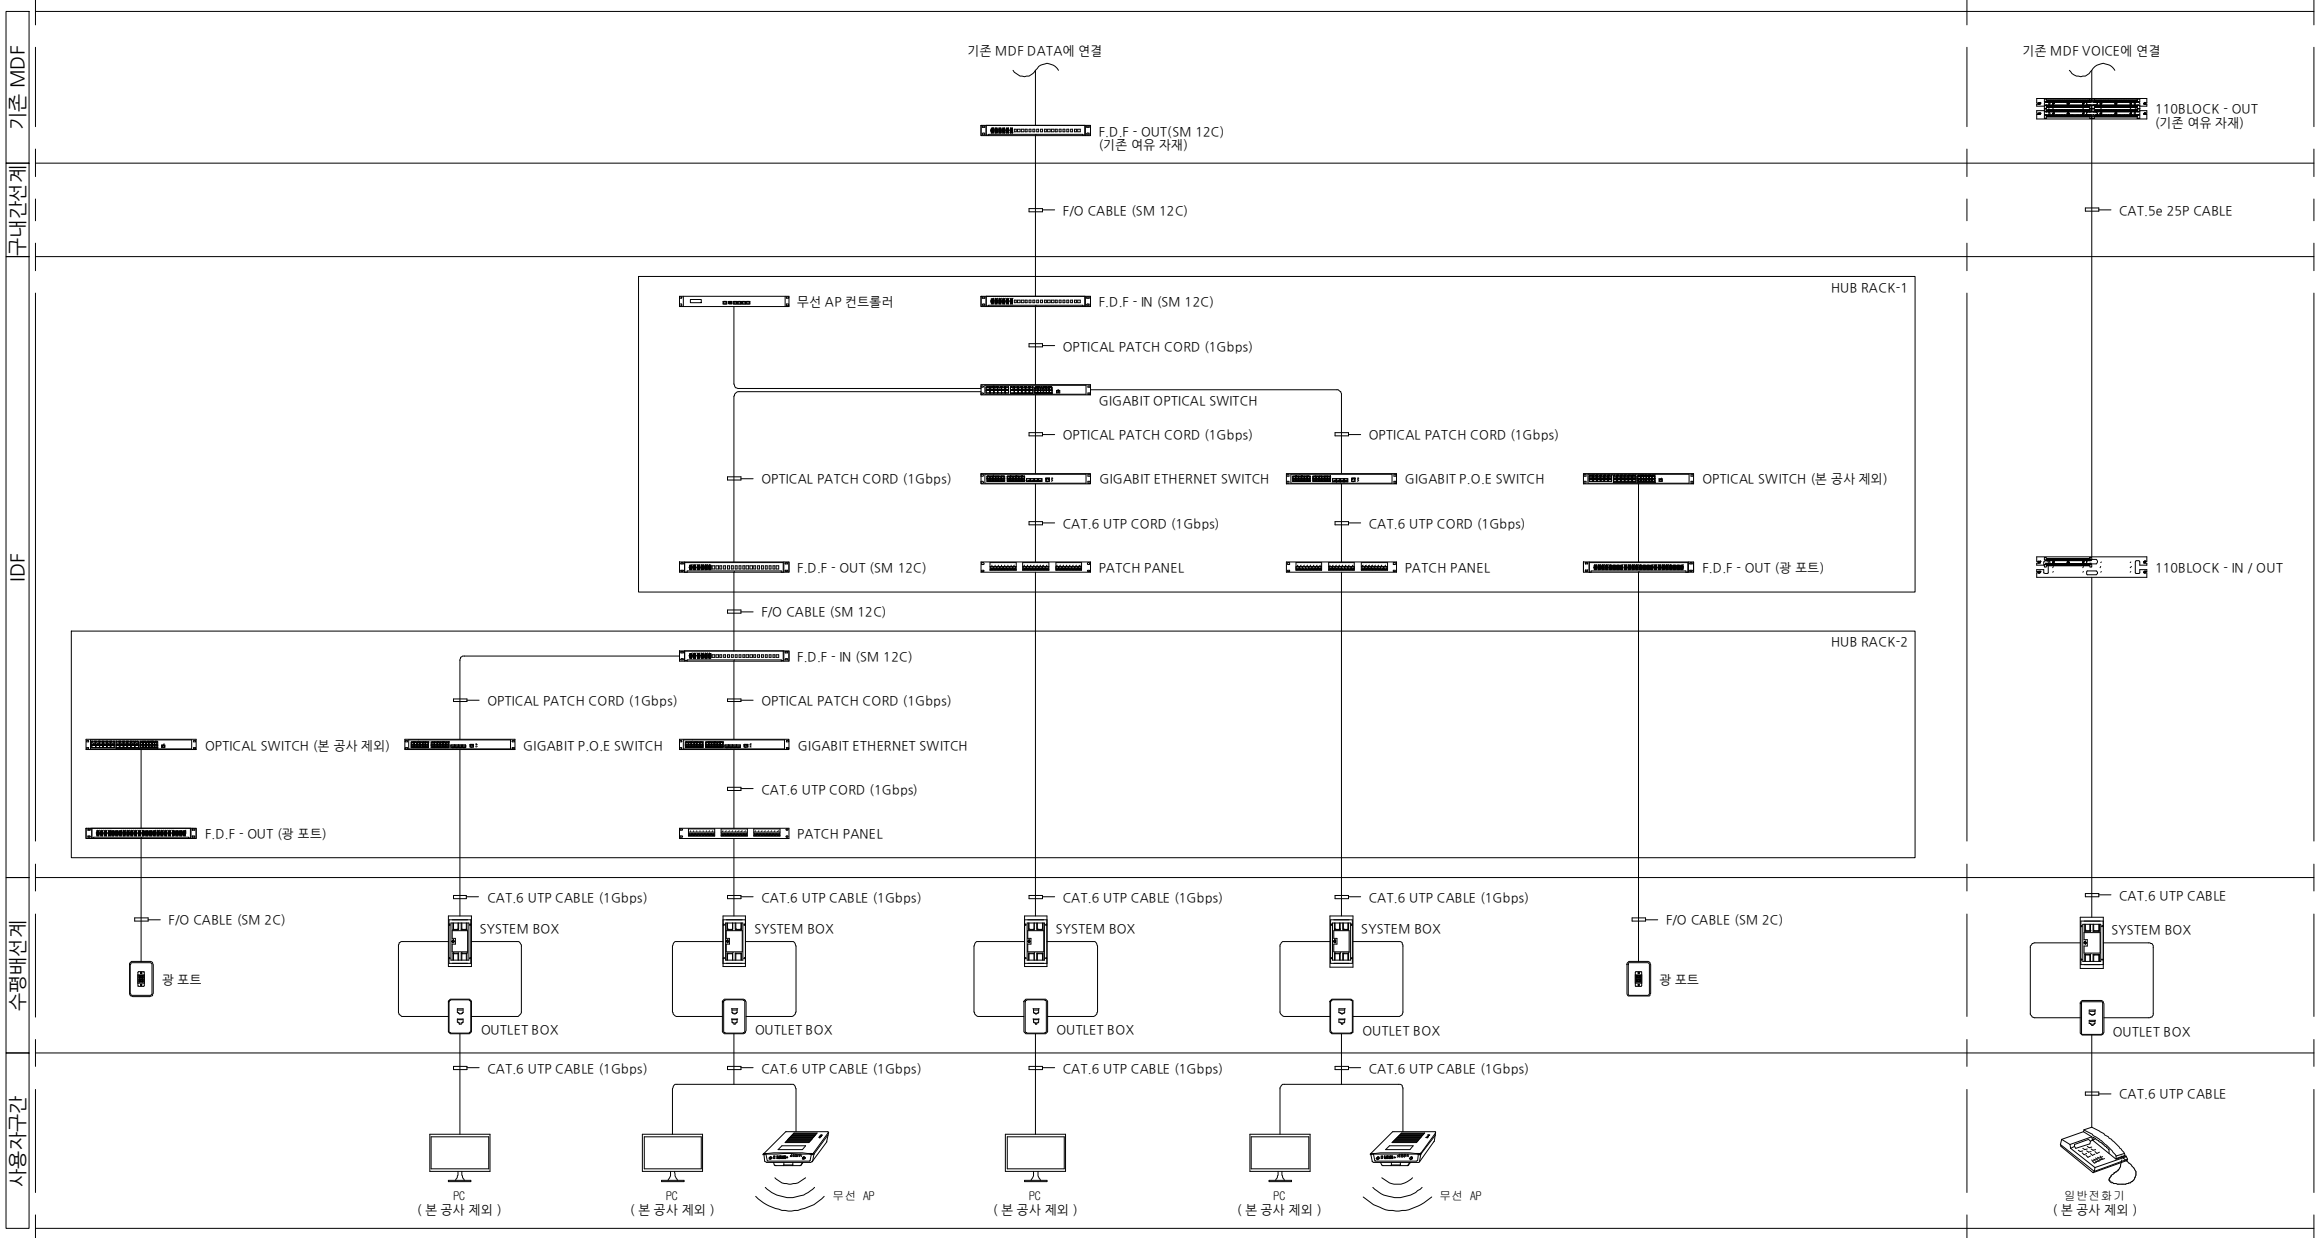

통합배선설비 구성도

축척:A1 : 1/NONE
A3 : 1/NONE

전력시설물종합설계업 제서울 E-1-055호
엔지니어링 활동주체 제06-378호
전기·정보통신 설계·감리 및 소방설계
JM(주) 정명기술단
대표·기술사 이 정 환

엔지니어링활동주체신고증 신고번호 제 06-378호
기술주분:통신·정보처리,전문분야:정보통신
JM(주) 정명기술단
통신설비산업기사 김 근 식

