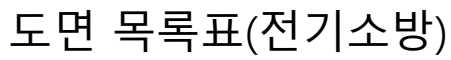


LS ELECTRIC 천안 R-Center 구축설계

- 실시설계 도서 -
[전기소방]

2024.05

(주)가운종합건축사사무소

[illegible]

JUNG YEON (주)정연엔지니어링

건축전문1종설계업등록 [경기안양1-1호]
 건축전문1종설계기사 조 성 환
 전문소방시설설계업등록
 [제2017-01-00097호]
 소방설비기사 홍 기 만
 정보통신등록 [제 E-6-825호]
 정보통신채용기사 황 선 석
 기계설비등록 [제 E-6-825호]
 건축기계설비기사 홍 기 만

경기도 안양시 동안구 흥안대로 415,
 1115호, 1116호 (판문동, 두산벤처다임)
 대 표 전 화 : (031) 456 - 9666

PROJECT TITLE

LS

LS Electric
R-Center 구축

PROJECT NUMBER

224001

DESIGN CONSULTANT

가운 건축

GAUN | Architects & Engineers

| 서울시 강남구 언주로 609, 10층 (논현동, 팍스타워)
Tel:82-2-3443-7799 Fax:82-2-3443-3807
[www.gaun.co.kr](#)

NOTES

KEY PLAN

△		
△		
△		
△		
△		
△		
△		
△		
NO.	DESCRIPTION	DATE
ISSUES & REVISIONS		

BUILDING NAME

R-Center

DRAWING TITLE

도면 목록표(전기소방)

DRAWN	SCALE
CHECK 1 안 동 식	A3:1/NONE
CHECK 2 이 은 진	DATE
APPR 정 용 재	2024.01

DRAWING NO.

EF - 000

소방범례 및 주기사항

구 분	SYMBOL	명 칭 및 규 격	비 고
경 보 설 비		차동식 감지기(2종 스포트형)-LED 부착형	
		정온식 감지기(1종 스포트형)-LED 부착형	
		연기식 감지기(1,2종 광전식)-LED 부착형	
		수동발신기 SET (소화전 상단형)	설치높이:바닥+1500mm(발신기중심)
		화재 수신반	
소화활동설비		SUPER VISORY PANEL	
		스프링클러 PREACTON VALVE	기계설비 공사
		스프링클러경보변 (전자 싸이렌)	90dB 이상
		방화셔터 연동제어반	
피 난 설 비		피난구 유도등 (소형)(중형)(대형)-(LED)	< 고휘도 60분용 >
		피난구 유도등 - 양면형(소형)-(LED)	< 고휘도 60분용 >
		통로 유도등-(LED)	< 고휘도 60분용 >

공 통 설 비		PULL BOX	별도명기없는것-100x100x50
		유도등, 비상콘센트 전원 공급용 분전반	
		감지기용 배관배선	
		유도등용 배관배선	
		천정 SLAB 매입 배관배선	
		바닥 SLAB 매입 배관배선	
		지중 매입 배관배선	
		천정 노출 및 은폐 배관배선	
		분전반 및 단자반으로 향하는 귀로	
		전선관 입상, 입하, 통과표시	

구 분	배관 배선 및 주기사항		
감지기용 배관 배선		16C (HFIX 2-1.5mm ²)	
		16C (HFIX 4-1.5mm ²)	
		22C (HFIX 8-1.5mm ²)	
		16C (HFIX 2-2.5mm ²)	
유도등용 배관 배선		16C (HFIX 2.5mm ² x 2 E-2.5mm ²)	
비상조명 배관 배선		16C (HFIX 2.5mm ² x 2 E-2.5mm ²)	

주 기 사 항	1. 각 소방 설비 배선중 표기없는 매입 전선관은 HI-PVC 전선관 또는
	난연용 CD전선관을 사용할것. (단, 노출부분은 아연도 강제후강전선관을 사용)
	배관용 금구는 용융 아연도금 제품을 사용하여야 한다.

(주)정연엔지니어링

전력전문1종설계업등록 [경기안양1-1호]
건축전기설비기술사 조 성 환
전 문 소 방 시 설 설 계 업 등 록
[제2017-01-00097호]
소방설비기술사 홍 기 만
정 보 통 신 등 록 [제 E-6-825호]
정보통신책임기술자 황 선 덕
기 계 설 비 등 록 [제 E-6-825호]
건축기계설비기술사 홍 기 만
경기도 안양시 동안구 흥안대로 415,
1115호,1116호 (평촌동,두산벤처다임)
대 표 전 화 : (031) 456 - 9666

PROJECT TITLE

LS Electric
R-Center 구축

PROJECT NUMBER

224001

DESIGN CONSULTANT

가운건축

GAUN I Architects & Engineers

[서울시 강남구 언주로 609, 10층 (논현동, 팍스타워)]
Tel:82-2-3443-7799 Fax:82-2-3443-3807
www.gaun.co.kr

NOTES

KEY PLAN

△

△

△

△

△

△

△

△

NO.

DESCRIPTION

DATE

ISSUES & REVISIONS

BUILDING NAME

R-Center

DRAWING TITLE

소방범례 및 주기사항

DRAWN

CHECK 1

CHECK 2

APPR

안 동 식

이 은 진

정 용 재

SCALE


DATE

A3:1/NONE

2024.01

DRAWING NO.

EF - 001

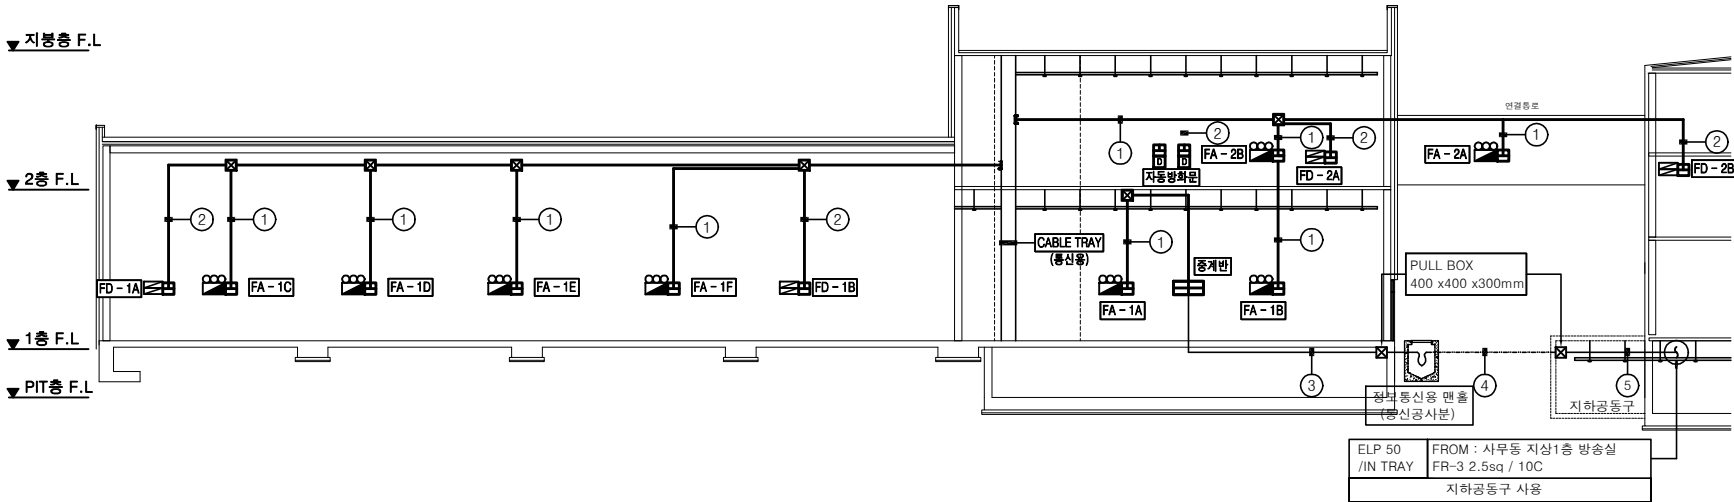

자동화재탐지설비의 수신기는 화재로 인하여 하나의 층의 지구음향장치의 배선이 단락되어도 다른 층의 화재통보에 지장이 없도록 해야한다.
ex) 경종단락보호장치를 설치하거나 경종, 경종공통선을 별개로 연결토록한다.

소방 간선설비 계통도

SCALE : 1/NONE(A3)
SCALE : 1/NONE(A1)

배관, 배선 규격표			
번호	배관 및 배선 규격	비고	비고
①	22C (TSP AWG #18 - 2PR) 28C (HFIX 8-2.5mm) 16C (HFIX 2-2.5mm)	중계기 신호 전송2 소화전 기동확인2, 공통, 위치표시등, 발신기음성, 경종, 표시음성, 회로, 방화전선	소화전, 발신기
②	22C (TSP AWG #18 - 2PR) 16C (HFIX 2-2.5mm)	중계기 신호 전송2 중계기전원2	방화셔터
③	F/O SM 8C x1(22C) FR-8 2.5mm/5Cx1(22C)	수신반연동	옥내
④	F/O SM 8C x1 FR-8 2.5mm/5Cx1 (ELP 30φ)	수신반연동	옥외
⑤	F/O SM 8C x1(IN TRAY) FR-8 2.5mm/5Cx1(IN TRAY)	수신반연동	기존동
▶ 전선은 소방기술기준에 적합한것을 사용한다. ▶ 전선본수는 제작사의 시스템에 따라 변동될수 있다. ▶ 모든 소방간선 케이블은 매입에서 TRAY로 구간 변경시 F-FR-8 CABLE을 사용토록 한다. (NFTC, NFTC 내화/내열배선 성능 충족할 것.)			

범례 및 주기사항		
심 별	내 용	비 고
☐	차동식 감지기(2종 스포트형)-LED 부착형	
□	정온식 감지기(1종 스포트형)-LED 부착형	
☒	연기식 감지기(1,2종 광전식)-LED 부착형	
☎	수동발신기 SET (소화전 상단형)	
☒	청각장애인을 위한 시각경보기	
☒	화재 주 수신반	
☒	전원반(중계기, 시각경보기, 불꽃감지기)	
☒	SUPER VISORY PANEL	
☒	모터 싸이렌	
☒	방화셔터 연동 제어반	
☒	배연창 연동 제어반	
1. 감지기 배관 배선 — F — : 16C (HFIX 2-1.5mm) — F — : 16C (HFIX 4-1.5mm) — F — : 22C (HFIX 8-1.5mm) 2. 시각경보기 배관 배선 — SR — : 16C (HFIX 2-2.5mm) 3. 싸이렌 배관 배선 — MG — : 16C (HFIX 2-2.5mm) : 노출 배관 공사시에는 STEEL 배관으로 시공 할수 있도록 한다.		

JUNG YEON (주)정연엔지니어링
전력전문1종설계업등록 [경기안양1-1호]
건축전기설비기술사 조 성 환
전 문 소 방 시 설 설 계 업 등 록
[제2017-01-00097호]
소방설비기술사 홍 기 만
정 보 통 신 등 록 [제 E-6-825호]
정보통신책임기술자 황 선 덕
기 계 설 비 등 록 [제 E-6-825호]
건축기계설비기술사 홍 기 만
경기도 안양시 동안구 흥안대로 415,
1115호 (평촌동, 두산벤처다임)
대 표 전 화 : (031) 456 - 9666

PROJECT TITLE

LS Electric
R-Center 구축

PROJECT NUMBER

224001

DESIGN CONSULTANT

가운 건축
GAUN I Architects & Engineers
서울시 강남구 영주로 609, 10층 (논현동, 파크타워)
Tel:82-2-3443-7799 Fax:82-2-3443-3807
www.gaun.co.kr

NOTES

KEY PLAN

NO.

DESCRIPTION

DATE

ISSUES & REVISIONS

BUILDING NAME

R-Center

DRAWING TITLE

소방 간선설비 계통도

DRAWN

CHECK 1

CHECK 2

APPR


DRAWING NO.

SCALE

DATE

2024.01

EF - 003

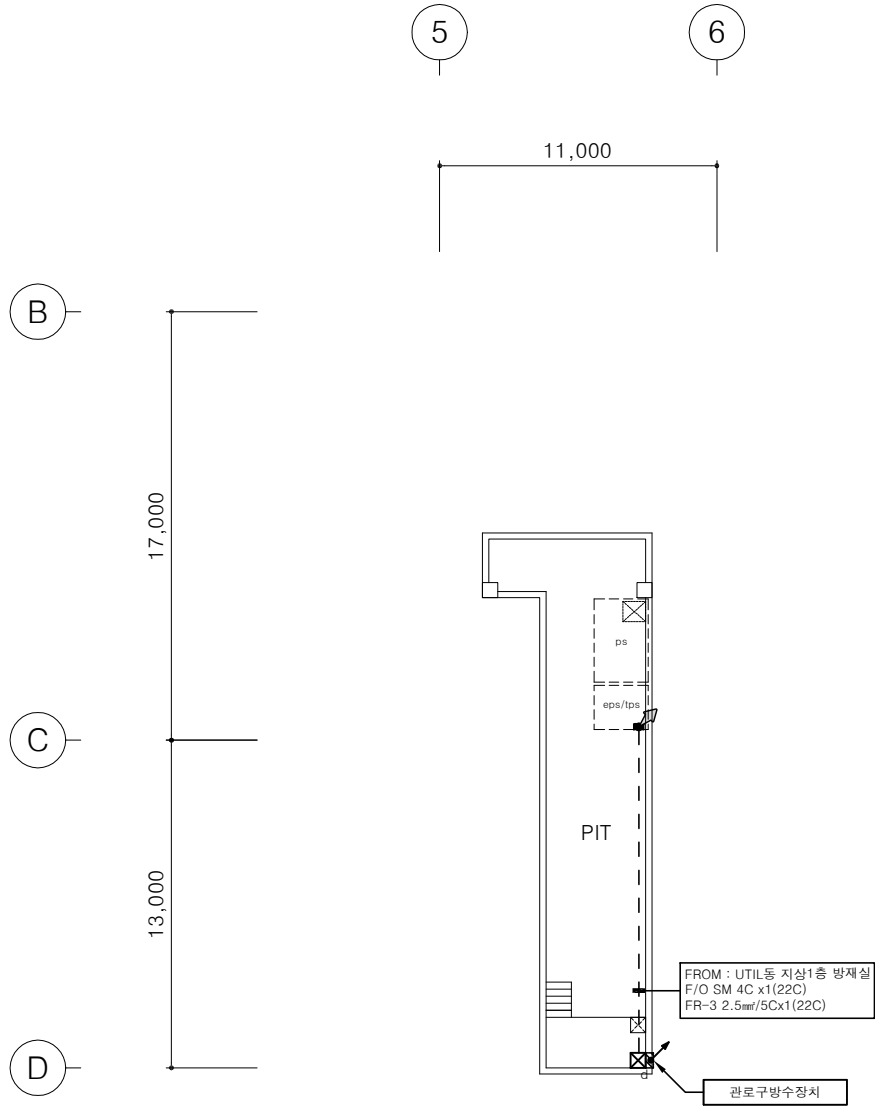

PIT 소방간선설비 평면도
SCALE : 1/300(A3)
SCALE : 1/150(A1)

- NOTE
1. 배관 배선
— : 슬라브 매입 배관 배선
— : 노출 배관 배선
— : 바닥 은폐 및 지중 매설 배관 배선
— : CABLE TRAY내 배선
2. 방송용 배관, 배선
—S— : 16C (HFIX 2~1.5sq)
—S— : 16C (HFIX 3~1.5sq)
—S— : 16C (HFIX 4~1.5sq)
3. LEGEND
— : SPEAKER 단자함
— : 스피커 천정형 (3W)
(SPEAKER-CEILING TYPE)
— : 컬럼형 SPEAKER (3W)
(SPEAKER-WALL BRACKET TYPE)
— : 컬럼형 SPEAKER (10W)
(SPEAKER-WALL BRACKET TYPE)
— : PULL BOX SIZE 150 x 150 x 100mm
— : PULL BOX SIZE 200 x 200 x 150mm
— : PULL BOX SIZE 300 x 300 x 200mm
— : PULL BOX SIZE 400 x 400 x 300mm
4. 간선 규격 및 기타 사항은 계통도 참조.

PROJECT TITLE

LS Electric
R-Center 구축

PROJECT NUMBER

224001

DESIGN CONSULTANT

가운건축
GAUN I Architects & Engineers
서울시 강남구 언주로 609, 10층 (논현동, 팍스타워)
Tel:82-2-3443-7799 Fax:82-2-3443-3807
www.gaun.co.kr

NOTES

KEY PLAN

△		
△		
△		
△		
△		
△		
△		
△		
NO.	DESCRIPTION	DATE

ISSUES & REVISIONS

BUILDING NAME

DRAWING TITLE

PIT 소방간선설비 평면도


DRAWN	SCALE
CHECK 1 안동식	A3:1/300
CHECK 2 이은진	DATE
APPR 정용재	2024.01

DRAWING NO.


EF - 101

(주)정연엔지니어링

전력전문1종설계업등록 [경기안양1-1호]
건축전기설비기술사 조 성 환
전 문 소 방 시 설 설 계 업 등 록
[제2017-01-00097호]
소방설비기술사 홍 기 만
정 보 통 신 등 록 [제 E-6-825호]
정보통신책임기술자 황 선 덕
기 계 설 비 등 록 [제 E-6-825호]
건축기계설비기술사 홍 기 만
경기도 안양시 동안구 흥안대로 415,
1115호,1116호 (평촌동,두산벤처다임)
대 표 전 화 : (031) 456 - 9666

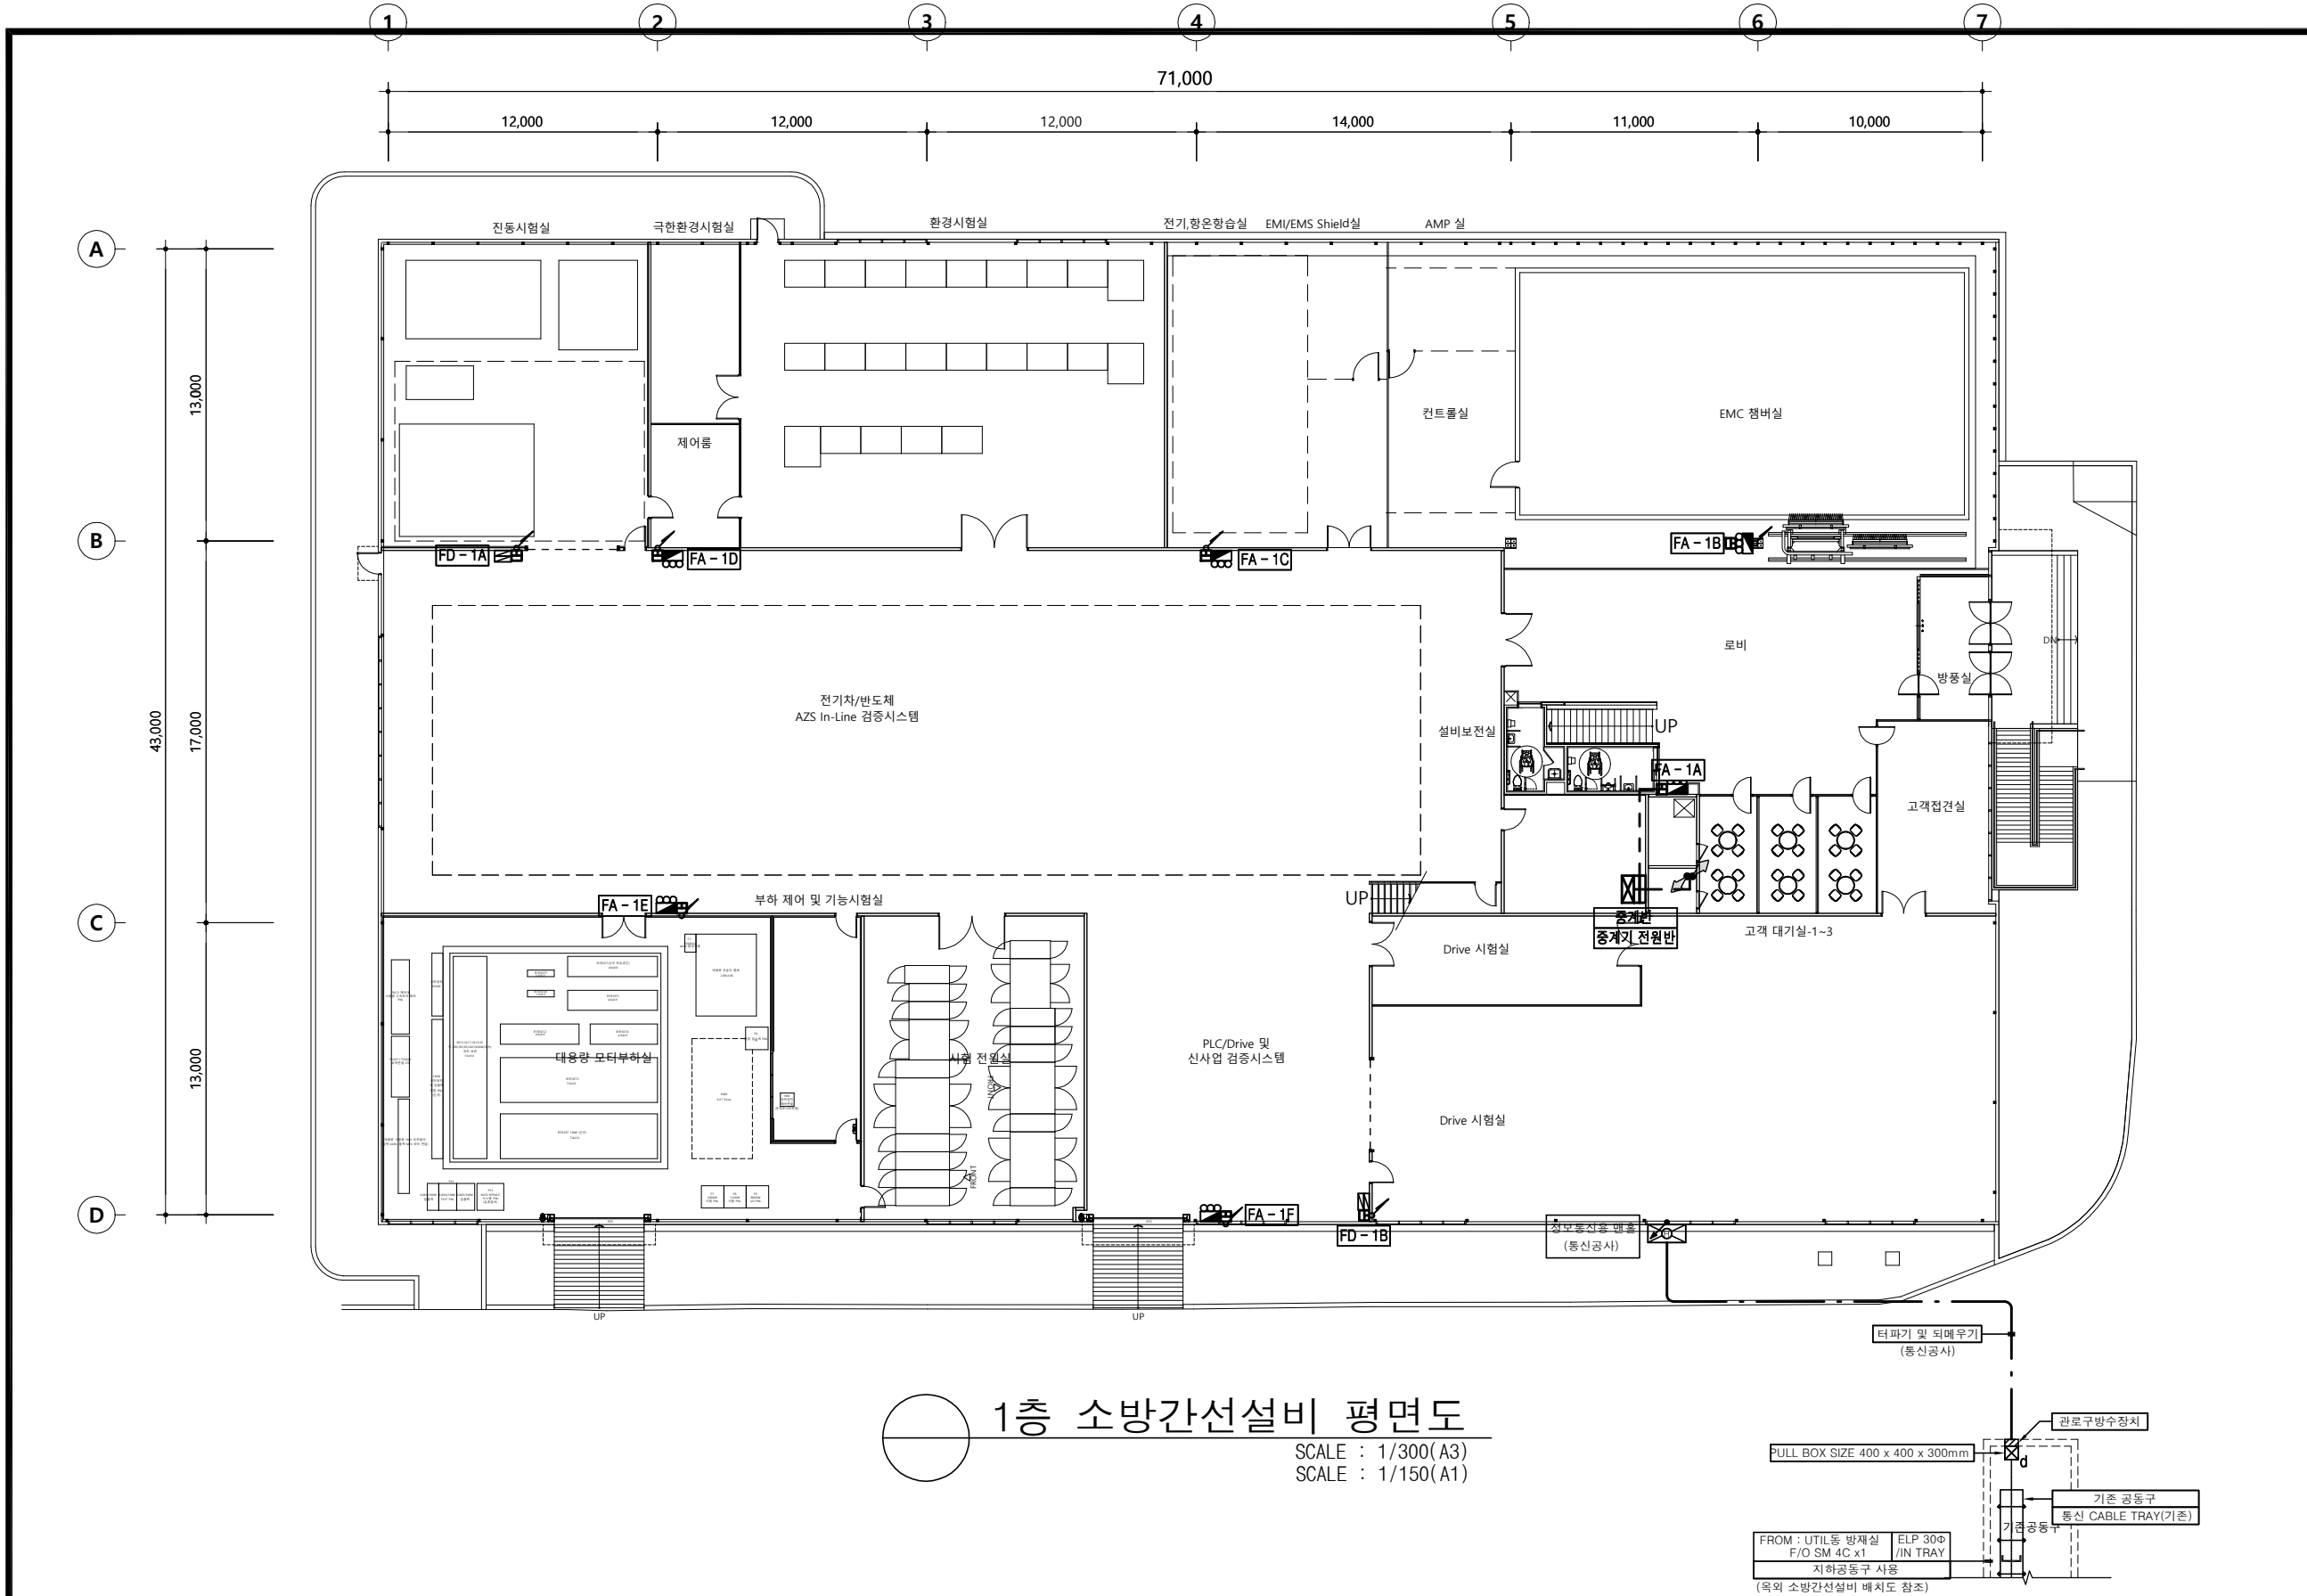

1층 소방간선설비 평면도
SCALE : 1/300(A3)
SCALE : 1/150(A1)

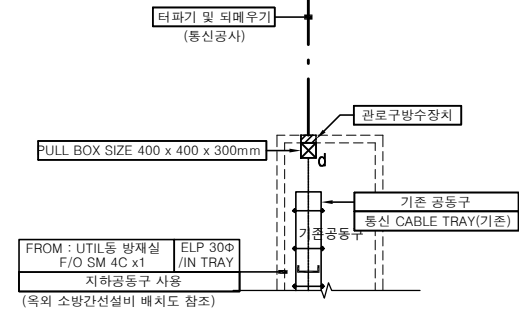

(주)정연엔지니어링
전력전문1종설계업등록 [경기안양1-1호]
건축전기설비기술사 조 성 환
전 문 소 방 시 설 설 계 업 등 록
[제2017-01-00097호]
소방설비기술사 홍 기 만
정 보 통 신 등 록 [제 E-6-825호]
정보통신책임기술자 황 선 덕
기 계 설 비 등 록 [제 E-6-825호]
건축기계설비기술사 홍 기 만
경기도 안양시 동안구 흥안대로 415,
1115호 (평촌동,두산벤처다임)
대 표 전 화 : (031) 456 - 9666

PROJECT TITLE

LS Electric
R-Center 구축

PROJECT NUMBER

224001

DESIGN CONSULTANT

가운 건축

GAUN | Architects & Engineers

서울시 강남구 언주로 609, 10층 (논현동, 팍스타워)
Tel:82-2-3443-7799 Fax:82-2-3443-3807
www.gaun.co.kr

NOTES

KEY PLAN

△		
△		
△		
△		
△		
△		
△		
△		
NO.	DESCRIPTION	DATE

ISSUES & REVISIONS

BUILDING NAME

R-Center


DRAWING TITLE

1층 소방간선설비 평면도

DRAWN	SCALE
CHECK 1 안 동 식	A3:1/300
CHECK 2 이 은 진	DATE
APPR 정 용 재	2024.01

DRAWING NO.

EF - 102

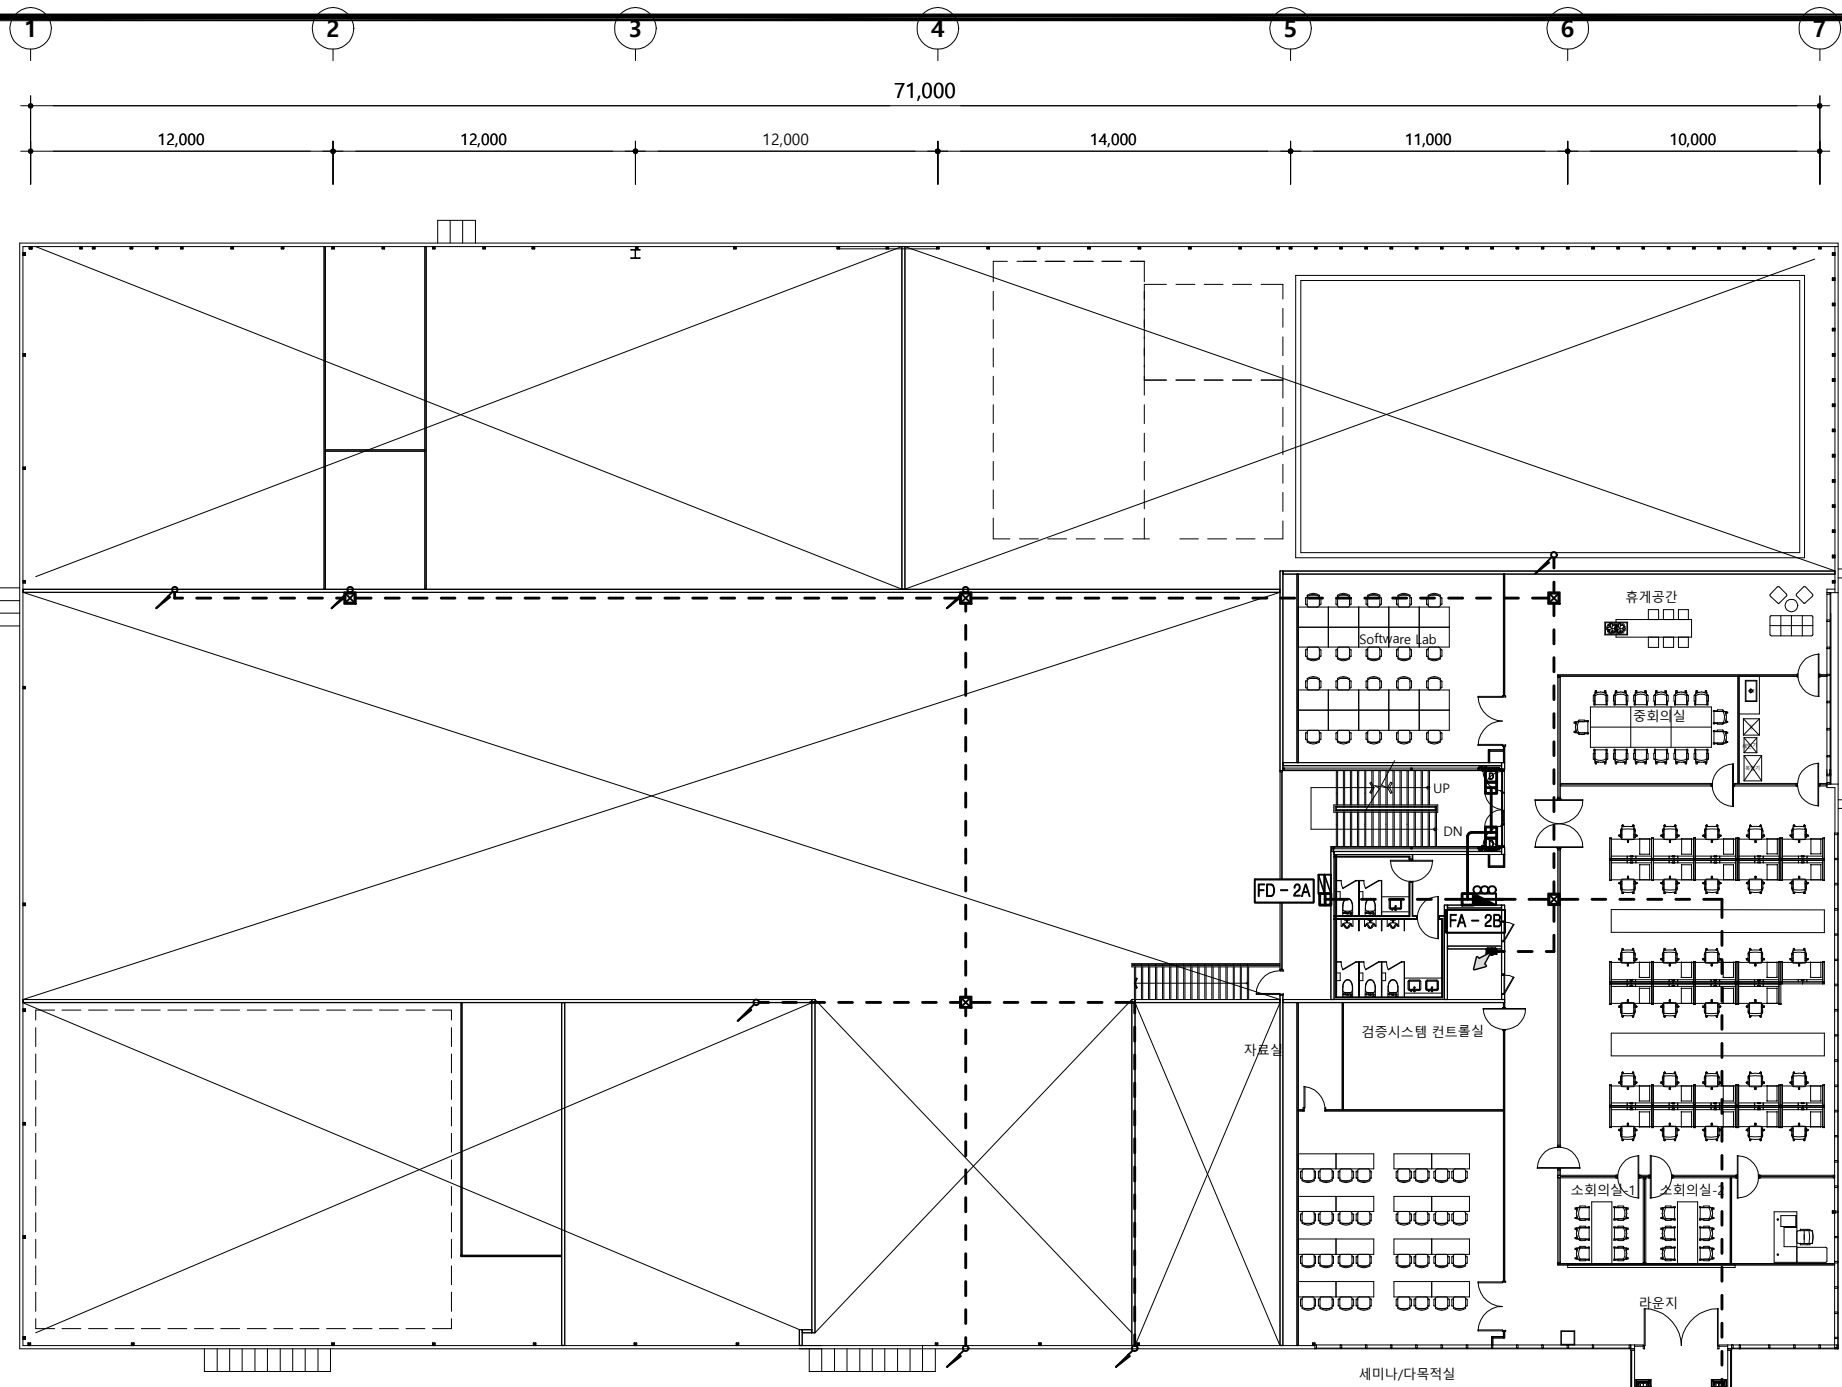

2층 소방간선설비 평면도
SCALE : 1/300(A3)
SCALE : 1/150(A1)

(주)정연엔지니어링
전력전문1종설계업등록 [경기안양1-1호]
건축전기설비기술사 조 성 환
전 문 소 방 시 설 설 계 업 등 록
[제2017-01-00097호]
소방설비기술사 홍 기 만
정 보 통 신 등 록 [제 E-6-825호]
정보통신책임기술자 황 선 덕
기 계 설 비 등 록 [제 E-6-825호]
건축기계설비기술사 홍 기 만
경기도 안양시 동안구 흥안대로 415,
1115호, 1116호 (평촌동, 두산벤처다임)
대 표 전 화 : (031) 456 - 9666

PROJECT TITLE

LS Electric

R-Center 구축

PROJECT NUMBER

224001

DESIGN CONSULTANT

가운 건축

GAUN | Architects & Engineers

서울시 강남구 언주로 609, 10층 (논현동, 팍스타워)
Tel:82-2-3443-7799 Fax:82-2-3443-3807
www.gaun.co.kr

NOTES

KEY PLAN

△

△

△

△

△

△

△

△

△

NO.

DESCRIPTION

DATE

ISSUES & REVISIONS

BUILDING NAME

R-Center

DRAWING TITLE

2층 소방간선설비 평면도

DRAWN

CHECK 1 안 동 식

CHECK 2 이 은 진

APPR 정 용 재

SCALE

A3:1/300

DATE

2024.01

DRAWING NO.

EF - 103

△		
△		
△		
△		
△		
△		
△		
△		




NO.	DESCRIPTION	DATE
-----	-------------	------

ISSUES & REVISIONS		
--------------------	--	--

BUILDING NAME
R-Center

DRAWING TITLE
1층 자동화재탐지설비 평면도

DRAWN	SCALE
CHECK 1 안동식	A3:1/300
CHECK 2	DATE
이은진	2024.01
APPR	
정용재	
DRAWING NO.	
EF - 201	

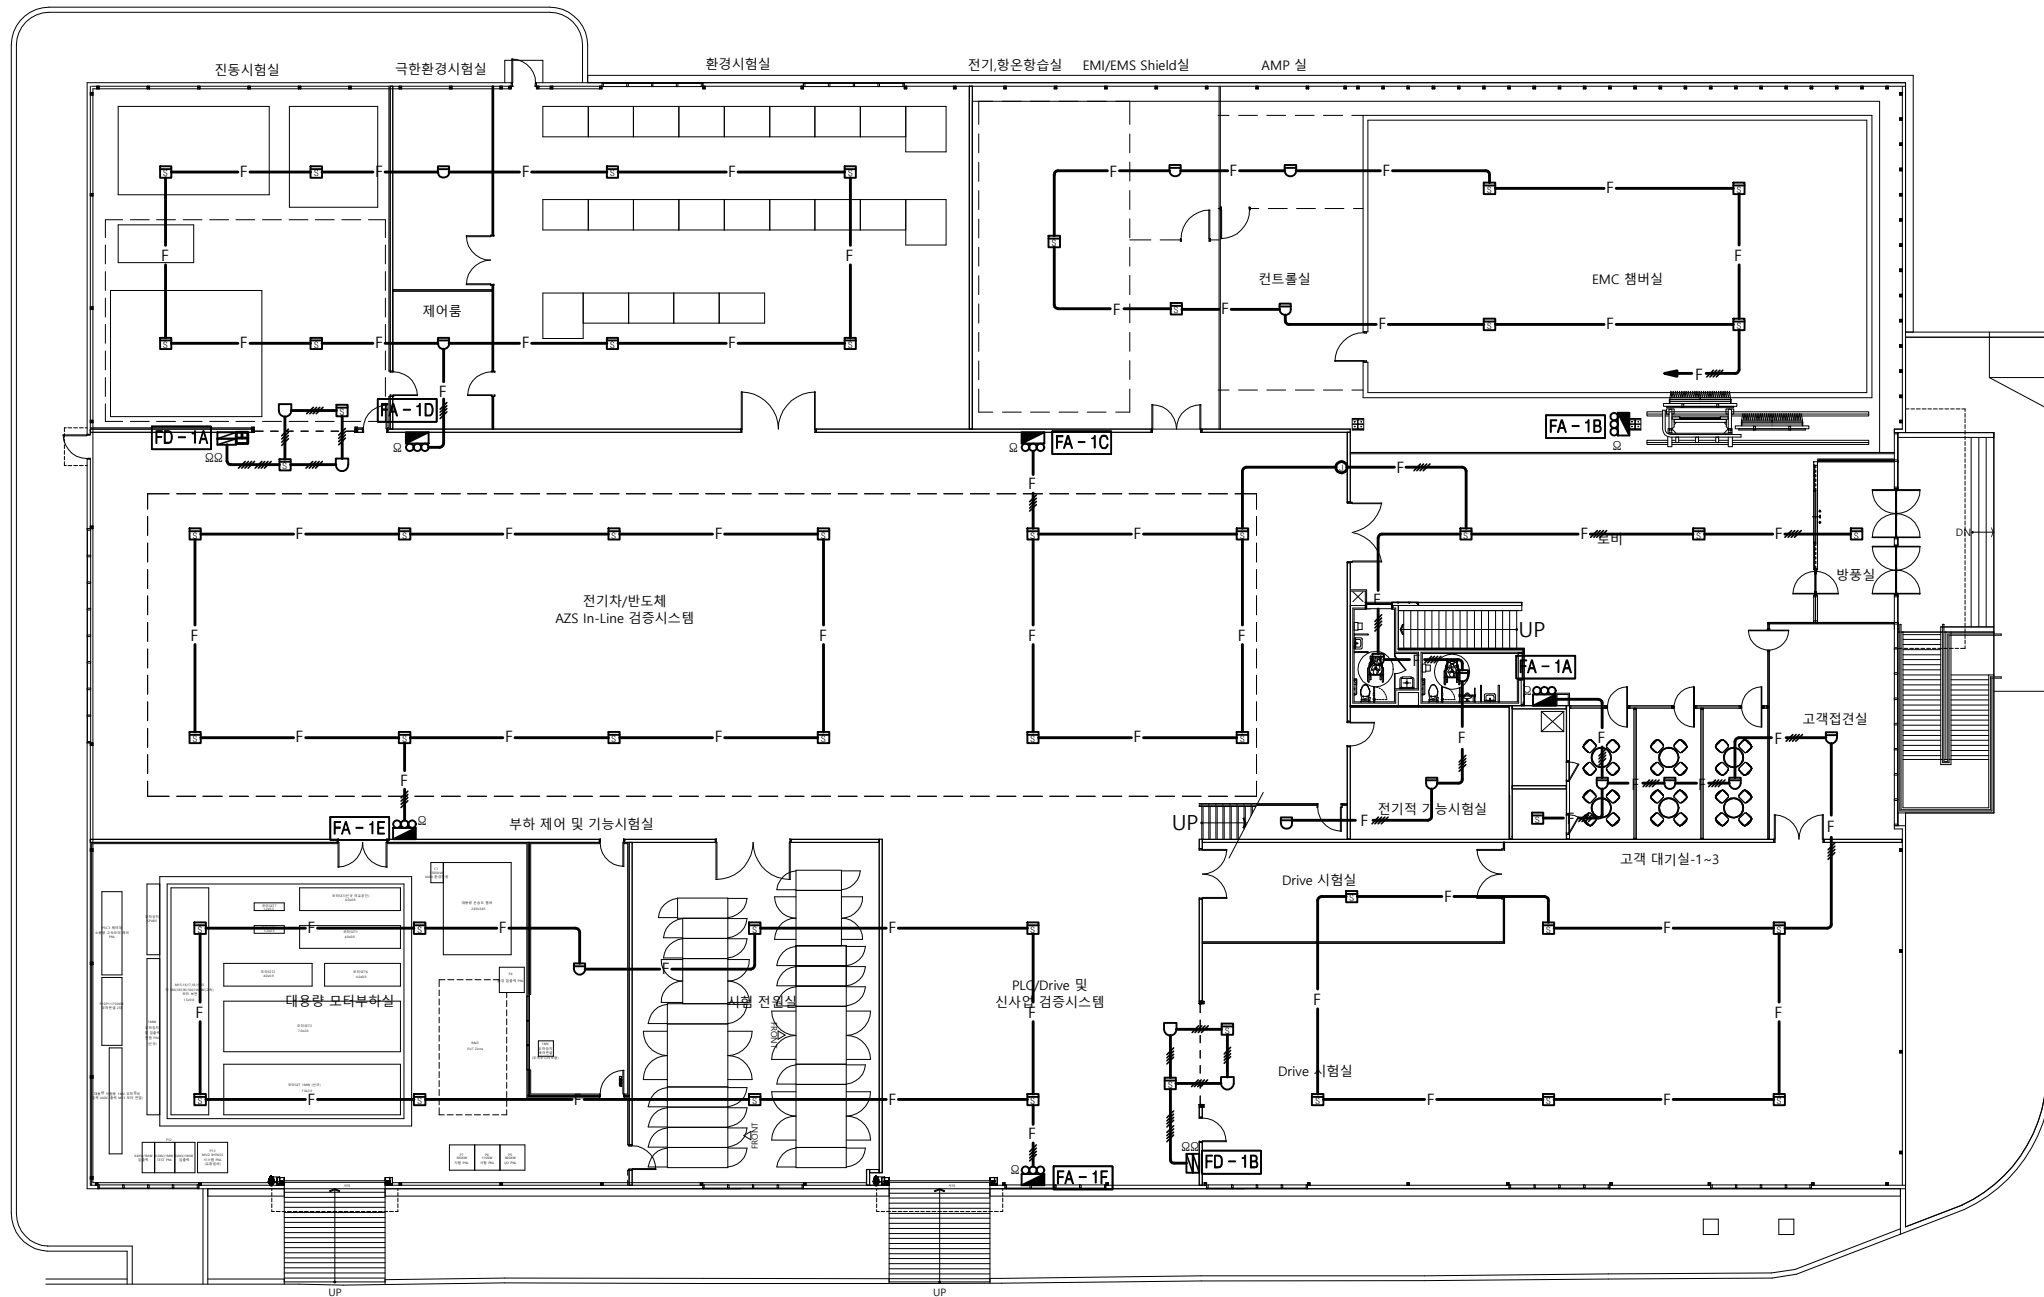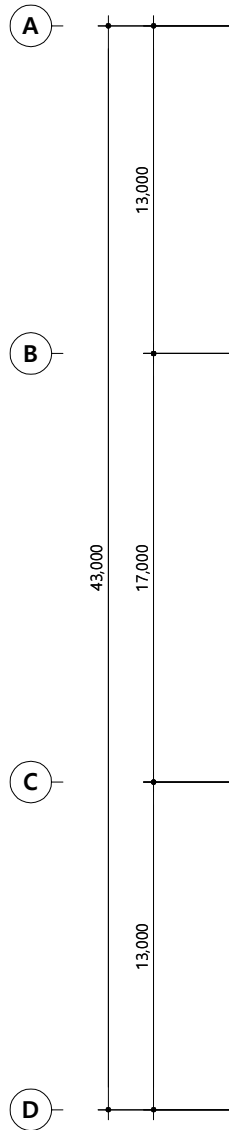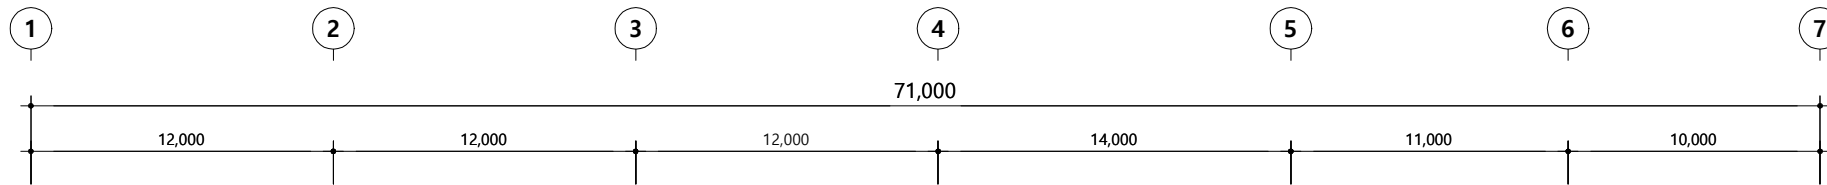




범례 및 주기사항		
심 별	내 용	수 량
☐	자동식 감지기(2종 스포트형)-LED 부착형	14EA
○	정온식 감지기(1종 스포트형)-LED 부착형	4EA
■	연기식 감지기(1,2종 광전식)-LED 부착형	48EA
■	수동발신기 SET (소화전 상단형)	6EA
■	화재 수신반	
■	전원반(중계기)	
■	방화셔터 연동 제어반	

1. 감지기 배관 배선	
— F —	: 16C (HFIX 2-1.5mm ²)
— F —	: 16C (HFIX 4-1.5mm ²)
: 노출 배관 공사시에는 STEEL 배관으로 시공 할수 있도록 한다.	

1층 자동화재탐지설비 평면도

SCALE : 1/NONE(A3)
SCALE : 1/NONE(A1)

정연엔지니어링
(주)정연엔지니어링
전력전문1종설계업등록 [경기안양1-호]
건축전기설비기술사 조 성 환
전문 소방 시설 설계 업 등록
[제2017-01-00097호]
소방설비기술사 홍 기 만
정보통신 등록 [제 E-6-825호]
정보통신책임기술자 황 선 덕
기계 설 비 등록 [제 E-6-825호]
건축기계설비기술사 홍 기 만
경기도 안양시 동안구 흥안대로 415,
1115호, 1116호 (평촌동, 두산벤처다임)
대 표 전 화 : (031) 456 - 9666

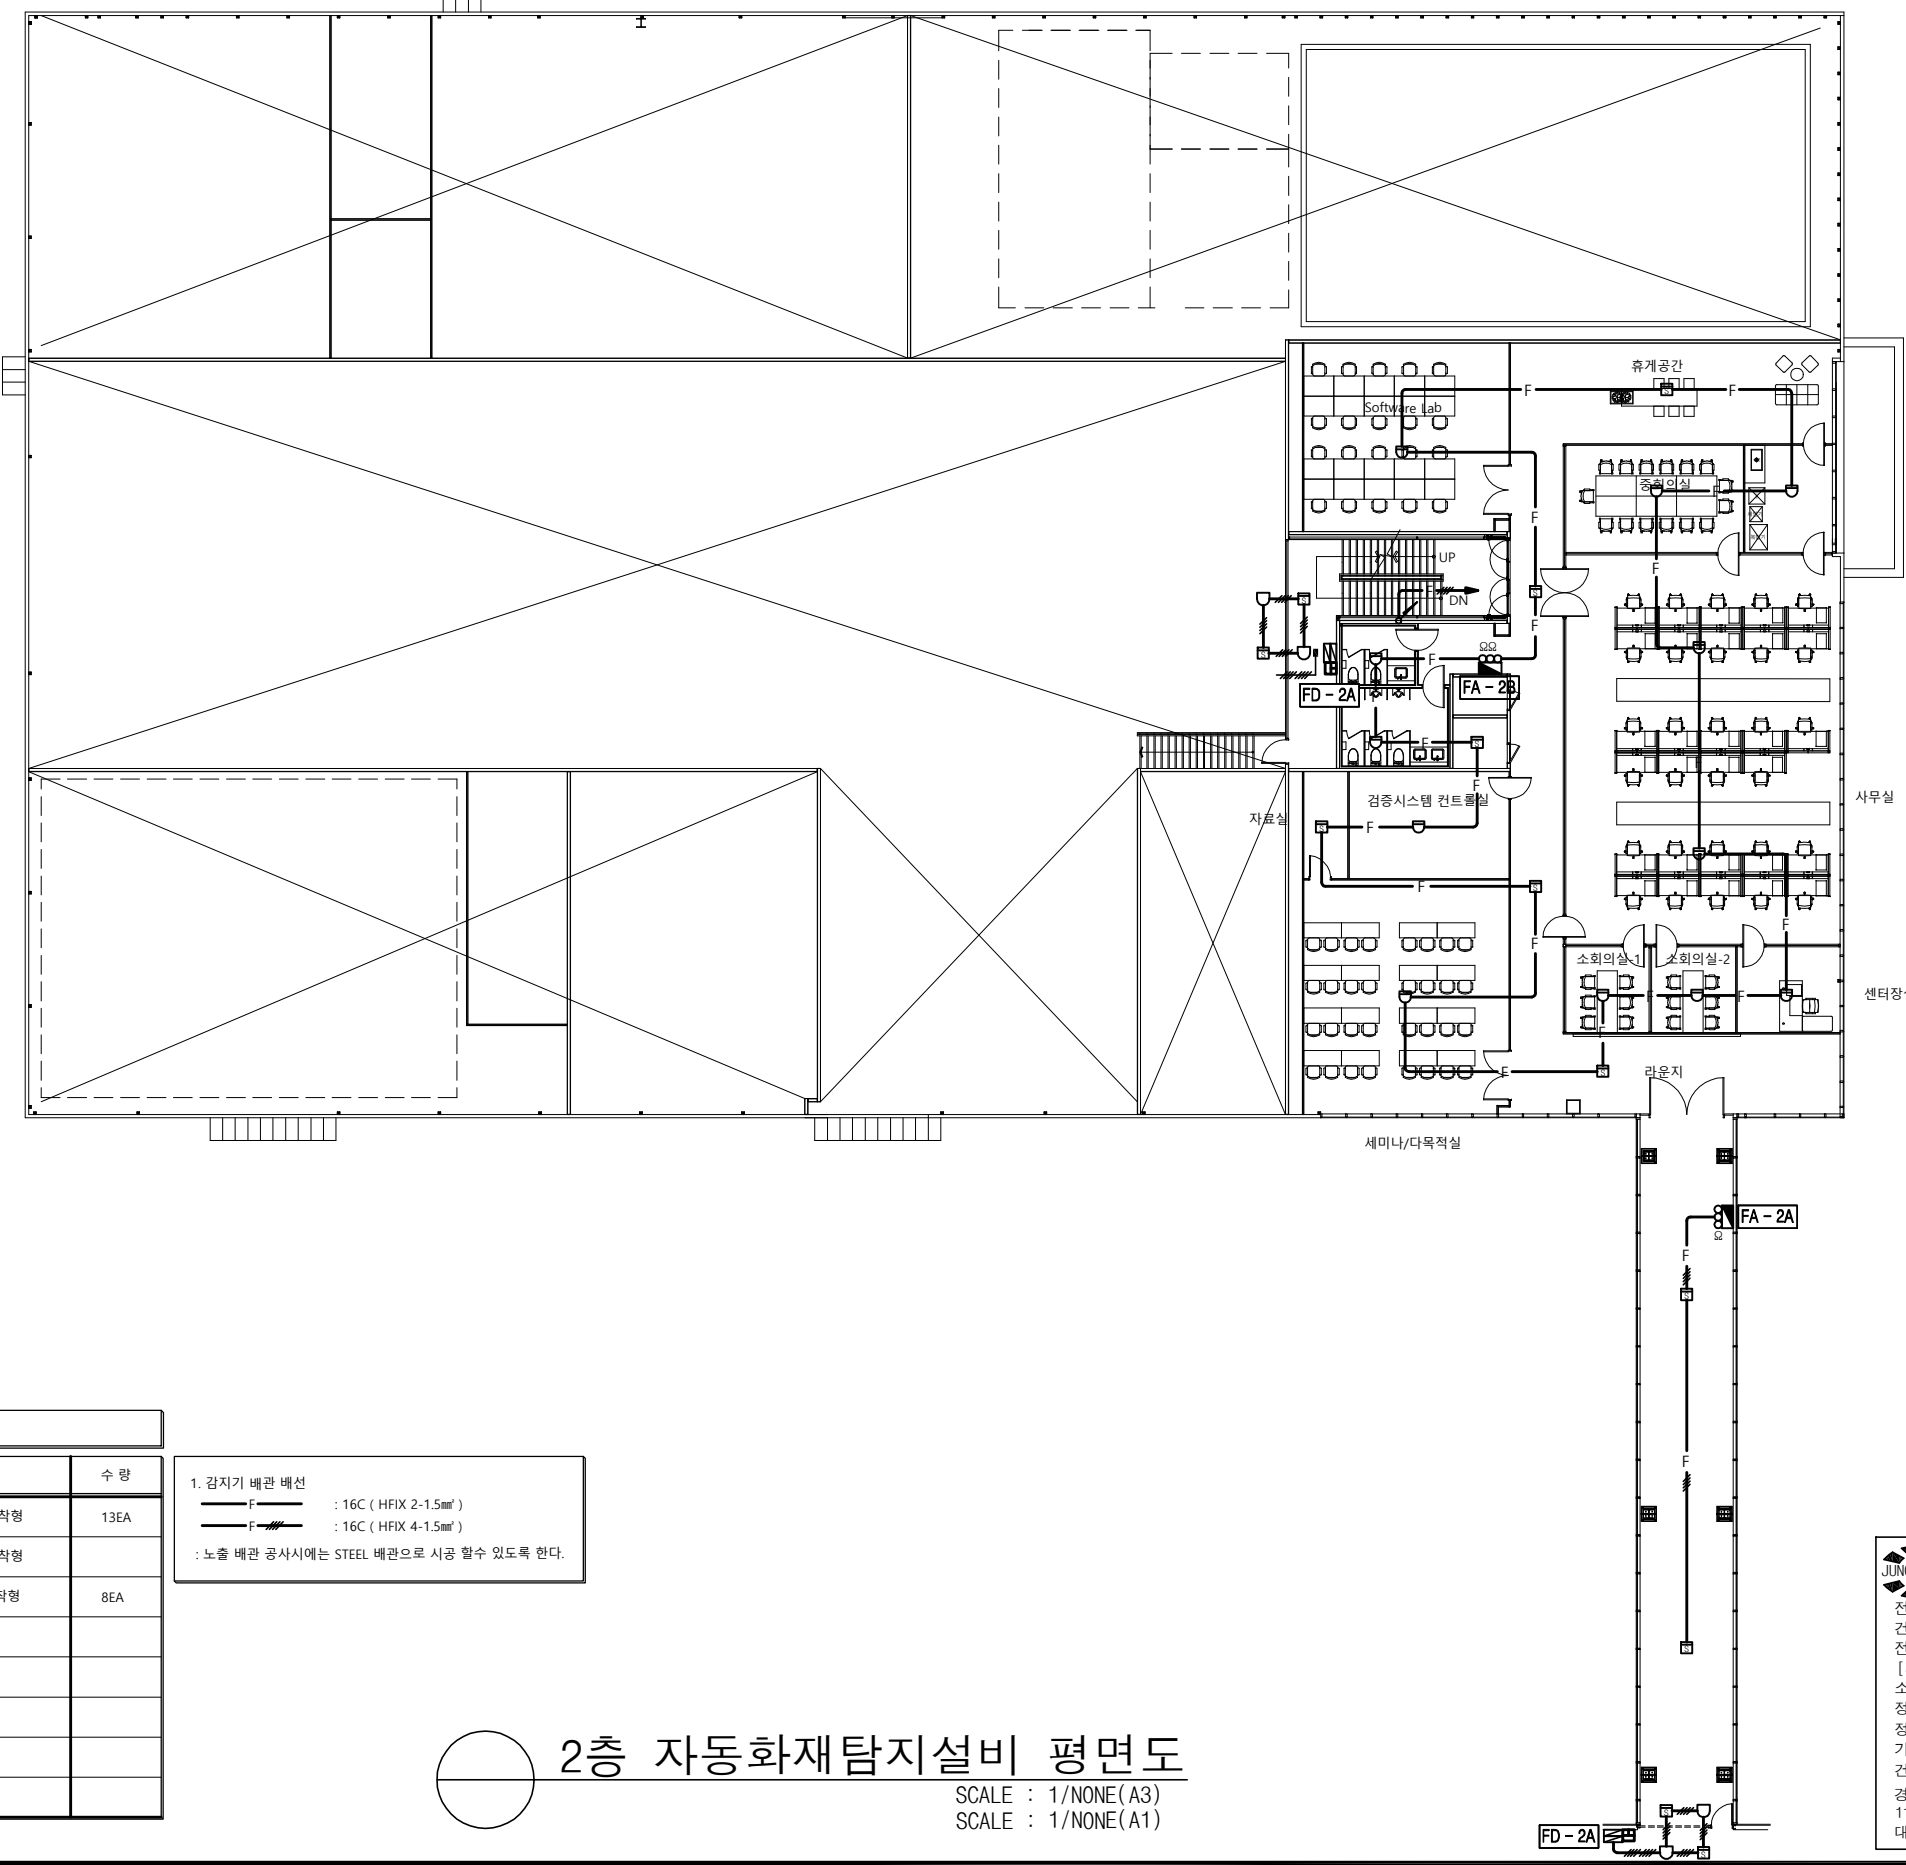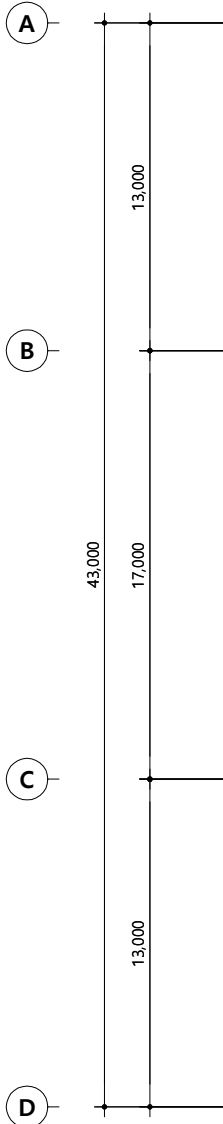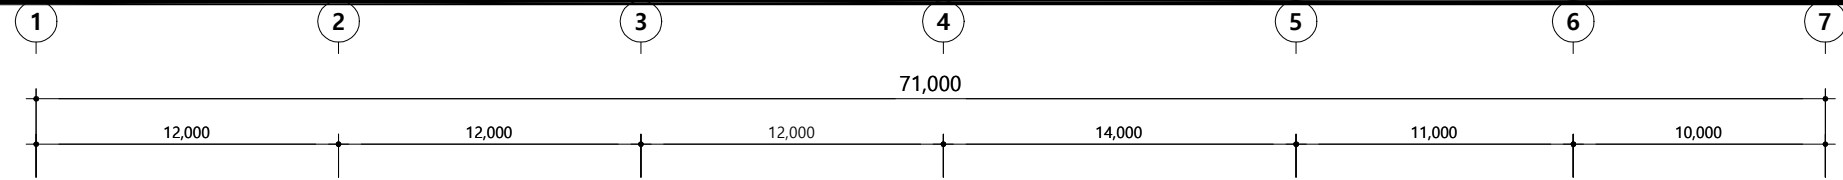

범례 및 주기사항		
심 별	내 용	수 량
☐	자동식 감지기(2종 스포트형)-LED 부착형	13EA
○	정온식 감지기(1종 스포트형)-LED 부착형	
■	연기식 감지기(1,2종 광전식)-LED 부착형	8EA
☐	수동발신기 SET (소화전 상단형)	
☒	화재 수신반	
☐	전원반(중계기)	
☐	방화셔더 연동 제어반	

1. 감지기 배관 배선
— F — : 16C (HFIX 2-1.5mm²)
— F — : 16C (HFIX 4-1.5mm²)
: 노출 배관 공사시에는 STEEL 배관으로 시공 할수 있도록 한다.

2층 자동화재탐지설비 평면도
SCALE : 1/NONE(A3)
SCALE : 1/NONE(A1)

(주)정연엔지니어링

전력전문1종설계업등록 [경기안양1-호]
건축전기설비기술사 조 성 환
전문 소방 시설 설계업 등록
[제2017-01-00097호]
소방설비기술사 홍 기 만
정보통신 등록 [제 E-6-825호]
정보통신책임기술자 황 선 덕
기계 설비 등록 [제 E-6-825호]
건축기계설비기술사 홍 기 만
경기도 안양시 동안구 흥안대로 415,
1115호, 1116호 (평촌동, 두산벤처대입)
대 표 전 화 : (031) 456 - 9666

LS Electric
R-Center 구축

PROJECT NUMBER
224001

DESIGN CONSULTANT
가운 건축
GAUN | Architects & Engineers
[서울시 강남구 언주로 609, 10층 (논현동, 팍스타워)]
Tel:82-2-3443-7799 Fax:82-2-3443-3807
www.gaun.co.kr

NOTES

KEY PLAN

△		
△		
△		
△		
△		
△		
△		
△		
NO.	DESCRIPTION	DATE




ISSUES & REVISIONS

BUILDING NAME
R-Center

DRAWING TITLE
2층 자동화재탐지설비 평면도

DRAWN	SCALE
CHECK 1 안 동 식	A3:1/300
CHECK 2 이 은 진	DATE
APPR 정 용 재	2024.01

DRAWING NO.
EF - 202

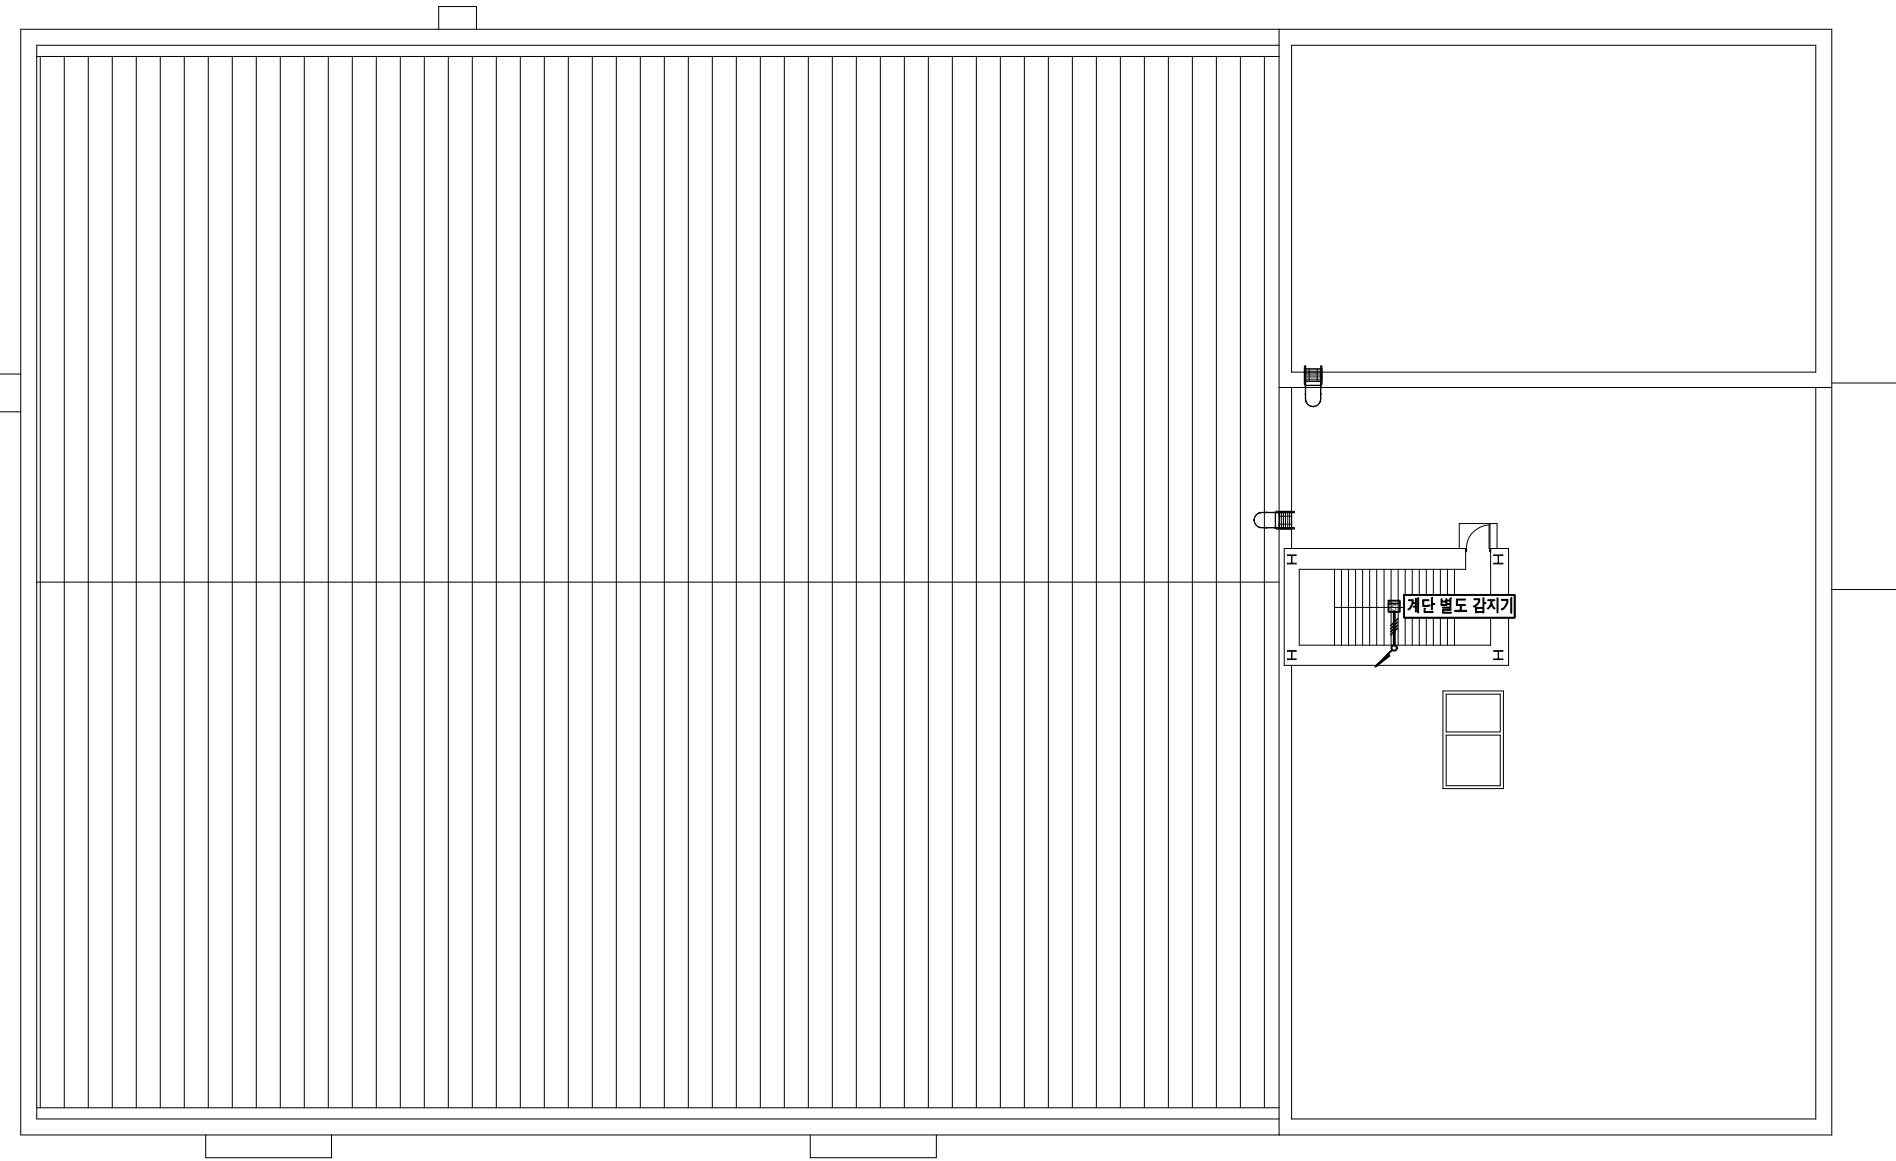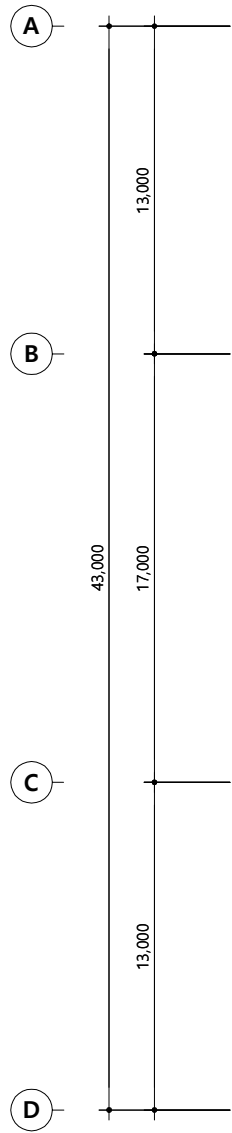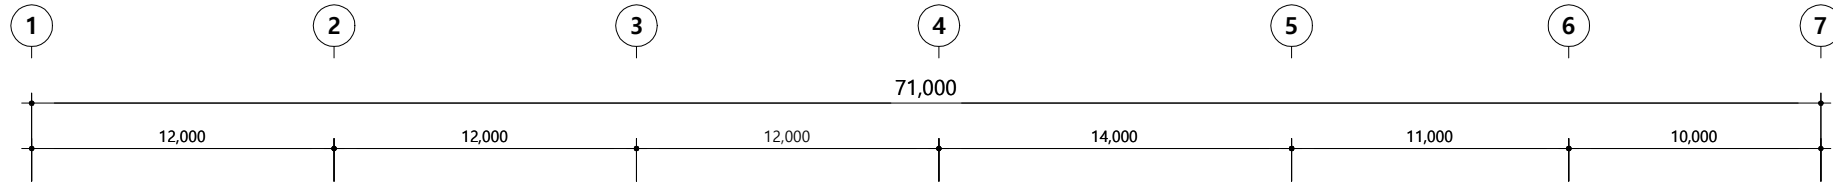

범례 및 주기사항		
심 별	내 용	수 량
☐	자동식 감지기(2종 스포트형)-LED 부착형	
○	정온식 감지기(1종 스포트형)-LED 부착형	
■	연기식 감지기(1,2종 광전식)-LED 부착형	1EA
■	수동발신기 SET (소화전 상단형)	
■	화재 수신반	
田	전원반(중계기)	
■	방화셔터 연동 제어반	

1. 감지기 배관 배선
— F — : 16C (HFIX 2-1.5mm²)
— F — : 16C (HFIX 4-1.5mm²)
: 노출 배관 공사시에는 STEEL 배관으로 시공 할수 있도록 한다.

○ 옥탑층 자동화재탐지설비 평면도
SCALE : 1/NONE(A3)
SCALE : 1/NONE(A1)

JUNG YEON

(주)정연엔지니어링

전력전문1종설계업등록 [경기안양1-1호]
건축전기설비기술사 조 성 환
전 문 소 방 시 설 설 계 업 등 록
[제2017-01-00097호]
소방설비기술사 홍 기 만
정 보 통 신 등 록 [제 E-6-825호]
정보통신책임기술자 황 선 덕
기 계 설 비 등 록 [제 E-6-825호]
건축기계설비기술사 홍 기 만
경기도 안양시 동안구 흥안대로 415,
1115호 ,1116호 (평촌동,두산벤처다임)
대 표 전 화 : (031) 456 - 9666

PROJECT TITLE

LS

LS Electric

R-Center 구축

PROJECT NUMBER

224001

DESIGN CONSULTANT

가운 건축

GAUN | Architects & Engineers

서울시 강남구 언주로 609, 10층 (논현동, 팍스타워)
Tel:82-2-3443-7799 Fax:82-2-3443-3807
www.gaun.co.kr

NOTES

KEY PLAN

△		
△		
△		
△		
△		
△		
△		
△		

NO.	DESCRIPTION	DATE
ISSUES & REVISIONS		

BUILDING NAME		
R-Center		




DRAWING TITLE

옥탑층
자동화재탐지설비 평면도

DRAWN	SCALE
CHECK 1 안 동 식	A3:1/300
CHECK 2 이 은 진	DATE
APPR 정 용 재	2024.01

DRAWING NO.

EF - 203

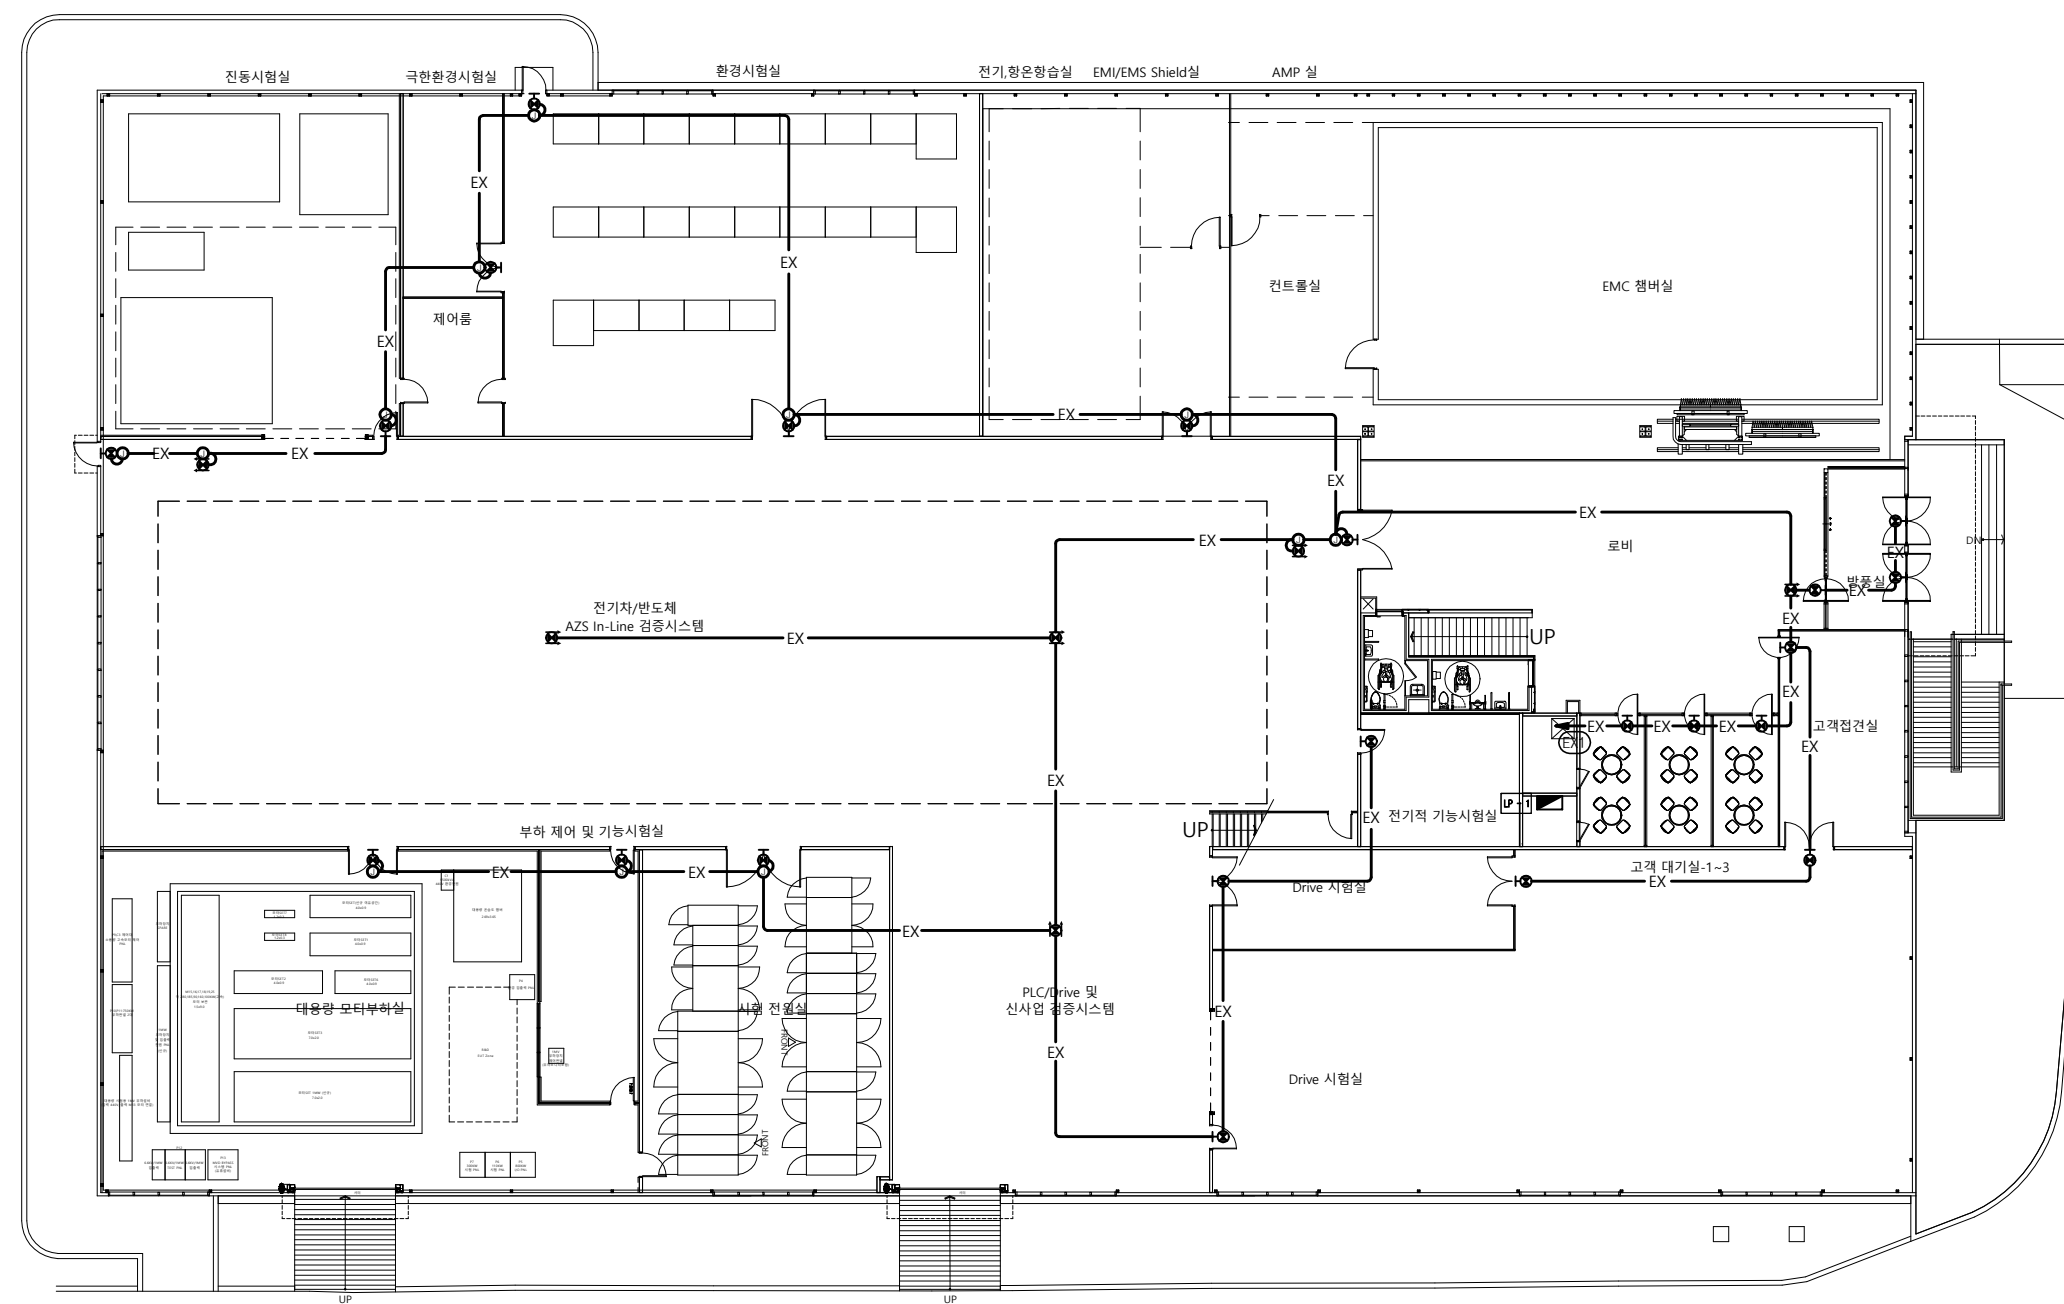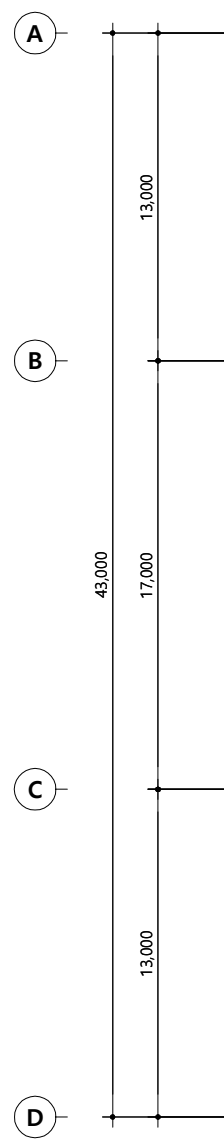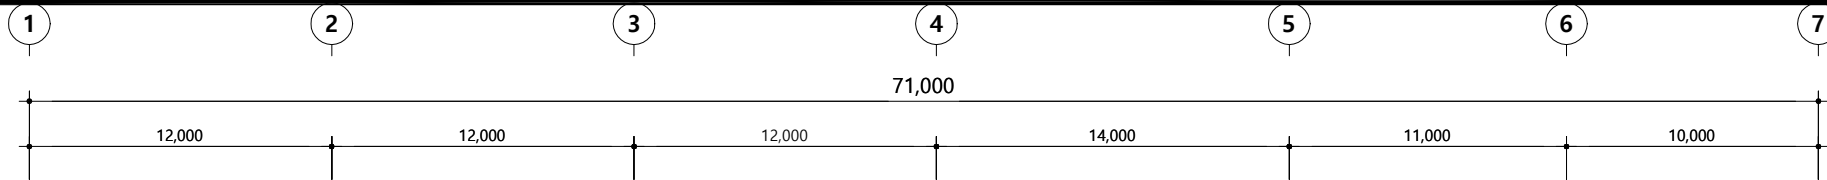

유도등 범례 및 주기사항		
심 별	명칭 및 규격	수 량
●	피난구 유도등 (전체 소형)	22EA
■	피난구 유도등 (전체 소형) 펜던트	3EA
□	계단 유도등-60분용(LED)	
□	복도 유도등-60분용(LED)	
□	거실 유도등-60분용(LED)	
—EX—	HF1X 2.5mm ² x 2 E-2.5mm ² (16C)	유도등 배선

1층 유도등설비 평면도
SCALE : 1/300(A3)
SCALE : 1/150(A1)

PROJECT TITLE

LS Electric
R-Center 구축

PROJECT NUMBER

224001

DESIGN CONSULTANT

가운 건축
GAUN | Architects & Engineers
[서울시 강남구 언주로 609, 10층 (논현동, 팍스타워)]
Tel:82-2-3443-7799 Fax:82-2-3443-3807
www.gaun.co.kr

NOTES

KEY PLAN

△		
△		
△		
△		
△		
△		
△		
△		
△		
NO.	DESCRIPTION	DATE

ISSUES & REVISIONS

BUILDING NAME

R-Center


DRAWING TITLE

1층 유도등설비 평면도

DRAWN	SCALE
CHECK 1 안동식	
CHECK 2 이은진	DATE
APPR 정용재	2024.01
DRAWING NO.	

EF - 301

(주)정연엔지니어링
전력전문1종설계업등록 [경기안양1-1호]
건축전기설비기술자 조 성 환
전문 소방 시설 설계업 등록
[제2017-01-00097호]
소방설비기술사 홍 기 만
정보통신 등록 [제 E-6-825호]
정보통신책임기술자 황 선 덕
기계설비 등록 [제 E-6-825호]
건축기계설비기술사 홍 기 만
경기도 안양시 동안구 흥안대로 415,
1115호 (평촌동, 두산벤처대입)
대표전화 : (031) 456 - 9666

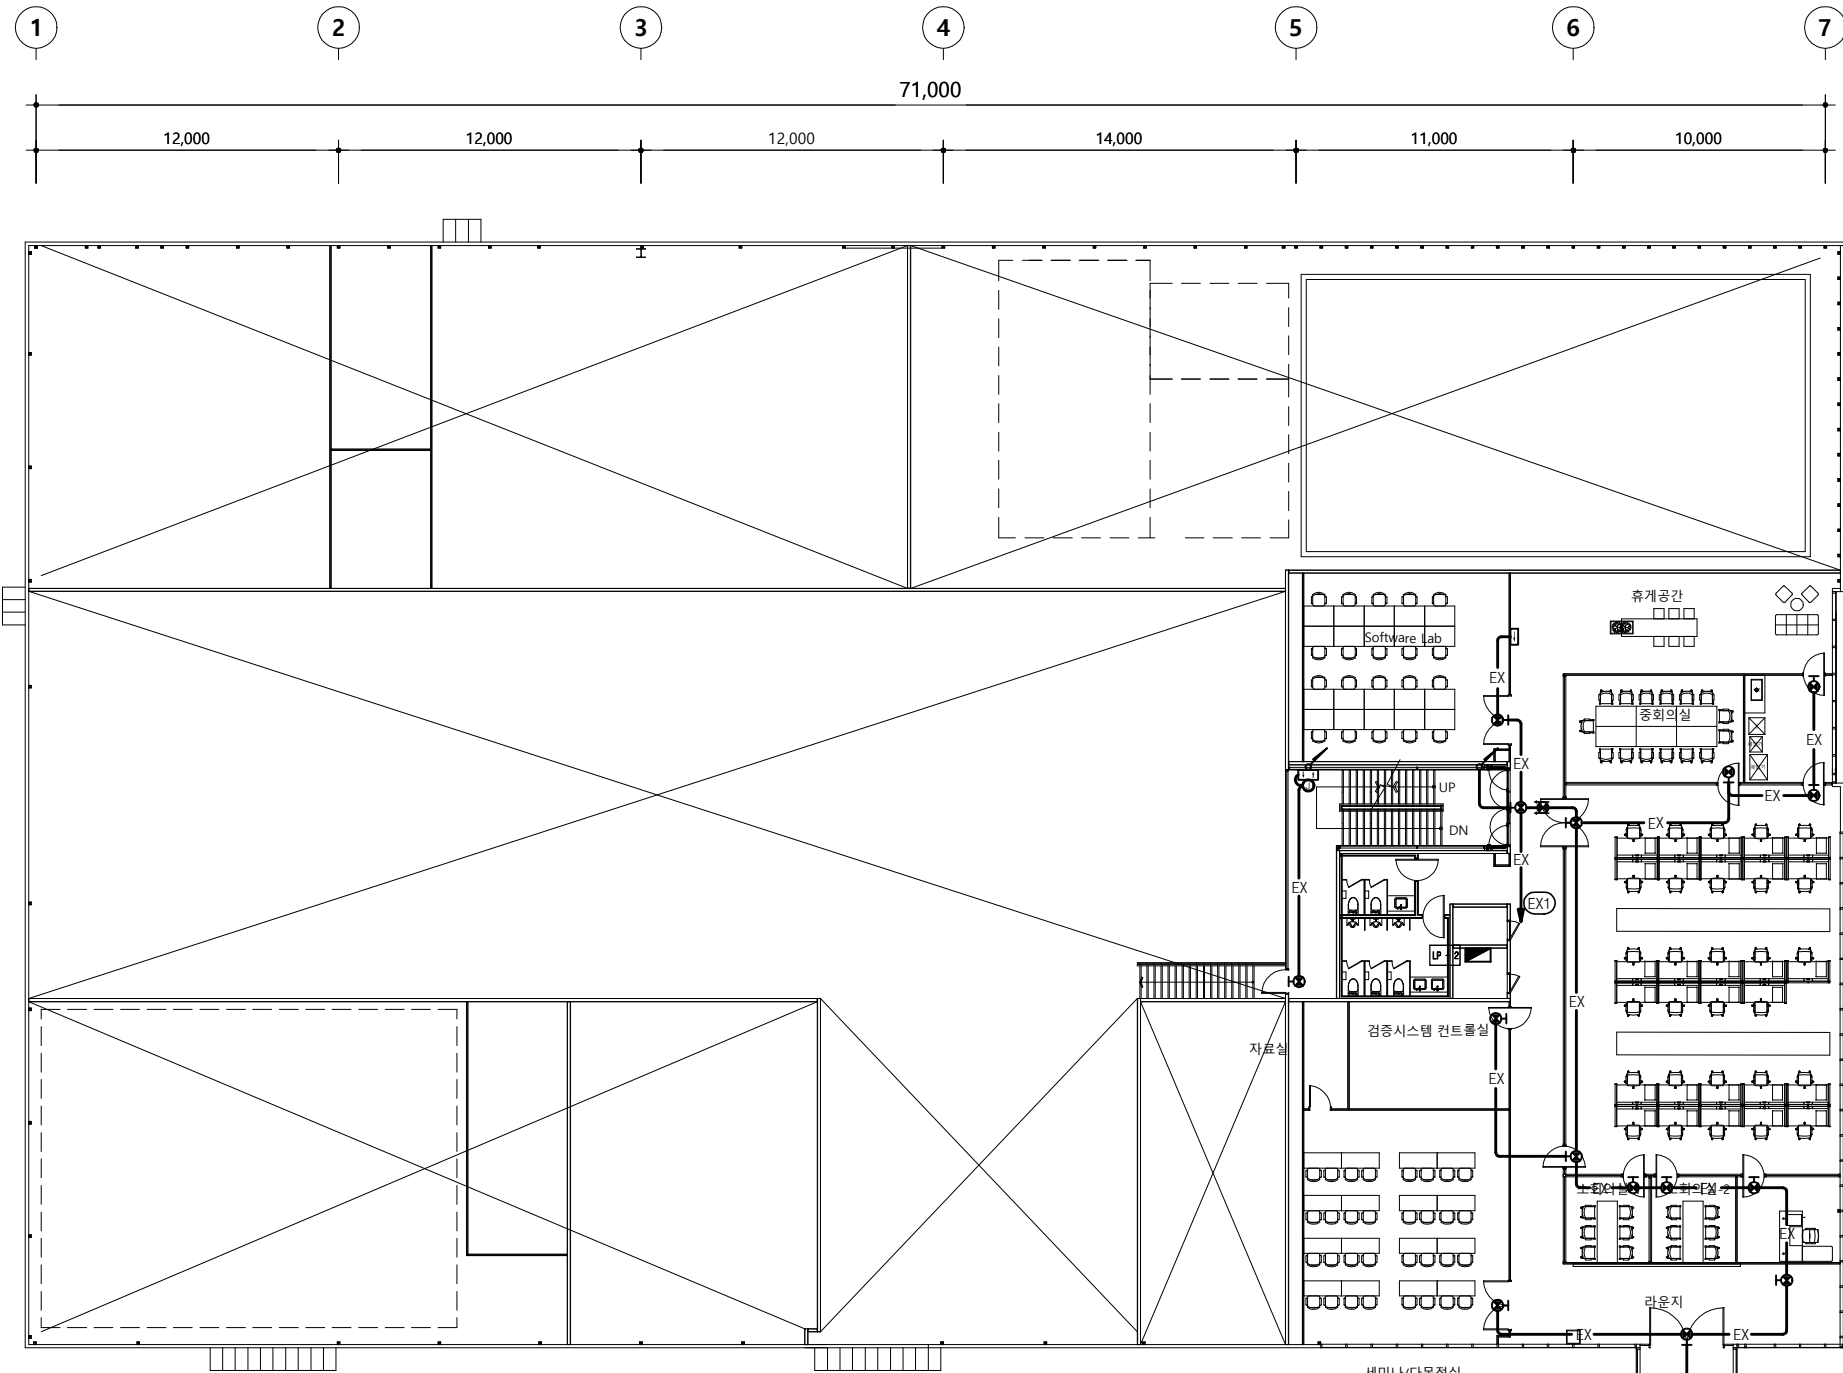

유도등 범례 및 주기사항		
심 별	명칭 및 규격	수 량
●	피난구 유도등 (전체 소형)	12EA
■	피난구 유도등 (전체 소형) 랜턴트	
□	계단 유도등-60분용(LED)	1EA
▢	복도 유도등-60분용(LED)	
▣	거실 유도등-60분용(LED)	
—EX—	HF1X 2.5mm ² x 2 E-2.5mm ² (16C)	유도등 배선

2층 유도등설비 평면도
SCALE : 1/300(A3)
SCALE : 1/150(A1)

JUNG YEON (주)정연엔지니어링
전력전문1종설계업등록 [경기안양1-1호]
건축전기설비기술사 조 성 환
전 문 소 방 시 설 설 계 업 등 록
[제2017-01-00097호]
소방설비기술사 홍 기 만
정 보 통 신 등 록 [제 E-6-825호]
정보통신책임기술자 황 선 덕
기 계 설 비 등 록 [제 E-6-825호]
건축기계설비기술사 홍 기 만
경기도 안양시 동안구 흥안대로 415,
1115호 (평촌동, 두산벤처다임)
대 표 전 화 : (031) 456 - 9666

PROJECT TITLE

LS
LS Electric
R-Center 구축

PROJECT NUMBER

224001

DESIGN CONSULTANT

가운 건축
GAUN | Architects & Engineers
[서울시 강남구 언주로 609, 10층 (논현동, 파크타워)]
Tel:82-2-3443-7799 Fax:82-2-3443-3807
www.gaun.co.kr

NOTES

KEY PLAN

△		
△		
△		
△		
△		
△		
△		
△		
NO.	DESCRIPTION	DATE

ISSUES & REVISIONS

BUILDING NAME

R-Center




DRAWING TITLE

2층 유도등설비 평면도

DRAWN	SCALE
CHECK 1 안 동 식	
CHECK 2 이 은 진	DATE
APPR 정 용 재	2024.01

DRAWING NO.

EF - 302

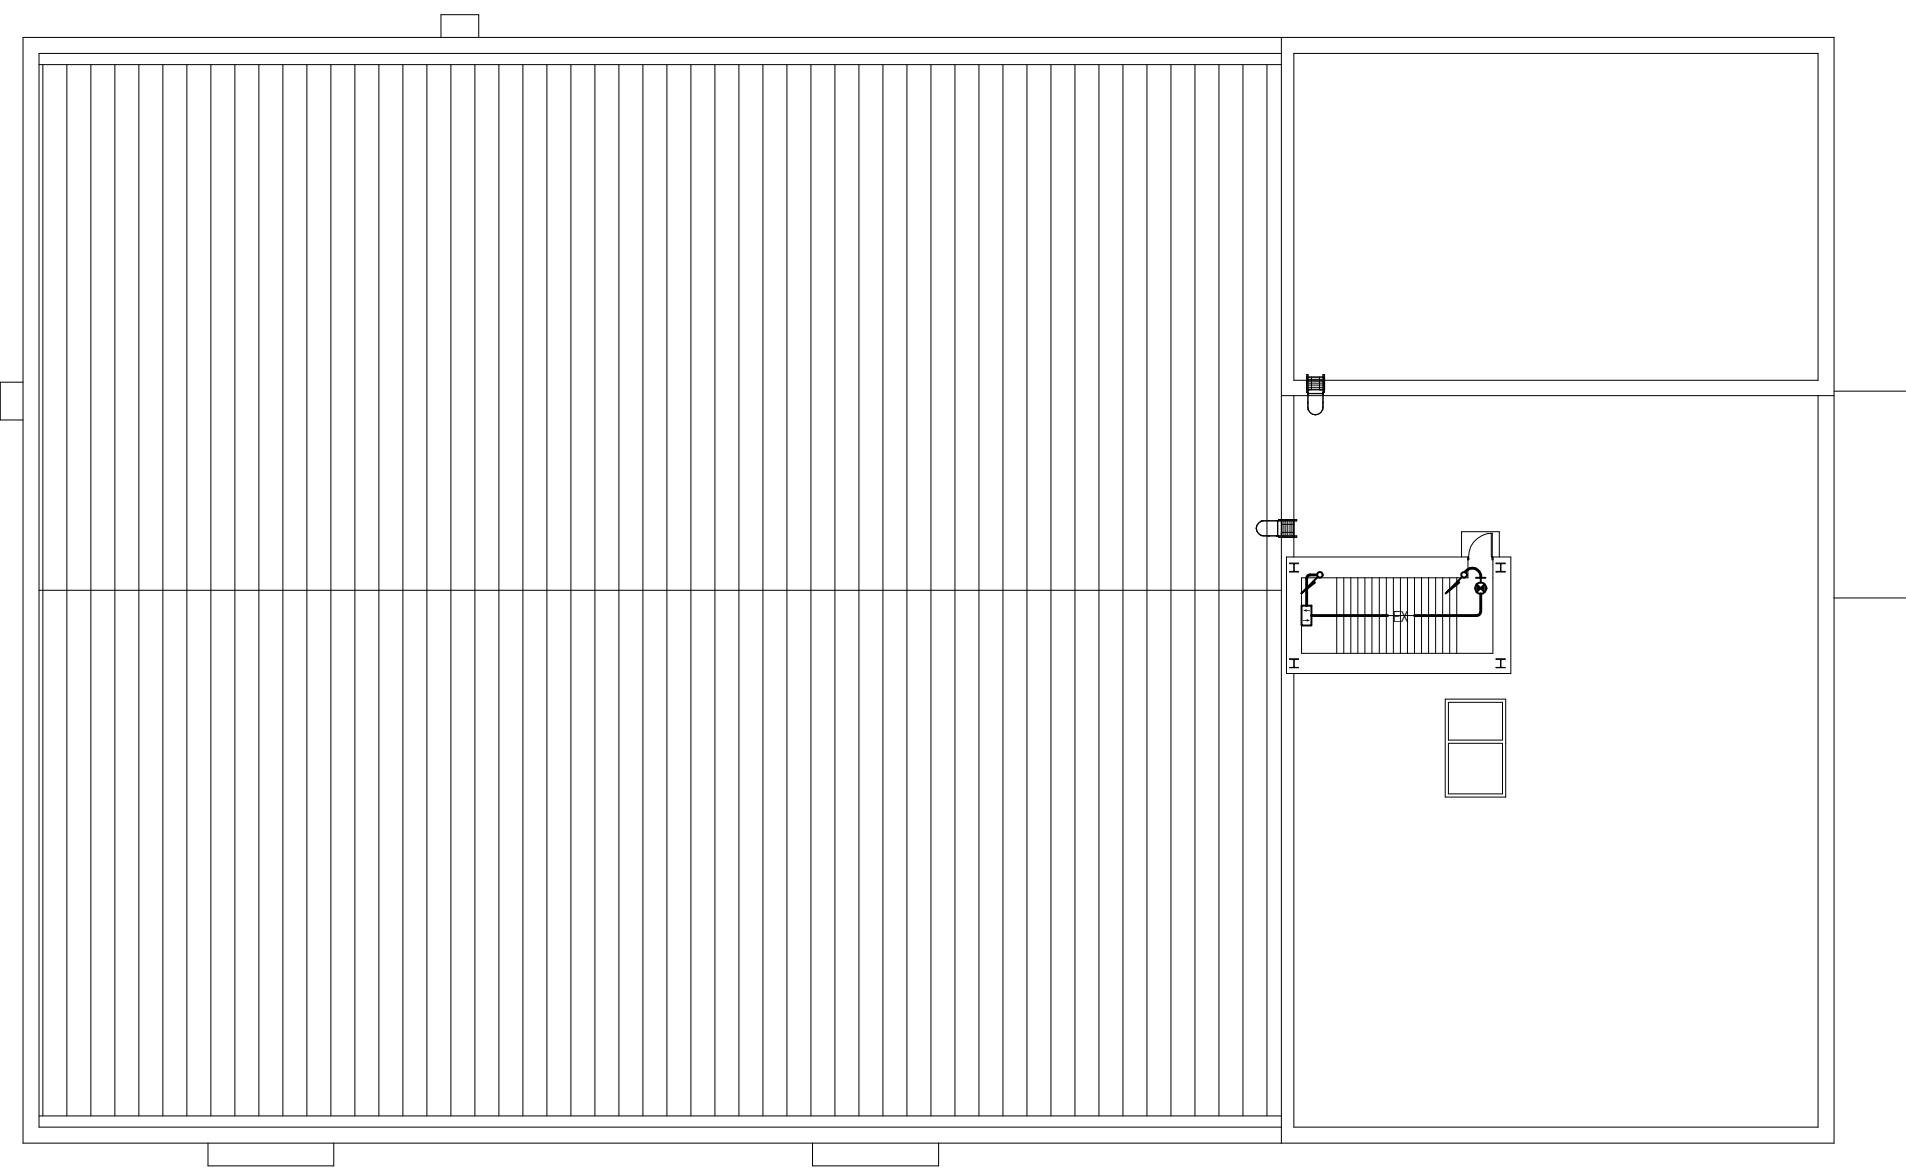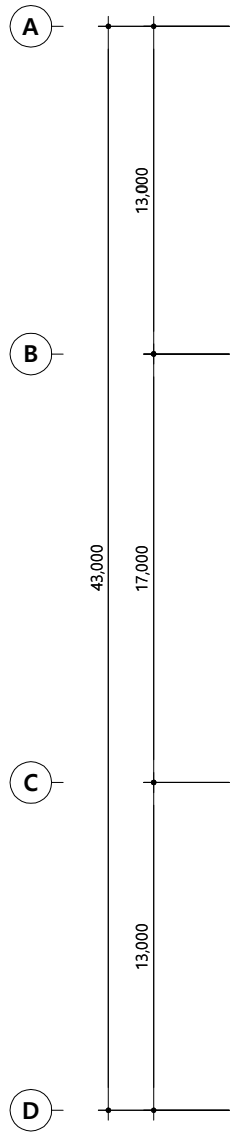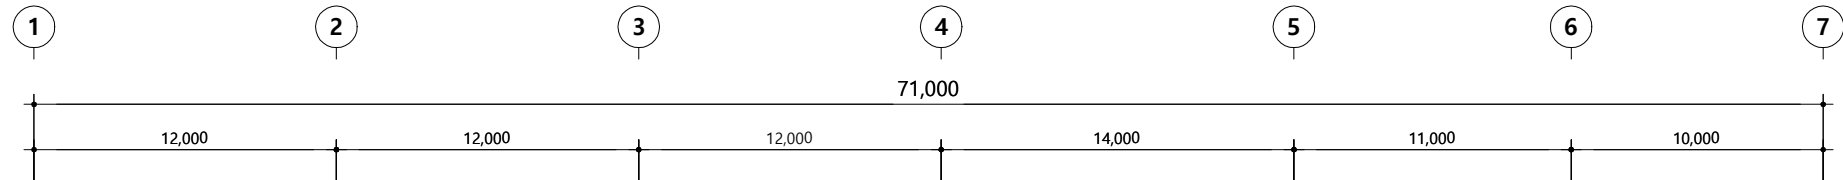

유도등 범례 및 주기사항		
심 별	명칭 및 규격	수 량
●	피난구 유도등 (전체 중형)	
■	피난구 유도등 (전체 중형) 뒀던트	
□	계단 유도등-60분용(LED)	1EA
□	복도 유도등-60분용(LED)	
□	거실 유도등-60분용(LED)	
—EX—	HF1X 2.5mm ² x 2 E-2.5mm ² (16C)	유도등 배선

○ 옥탑층 유도등설비 평면도
SCALE : 1/300(A3)
SCALE : 1/150(A1)

 (주)정연엔지니어링

전력전문1종설계업등록 [경기안양1-1호]
건축전기설비기술사 조 성 환
전 문 소 방 시 설 설 계 업 등 록
[제2017-01-00097호]
소방설비기술사 홍 기 만
정 보 통 신 등 록 [제 E-6-825호]
정보통신책임기술자 황 선 덕
기 계 설 비 등 록 [제 E-6-825호]
건축기계설비기술사 홍 기 만
경기도 안양시 동안구 흥안대로 415,
1115호,1116호 (평촌동,두산벤처다임)
대 표 전 화 : (031) 456 - 9666

PROJECT TITLE


LS Electric
R-Center 구축

PROJECT NUMBER

224001

DESIGN CONSULTANT

가운 건축
GAUN | Architects & Engineers
[서울시 강남구 언주로 609, 10층 (논현동, 팍스타워)]
Tel:82-2-3443-7799 Fax:82-2-3443-3807
www.gaun.co.kr

NOTES

KEY PLAN

△		
△		
△		
△		
△		
△		
△		
△		
NO.	DESCRIPTION	DATE

ISSUES & REVISIONS

BUILDING NAME

DRAWING TITLE

옥탑층 유도등설비 평면도

DRAWN	SCALE
CHECK 1 안 동 식	
CHECK 2 이 은 진	DATE
APPR 정 용 재	2024.01

DRAWING NO.

EF - 303