


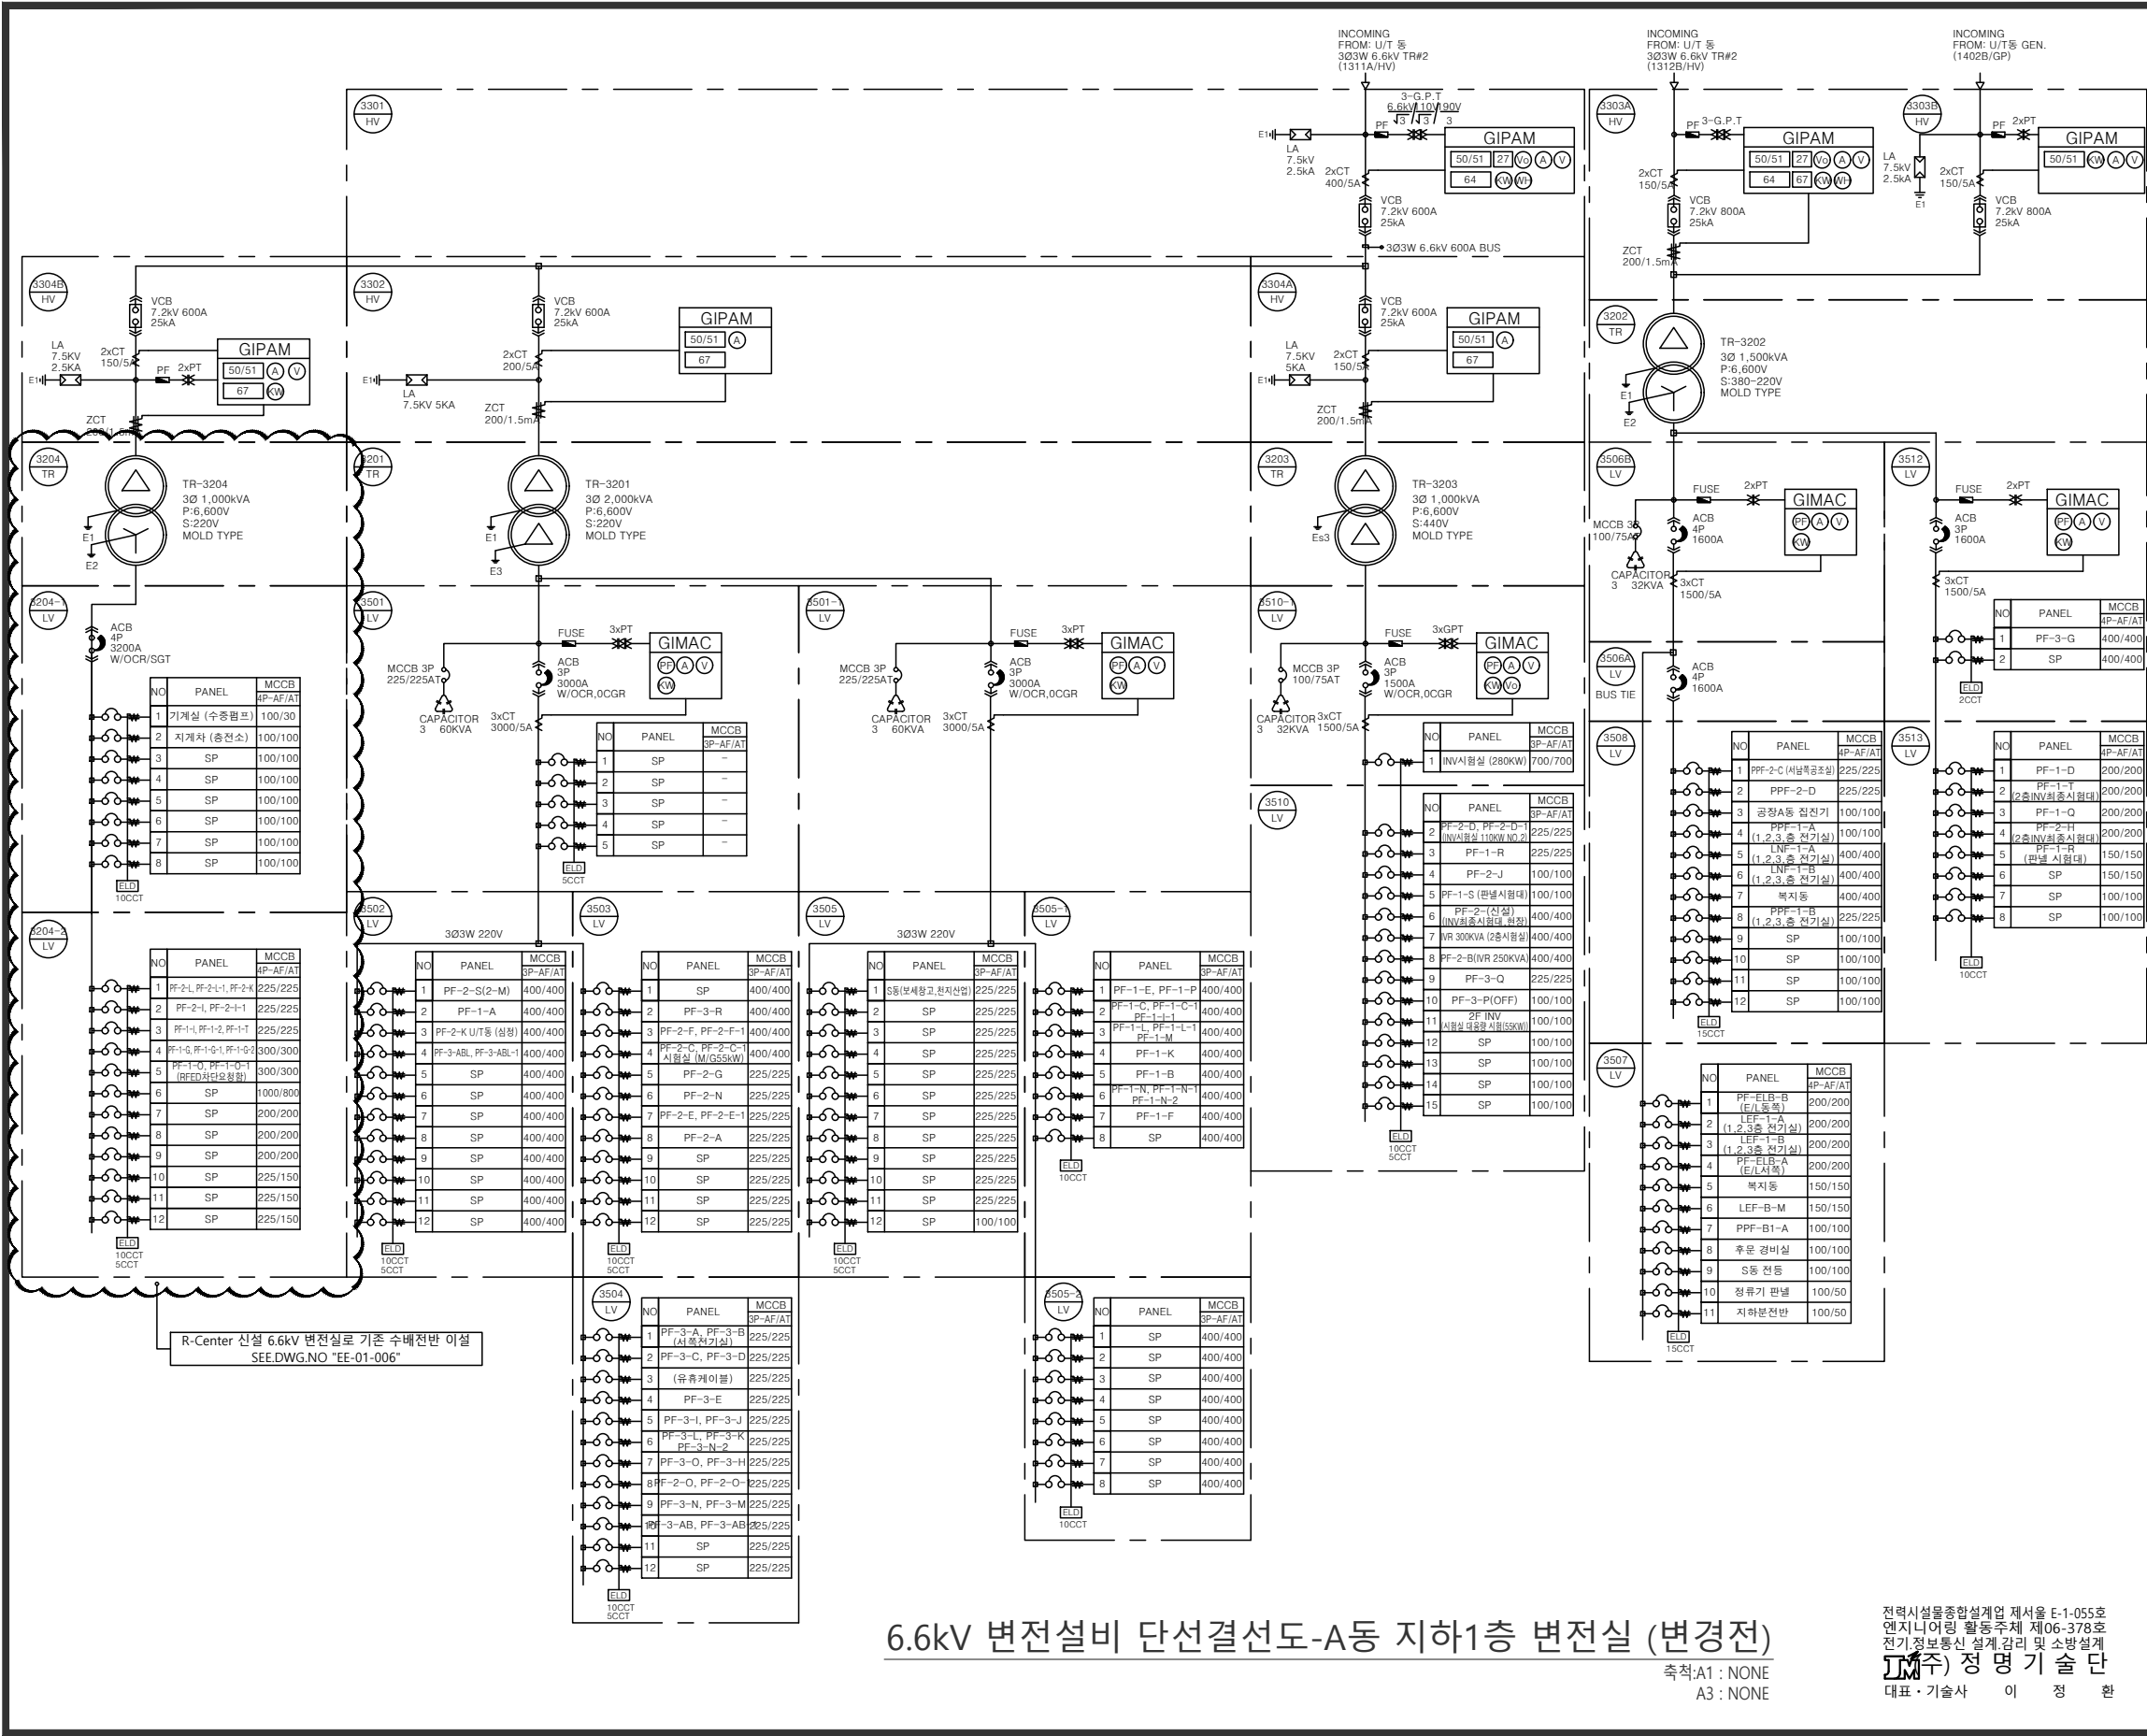

R-Center 신설 6.6kV 변전실로 기존 수배전반 이설
SEE.DWG.NO "EE-01-006"

6.6kV 변전설비 단선결선도-A동 지하1층 변전실 (변경전)

축척:A1 : NONE
A3 : NONE

전력시설물종합설계업 제서울 E-1-055호
엔지니어링 활동주체 제06-378호
전기정보통신 설계감리 및 소방설계
주) 정명기술단
대표·기술사 이 정 환



LS Electric
R-Center 구축

PROJECT NUMBER
224001

DESIGN CONSULTANT
가운 건축
GAUN | Architects & Engineers
서울시 강남구 연주로 609, 10층 (논현동, 박스타워)
Tel:82-2-3443-7799 Fax:82-2-3443-3807
www.gaun.co.kr

NOTES
1. 도면에 표기되지 않은 사항은 현장 확인 후 관계 법령의 테두리 내에서 시행하되 현장 감독관의 선승인을 득한후 시공 하도록 한다.
2. : 본공사에 해당함.

REV PLAN

△		
△		
△		
△		
△		
△		
△		
△		
NO.	DESCRIPTION	DATE

ISSUES & REVISIONS

BUILDING NAME

DRAWING TITLE
6.6kV 변전설비 단선결선도
A동 지하1층 변전실 (변경전)

DRAWN	SCALE
CHECK 1 만 동 식	A1 : NONE A3 : NONE
CHECK 2 이 은 진	DATE
APPR 정 용 재	2024.04
DRAWING NO.	

EE-01-004