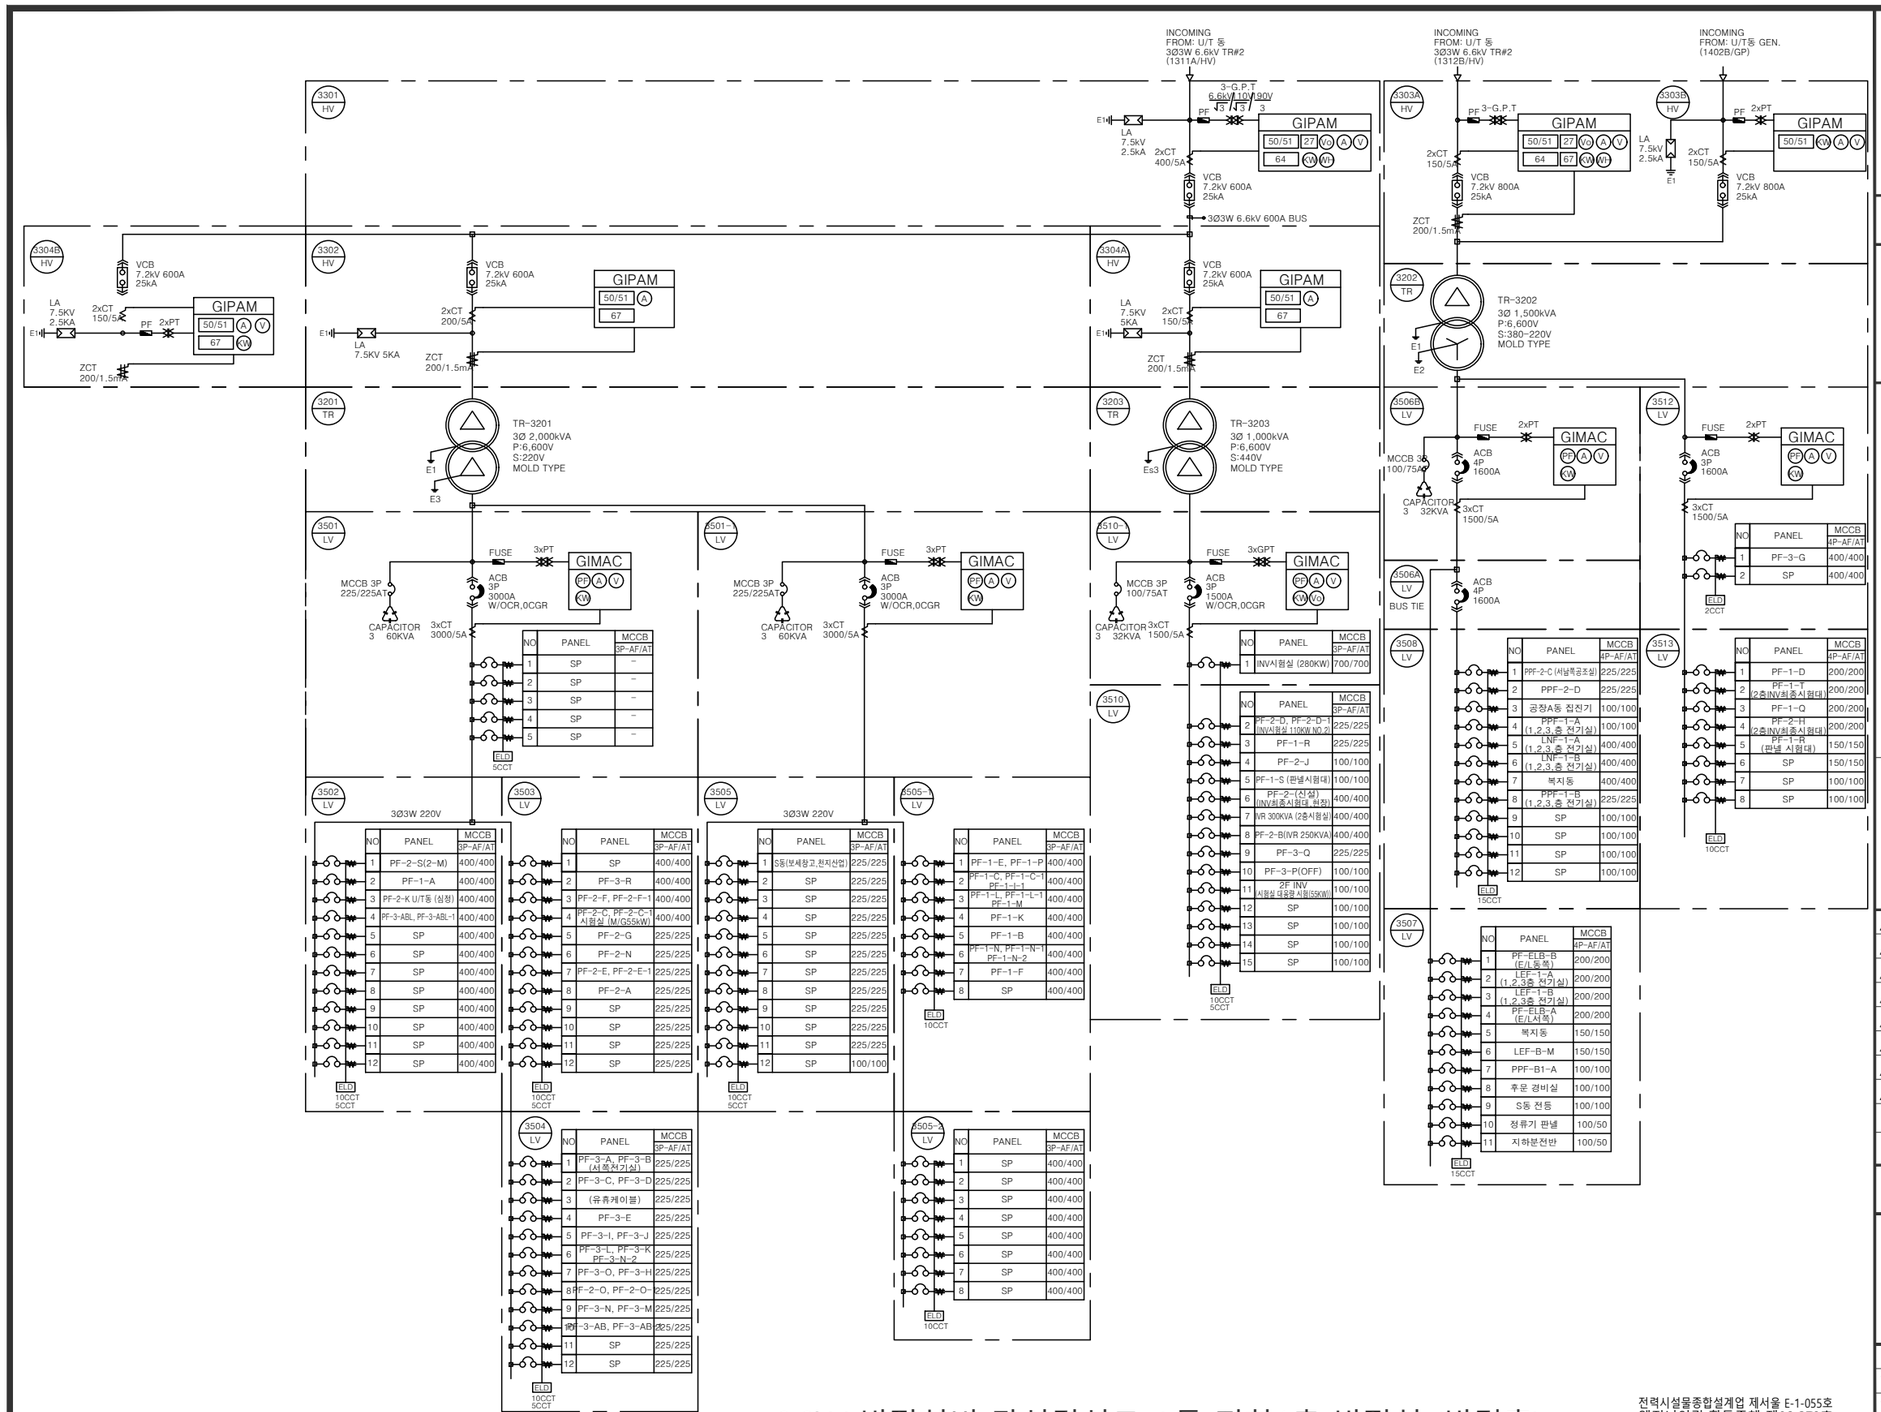

6.6kV 변전설비 단선결선도-A동 지하1층 변전실 (변경후)

축척:A1 : NONE
A3 : NONE

전력시설물종합설계업 제서울 E-1-055호
엔지니어링 활동주체 제06-378호
전기,정보통신 설계,감리 및 소방설계
(주) 정 명 기 술 단
대표 · 기술사 이 정 환

PROJECT TITLE

LS Electric
R-Center 구축

PROJECT NUMBER

224001

DESIGN CONSULTANT

가 운 건 축

GAUN | Architects & Engineers

서울시 강남구 언주로 609, 10층 (논현동, 팩스타워)
Tel:82-2-3443-7799 Fax:82-2-3443-3807
www.gaun.co.kr

NOTES

1. 도면에 표기되지 않은 사항은 현장 확인 후 관계 법령의 테두리 내에서 시행하되 현장 감독관의 선승인을 득한후 시공하도록 한다.
2. [redacted] : 본공사에 해당함.

KEY PLAN

NO.	DESCRIPTION	DATE

ISSUES & REVISIONS

BUILDING NAME

DRAWING TITLE

6.6kV 변전설비 단선결선도
A동 지하1층 변전실 (변경후)

DRAWN		SCALE: A1 : NONE, A3 : NONE
CHECK 1	안 동 식	
CHECK 2	이 은 진	DATE: 2024.04
APPR	정 용 재	

DRAWING NO.

EE-01-005