
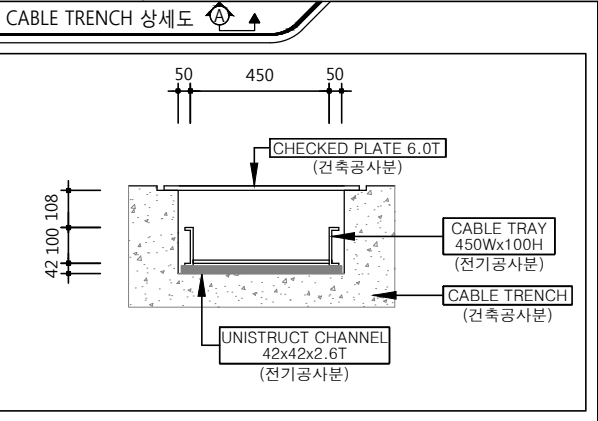


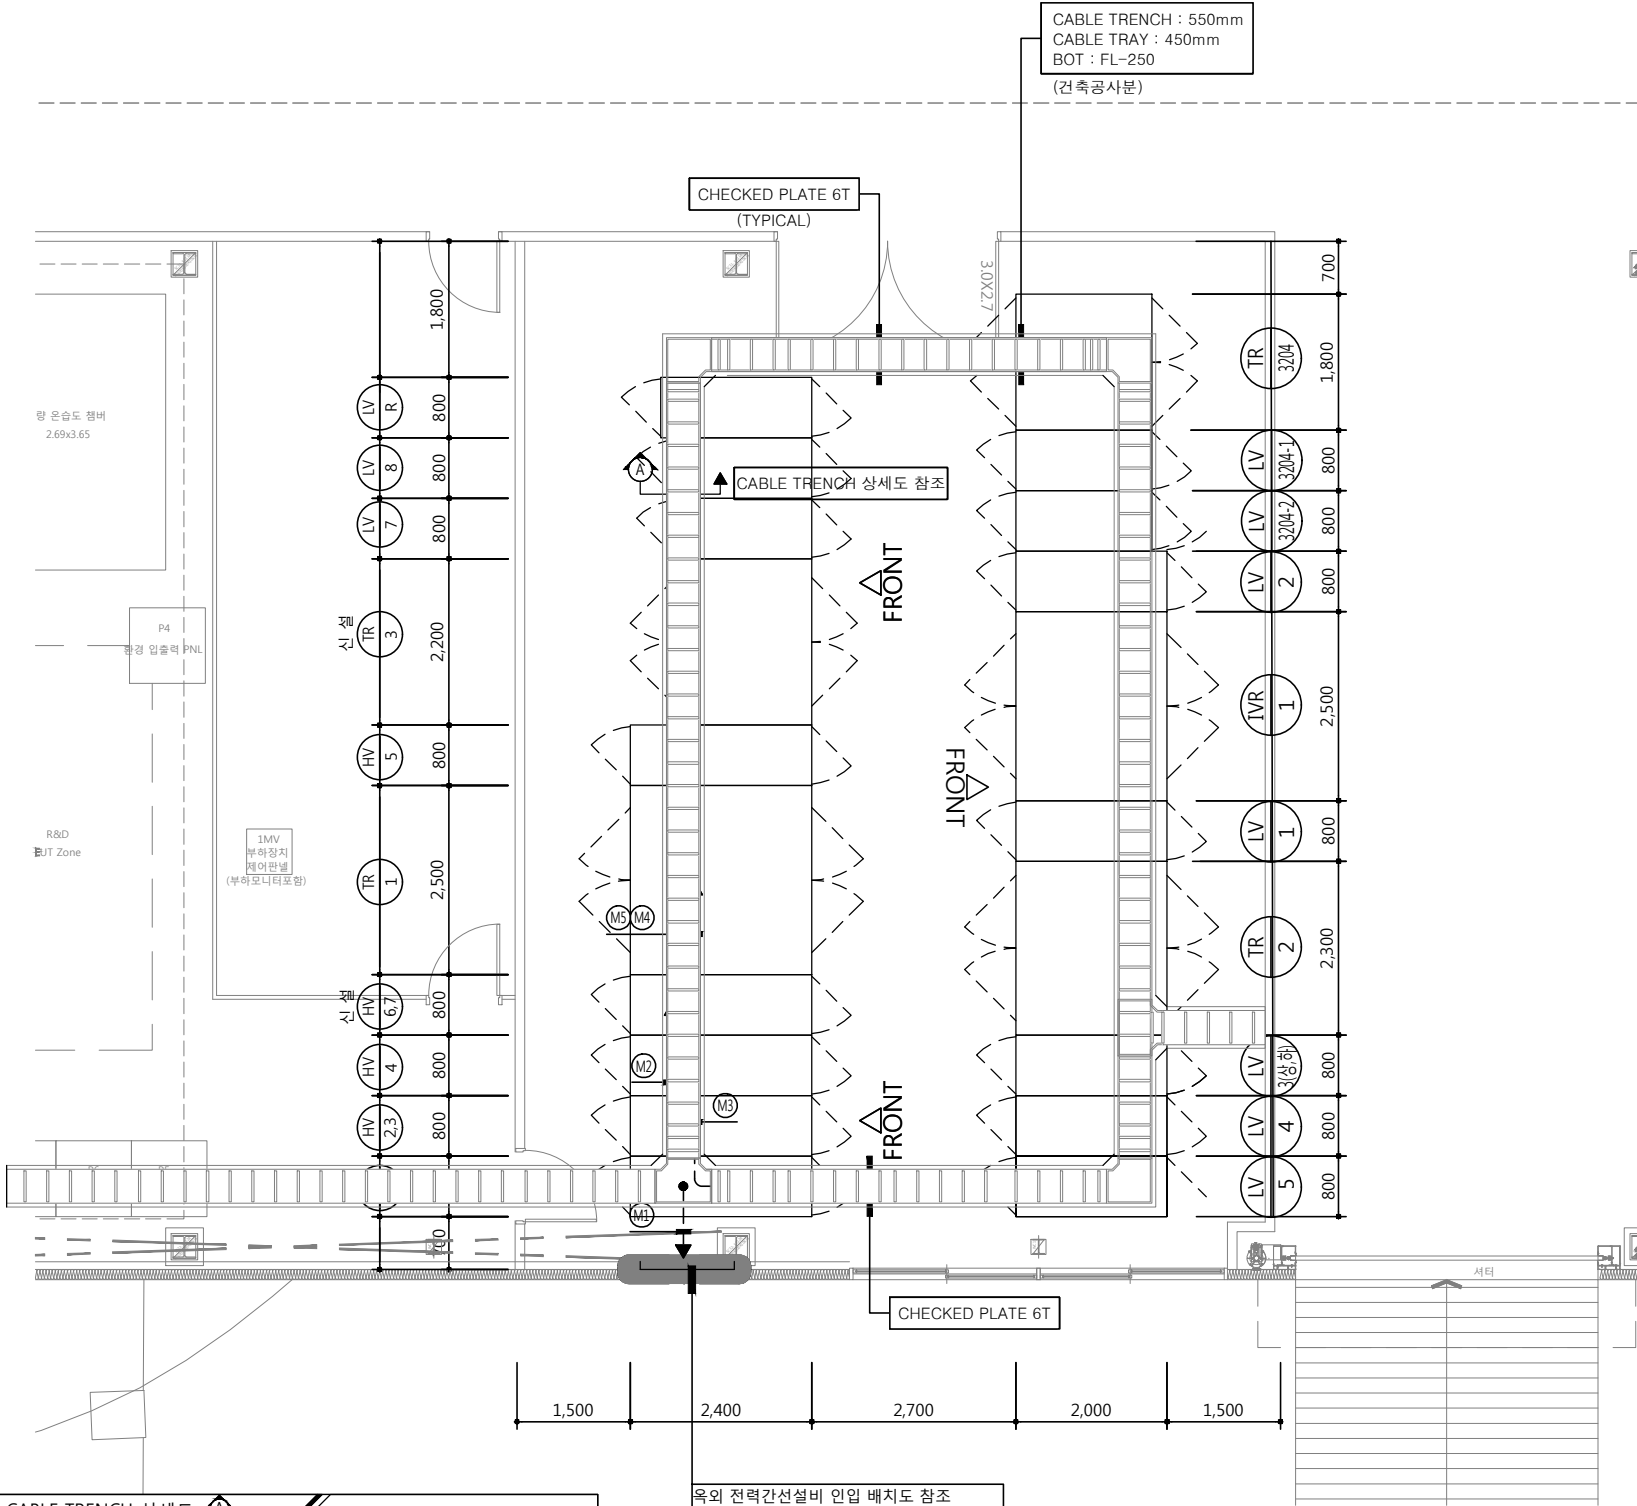

6.6KV R-Center 변전실 전력간선 확대 설비 평면도-1 (변경후)

축척:A1 : 1/ 50
A3 : 1/100

주기사항

- * 기존 이설배전반 열반시 측면 보호 커버를 제거하여 시설하여야 하며 신설 배전반은 기존이설 배전반과 동일 색상으로 제작되어야 한다.
- * 방화구획을 관통하는 부위에는 불연재의 방화재로 완전 방화구획이 되도록 차폐한다.
- * CABLE TRAY 내 배관은 제외한다.
- * CABLE TRAY 내 포설시 전선관을 제외한 TRAY용 난연성 CABLE만 포설한다.
- * EPS 및 S/S로 귀로되는 CABLE TRAY 내 접지 모선은 GV 1-120sq를 포설, S/S로 귀로되는 모든 접지선은 접지 모선에 연결한다.
- * CABLE TRAY 지지금구는 1500mm마다 견고하게 고정한다.

ELECTRICAL EQUIPMENT LIST

NO.	FROM	TO	DESCRIPTION	SIZE			Q'TY	REMARK
				W	D	H		
1	U/T 동 주변전실 HV-1317B	HV 1	6.6kV INCOMING SWGR	800	2500	2350	1	A동에서 이설 (시험센터)
2	HV 1	HV 2	6.6kV SWGR	800	2500	2350	1	A동에서 이설 (시험센터)
3		HV 3	6.6kV SWGR	800	2500	2350	1	A동에서 이설 (시험센터)
4		HV 4	6.6kV SWGR	800	2500	2350	1	A동에서 이설 (시험센터)
5			SPARE	800	2500	2350	1	A동에서 이설 (시험센터)
6		HV 6	6.6kV SWGR	800	2500	2350	1	신 설
7		HV 7	6.6kV SWGR	800	2500	2350	1	신 설
8	HV 3	TR 1	6.6kV / 3300V MOLD TR 2,000kVA	2500	2500	2350	1	A동에서 이설 (시험센터)
9	TR 1	HV 5	6.6kV SWGR	800	2500	2350	1	A동에서 이설 (시험센터)
10	HV 4	TR 2	6.6kV / 440V MOLD TR 2,000kVA	2300	2500	2350	1	A동에서 이설 (시험센터)
11	TR 2	LV 1	440V SWGR	800	2500	2350	1	A동에서 이설 (시험센터)
12	LV 1	IVR 1	440V / 320~550V MOLD TR 1,500kVA	2500	2500	2350	1	A동에서 이설 (시험센터)
13	IVR 1	LV 2	320~550V SWGR	800	2500	2350	1	A동에서 이설 (시험센터)
14	TR 2	LV 3(상)	440V SWGR	800	2500	2350	1	A동에서 이설 (시험센터)
15		LV 3(중)	440V SWGR	800	2500	2350	1	A동에서 이설 (시험센터)
16		LV 4	440V SWGR	800	2500	2350	1	A동에서 이설 (시험센터)
17		LV 5	440V SWGR	800	2500	2350	1	A동에서 이설 (시험센터)
18	HV 6	TR 3204	6.6kV / 220V MOLD TR 1,000kVA	1800	1800	2350	1	A동에서 이설 (지하 변전실)
19	TR 3204	LV 3204-1	220V SWGR	800	1800	2350	1	A동에서 이설 (지하 변전실)
20		LV 3204-2	220V SWGR	800	1800	2350	1	A동에서 이설 (지하 변전실)
21	HV 6	TR 3	6.6kV / 380V MOLD TR 2,000kVA	1800	1800	2350	1	신 설
22	TR 3	LV 7	380V SWGR	800	2200	2350	1	신 설
23	TR 3	LV 8	380V SWGR	800	2200	2350	1	신 설
24	LV 5	LV R	정류기반	800	2500	2350	1	A동에서 이설 (시험센터)

CABLE SCHEDULE

NO	FROM	TO	전 원	CABLE SCHEDULE	REMARK
M1	U/T 동 HV-1317B	HV-1	3Φ 6.6kV	10kV F-CV 150SQ/1Cx6L	CABLE TRENCH
M2	HV-3	TR-1	3Φ 6.6kV	10kV F-CV 70SQ/1Cx3L	CABLE TRENCH
M3	HV-4	TR-2	3Φ 6.6kV	10kV F-CV 70SQ/1Cx3L	CCABLE TRENCH
M4	HV-6	TR-3204	3Φ 6.6kV	10kV F-CV 70SQ/1Cx3L	CABLE TRENCH
M5	HV-7	TR-3	3Φ 6.6kV	10kV F-CV 70SQ/1Cx3L	CABLE TRENCH

전력시설물종합설계업 제서울 E-1-055호
엔지니어링 활동주체 제06-378호
전기 정보통신 설계·감리 및 소방설계
JM(주) 정 명 기 술 단
대표 · 기술사 이 정 환

LS Electric
R-Center 구축

PROJECT NUMBER
224001

DESIGN CONSULTANT
가운 건축
GAUN | Architects & Engineers
서울시 강남구 연주로 609, 10층 (논현동, 파스타워)
Tel:82-2-3443-7799 Fax:82-2-3443-3807
www.gaun.co.kr

NOTES

KEY PLAN

△		
△		
△		
△		
△		
△		
△		
△		
△		
△		
NO.	DESCRIPTION	DATE

ISSUES & REVISIONS

BUILDING NAME

DRAWING TITLE
6.6KV R-Center 변전실
전력간선 확대 설비 평면도-1

DRAWN	SCALE
CHECK 1 안 동 식	A3 : 1/ 50 A3 : 1/100
CHECK 2 이 은 진	DATE
APPR 정 용 재	2024.04

DRAWING NO.
EE-01-007