

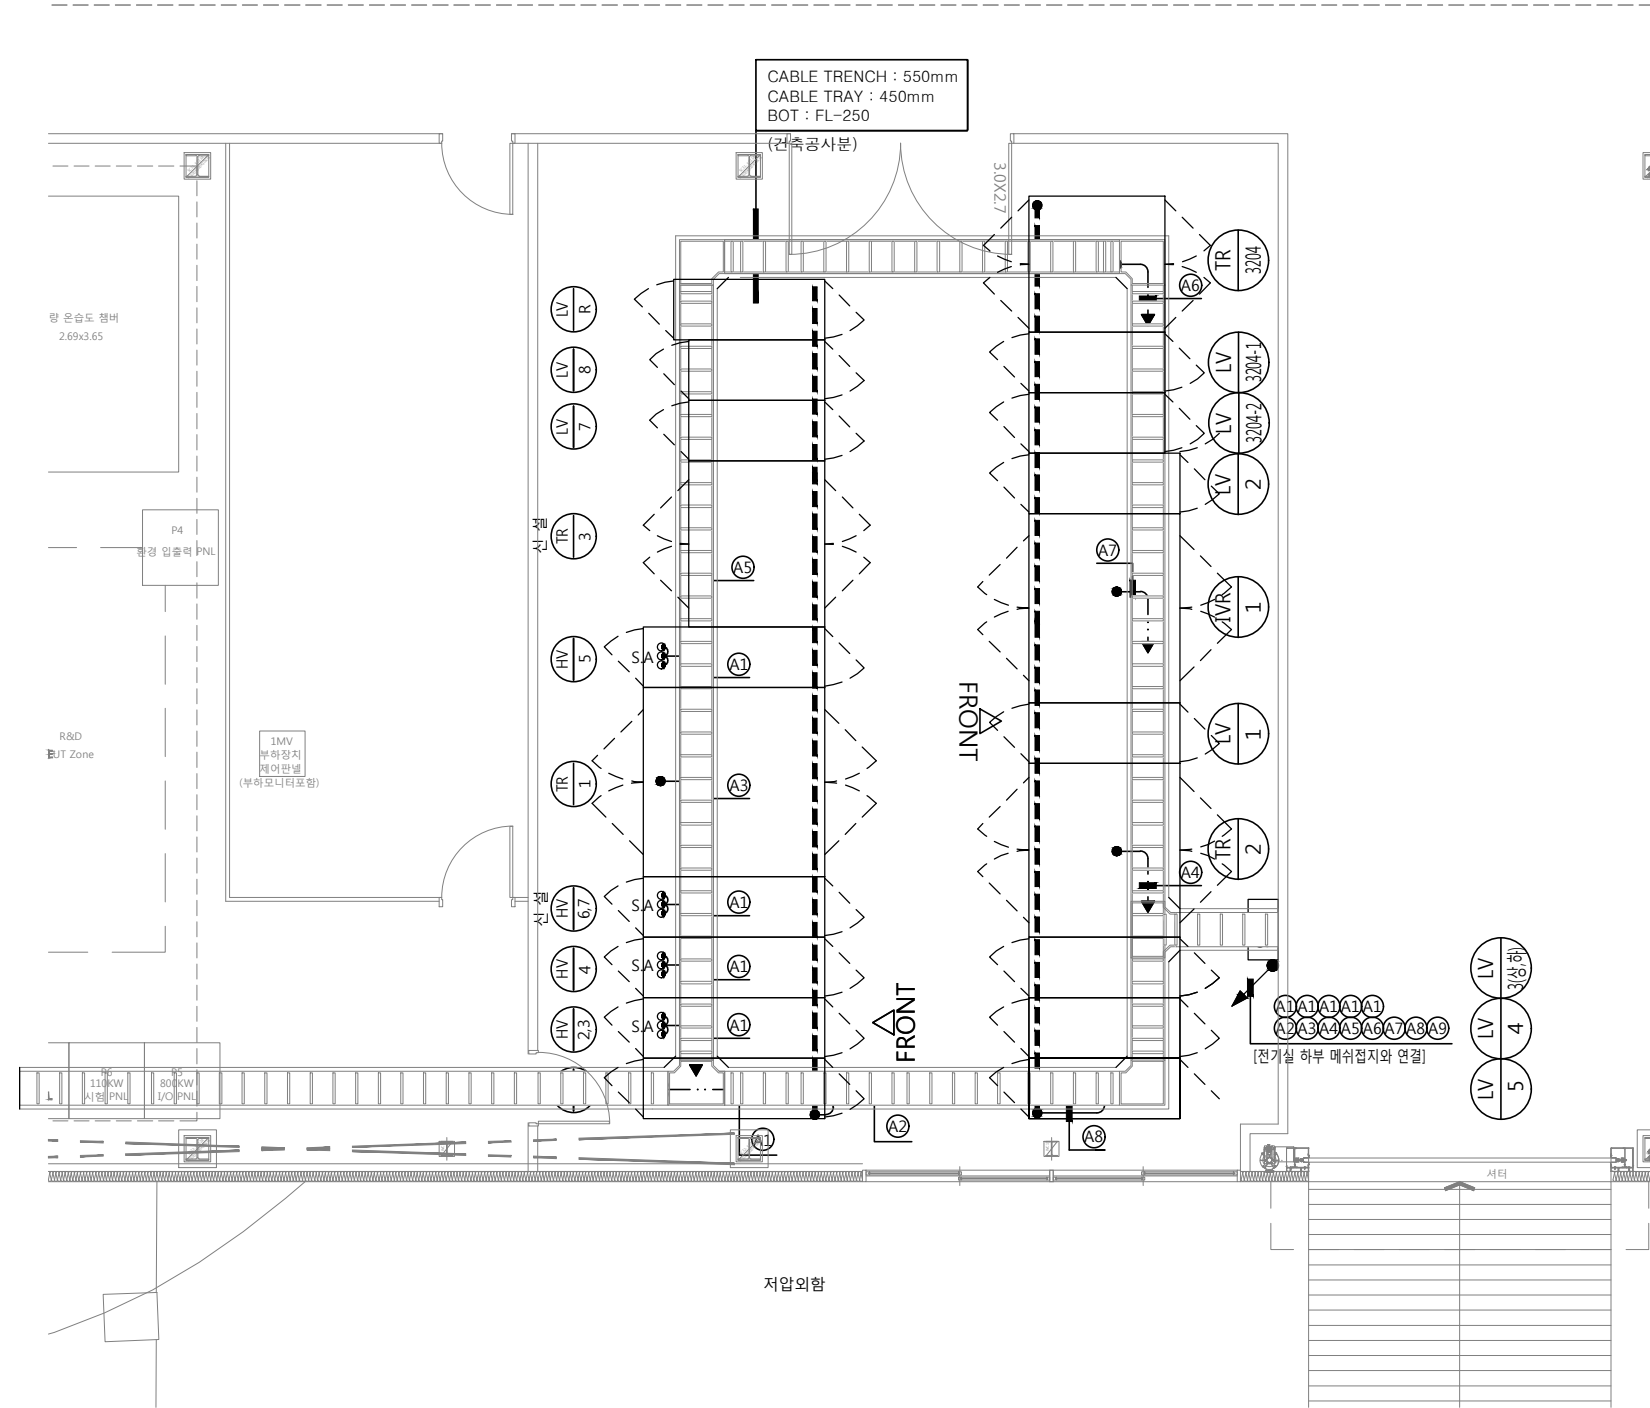


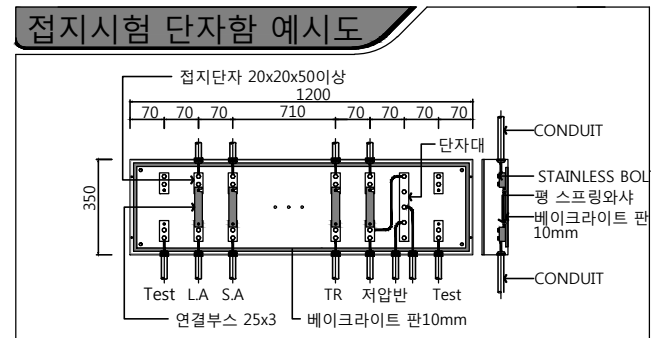

접지 CABLE SCHEDULE			
NO.	접지용도	CABLE SCHEDULE	REMARKS
A1	LA 및 SA	F-GV 120mm² (HI 36)	
A2	특고기기 및 외함 보호도체	F-GV 120mm² (HI 36)	
A3	TR-1 중성점 보호도체	F-GV 95mm² (HI 42)	
A4	TR-2 중성점 보호도체	F-GV 95mm² (HI 42)	
A5	TR-3 중성점 보호도체	F-GV 95mm² (HI 42)	
A6	TR-3204 중성점 보호도체	F-GV 95mm² (HI 42)	
A7	IVR-1 중성점 보호도체	F-GV 50mm² (HI 42)	
A8	저압기기 및 외함 보호도체	F-GV 240mm² (HI 54)	
A9	TEST - 2LINE	F-GV 16mm² (HI 16)	

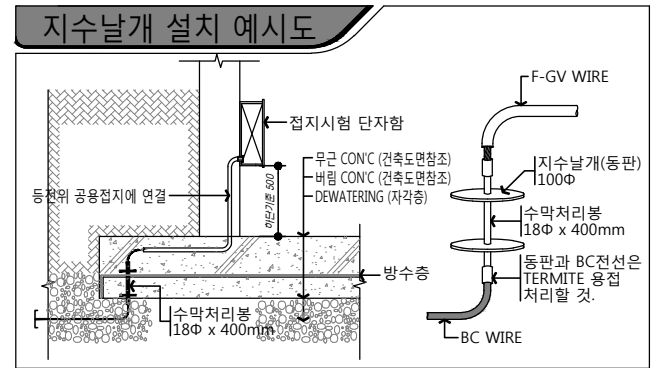

6.6KV R-Center 변전실 접지 배치 설비 평면도
(변경후)

축척: A1 : 1/50
A3 : 1/100

전력시설물종합설계업 제서울 E-1-055호
엔지니어링 활동주체 제06-378호
전기·정보통신 설계·감리 및 소방설계
정명기술(주) 정명기술
대표·기술사 이 정 환