
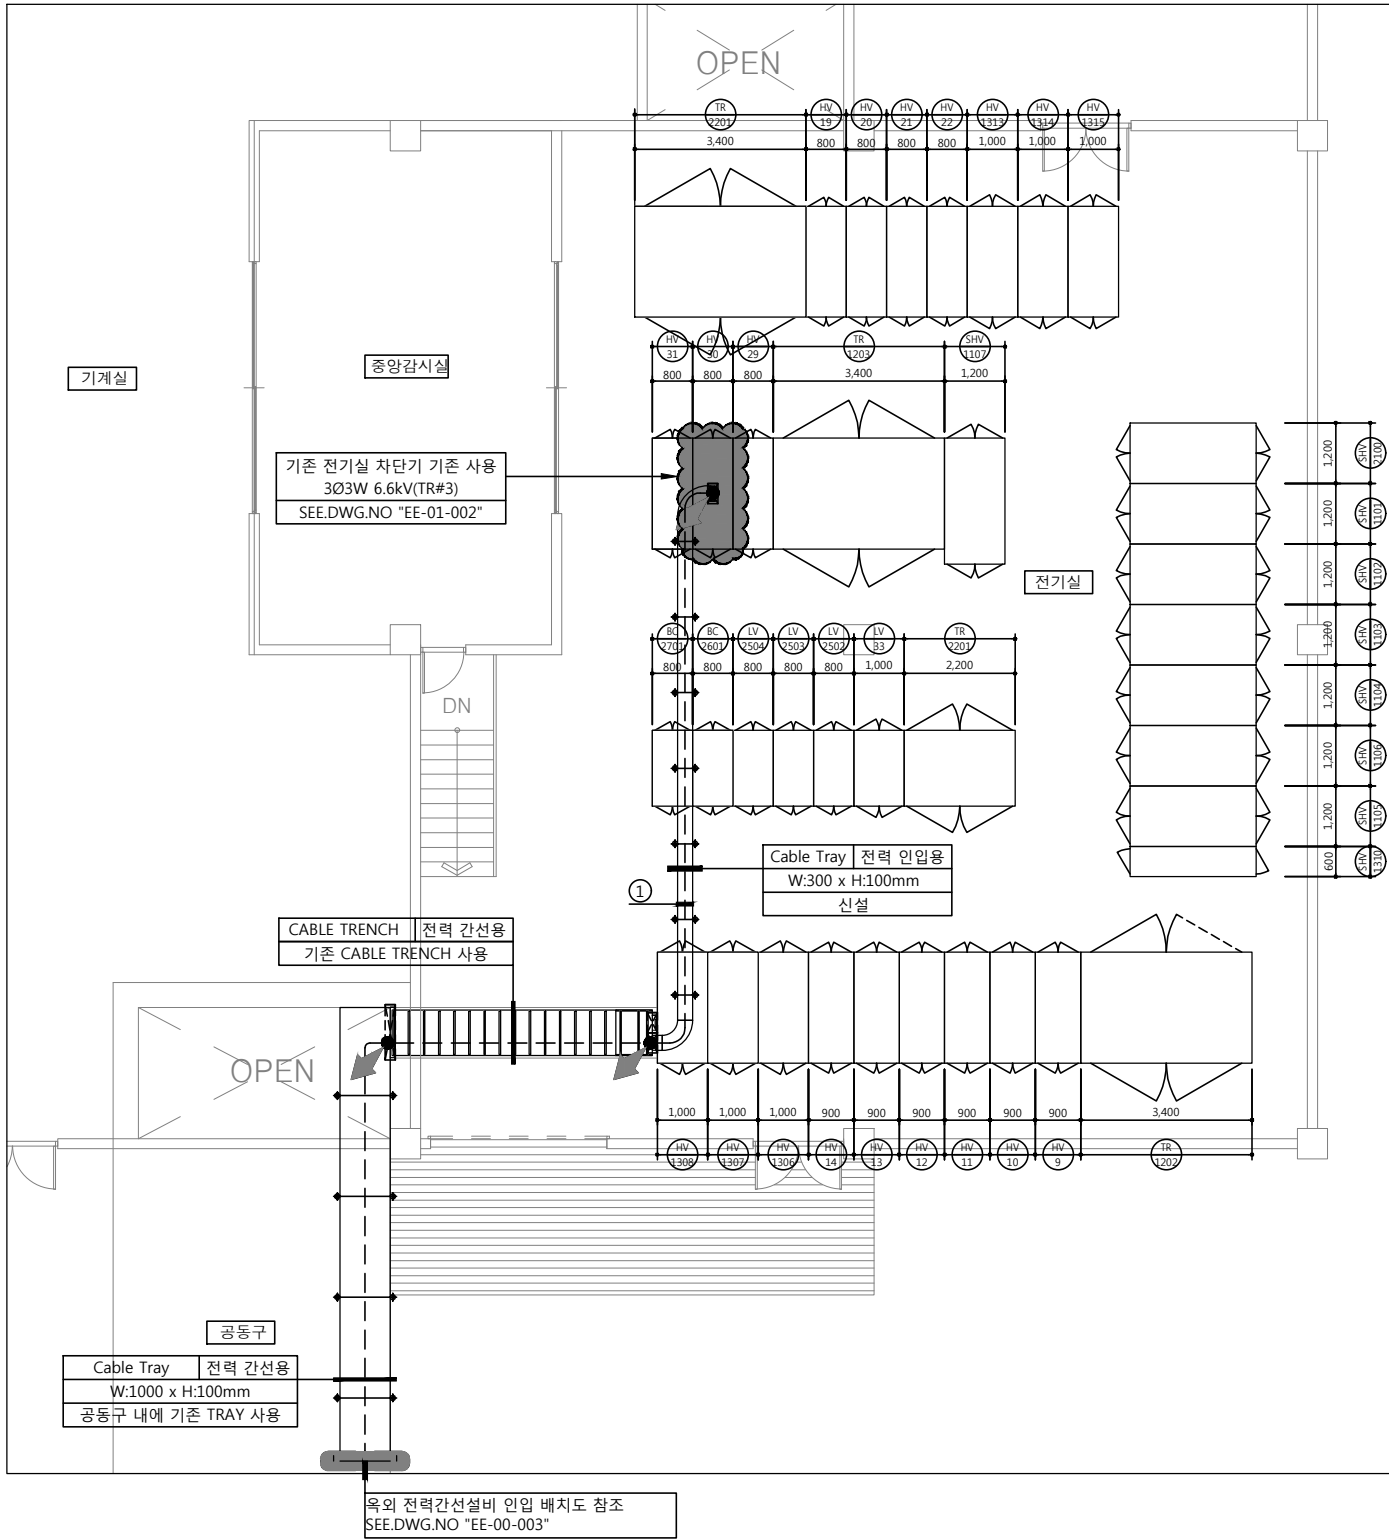
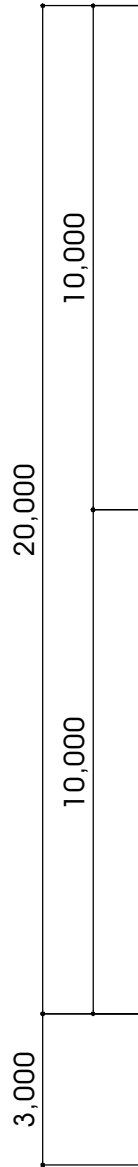


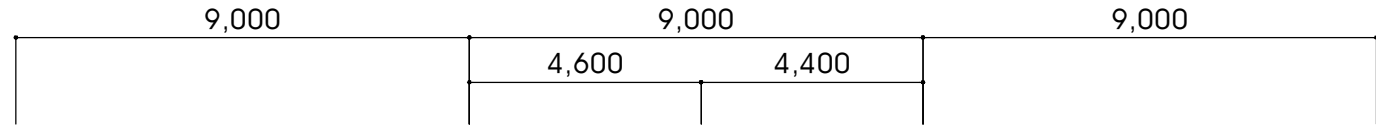

ELECTRICAL EQUIPMENT LIST							
NO.	DESCRIPTION	QTY	REMARK	NO.	DESCRIPTION	QTY	REMARK
1	SHV-1101 22.9kV INCOMING VCB	1		20	HV-1310A B2-1	1	
2	SHV-1102 22.9kV MOF	1			HV-1310B 냉동기 #4	1	
3	SHV-1103 22.9kV PT	1		21	HV-1311A 공장S동 동력	1	
4	SHV-1104 22.9kV MAIN VCB	1			HV-1311B A동 비상발전기	1	
5	SHV-1106 22.9kV TR-1202 VCB	1		22	HV-1312 6.6kV CON. VCB	1	
6	SHV-1105 22.9kV TR-1201 VCB	1			HV-1312 A동 공장동력	1	
7	SHV-1310 JUNCTION BOX	1		23	HV-1313 NO.4 CONDENSER (200KVAR)	1	
8	MOLD TR-1202 22.9/6.6kV 3000kVA	1		24	HV-1314 NO.5 CONDENSER (200KVAR)	1	
9	HV-1301 MAIN VCB	1		25	HV-1315 NO.6 CONDENSER (200KVAR)	1	
	HV-1301 SPARE	1		27	SHV-1107 22.9kV TR-1203 VCB	1	
10	HV-1302 U/T동 부속동력	1		28	MOLD TR-1203 22.9/6.6kV 3000KVA	1	
	HV-1302 비상발전기	1		29	HV-1316A INCOMING VCB	1	
11	HV-1303 오페수처리장	1			HV-1316B CON. VCB	1	
	HV-1303 비상발전기	1		30	HV-1317A 공장 A동	1	
12	HV-1304 예비	1			기존 HV-1317B ⇒ R-Center 전기실	1	
	HV-1304 6.6kV #2 냉동기	1		31	HV-1318A 냉동기 #1	1	
13	HV-1305 6.6kV CON. MAIN	1			HV-1318B SPARE	1	
	HV-1305 예비	1		32	MOLD TR-2201 6.6/0.38-0.22kV 1500kVA	1	
14	HV-1310 사무동	1		33	LV-2501 ACB INCOMING	1	
	HV-1305 예비	1			LV-2501 BATT./CHARGER	1	
15	HV-1306 NO.1 CONDENSER (200KVAR)	1		34	LV-2502 MCCB	1	
16	HV-1307 NO.2 CONDENSER (200KVAR)	1		35	LV-2503 MCCB	1	
17	HV-1308 NO.3 CONDENSER (200KVAR)	1		36	LV-2504 MCCB	1	
18	MOLD TR-1201 22.9/6.6kV 3000kVA	1		37	BC-2601 청류기반	1	
19	HV-1309 6.6kV INCOMING VCB	1		38	BA-2701 축전지반	1	
	HV-1309 6.6kV BUS TIE VCB	1		39	SHV-2100 22.9kV FEDEER VCB (21동)	1	

전력 CABLE SCHEDULE

NO.	FROM	TO	CALBE SCHEDULE
1	UT동 HV-1317B	R-Center 전기실	3Φ 3W 6.6kV F-CV 150mm ² -1C x6L (IN TRAY)
주기 사항			
1. 외벽 관통부위는 SEALING GASKET를 사용하여 누수를 예방할 수 있는 구조로한다. 2. 특고압 인입관련 P.B 및 덕트 연결부위는 접지본드를 사용하여 특고압반. 외함접지와 공용접지한다 3. 전력인입맨홀에 특고케이블(1M이상)여장을 둘 것. 4. 케이블트레이 및 덕트내에서는 배관은 제외한다. 5. CABLE TRAY는 1.5M 마다 견고하게 지지 시공한다. 6. CABLE TRAY의 벽 관통시 방화구획을 통과하는 CABLE TRAY 및 배관은 방화재를 사용하여 완전구획한다.			

U/T동 주변전실 기기 배치 설비 평면도

축척:A1 : 1/75
A3 : 1/150

전력시설물중합설계업 제서울 E-1-055호
엔지니어링 활동주체 제06-378호
전기.정보통신 설계.감리 및 소방설계
JM(주) 정명기술단
대표 · 기술사 이 정 환

PROJECT TITLE



LS Electric

R-Center 구축

PROJECT NUMBER

224001

DESIGN CONSULTANT

가운 건축

GAUN | Architects & Engineers

서울시 강남구 영주로 609, 10층 (논현동, 파스타워)


Tel:82-2-3443-7799 Fax:82-2-3443-3807

www.gaun.co.kr

NOTES

1.  : 금회 공사부분

KEY PLAN

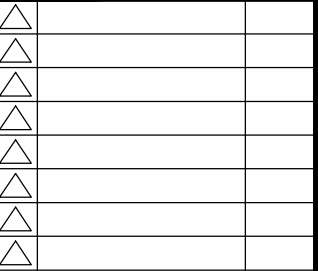

ISSUES & REVISIONS

NO.	DESCRIPTION	DATE

BUILDING NAME

DRAWING TITLE

U/T동 주변전실
기기 배치 설비 평면도

DRAWN

CHECK 1 안 동 식

CHECK 2 이 은 진

APPR 정 용 재

SCALE

A3 : 1/75
A3 : 1/150

DATE

2024.04

DRAWING NO.

EE-01-010