


P-F

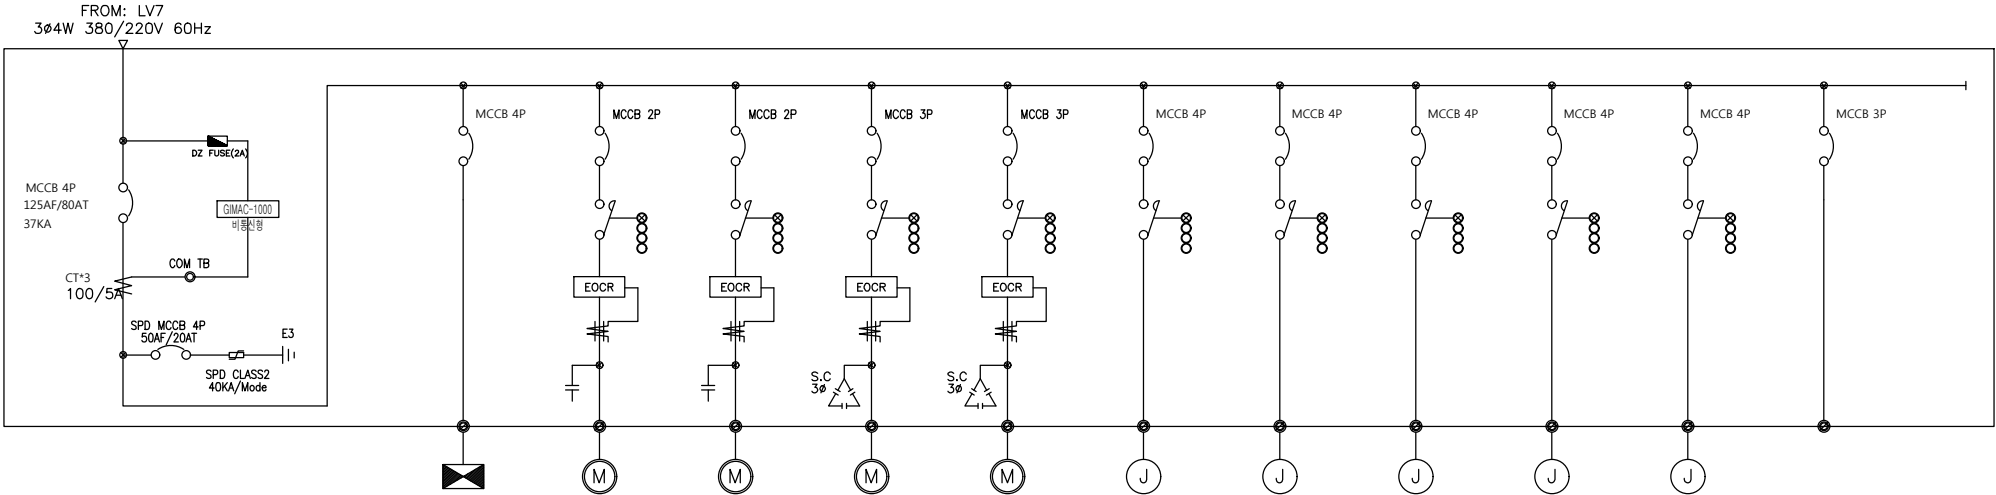

MOTOR CONTROL CENTER SCHEDULE	UNIT NO.	MAIN	1	2	3	4	5	6	7	8	9	10	11
	EQUIPMENT NO.		SP-1	SF-2	TEF-1	EF-1	SF-1	CHU-1	CHU-1	CHU-1	CHU-1	CHU-1	SP
	SERVICE NAME		배수 펌프 CONT. PNL	1층 SUPPLY FAN	옥상층 EXHAUST FAN	1층 공장 SUPPLY FAN	1층 공장 EXHAUST FAN	전정취출형 냉난방 유니트	전정취출형 냉난방 유니트	전정취출형 냉난방 유니트	전정취출형 냉난방 유니트	전정취출형 냉난방 유니트	SPARE
	CAPACITY (KW)		3 1.5kW x2	1ø 0.214 KW	1ø 0.4 KW	3ø 5.5kW	3ø 5.5kW	3ø 1.6 KW	3ø 1.6 KW	3ø 1.6 KW	3ø 1.6 KW	3ø 1.6 KW	-
	MCCB (AF/AT)	125 80 50 40 50 20 50 20 50 40 50 40 50 20 50 20 50 20 50 20 50 20 50 40											
	MCCB TYPE	ABS 104c 37KA	ABS 54c 18KA	ABS 52c 35KA	ABS 52c 35KA	ABS 53c 18KA	ABS 53c 18KA	ABS 54c 18KA	ABS 54c 18KA	ABS 54c 18KA	ABS 54c 18KA	ABS 54c 18KA	ABS 53c 18KA
	MAGNETIC CONTACTOR	88M		MC-12b	MC-12b	MC-18b	MC-18b	MC-12b	MC-12b	MC-12b	MC-12b	MC-12b	
		88D(R)											
		88S											
	EOCR TYPE			DMP06i TB	DMP06i TB	DMP65i TB	DMP65i TB						
	동작 전류 범위			0.5~6A	0.5~6A	5~65A	5~65A						
	CT & A-METER	100/5A											
	CONDENSER(uF)			1 15uF	1 20uF	3ø 50uF	3ø 50uF						
	Z.C.T			-	-	-	-	-	-	-	-	-	-
	POWER TB		4P 60A	3P 30A	3P 30A	3P 60A	3P 60A	4P 30A	4P 30A	4P 30A	4P 30A	4P 30A	3P 60A
	STAB CONNECTOR(sq)												
	CABLE(sq)	POWER	10 SQ	4 SQ	4 SQ	6 SQ	6 SQ	4 SQ	4 SQ	4 SQ	4 SQ	4 SQ	10 SQ
		CONDENSOR		4 SQ	4 SQ	4 SQ	4 SQ						
	DOOR TYPE												
	SEQUENCE TYPE		FEEDER	1상 직입	1상 직입	3? ??	3? ??	MC	MC	MC	MC	MC	FEEDER

PROJECT TITLE

LS

LS Electric
R-Center 구축

PROJECT NUMBER

224001

DESIGN CONSULTANT

가운 건축

GAUN | Architects & Engineers

서울시 강남구 영주로 609, 10층 (논현동, 파스타워)
Tel:82-2-3443-7799 Fax:82-2-3443-3807
www.gaun.co.kr

NOTES

1. EPS내 노출형 분전반의 외함 전면은 STEEL 1.6t, 속판은 STEEL 1.6t로 제작
2. EPS외 매입형 분전반의 외함 전면은 STS 1.5t,속판 STEEL 1.6t로 한다.
3. 손잡이는 누름버튼형(자물쇠 매입형) 나사등은 녹이 생기지 않는 재질로 한다.
4. 정격전압이 3P, 4P MCCB 600V, 2P MCCB 250V, ELB 220V 이상 제품 설치하도록 한다.
(프레임, 트립전류 및 차단용량은 사용전압 기준임)
5. 차단기의 변경, 추가, 삭제 등의 발생시 별도의 가공을 하지 않고 변경작업이 용이하도록 가공된 내판을 사용한다.

분기 차단기 적용 차단 용량	
30AF	5KA 이상
50AF	10KA 이상
100AF	25KA 이상
125AF	25KA 이상
250AF	25KA 이상
400AF	35KA 이상
600AF	50KA 이상

- 제품에 따라 변경이 가능함

KEY PLAN

△		
△		
△		
△		
△		
△		
△		
△		

NO.	DESCRIPTION	DATE
-----	-------------	------

ISSUES & REVISIONS

BUILDING NAME

DRAWING TITLE


동력 결선도

DRAWN	SCALE
CHECK 1 안 동 식	A1 : NONE A3 : NONE
CHECK 2 이 은 진	DATE
APPR 정 용 재	2024.04

DRAWING NO.

EE-01-013

배수펌프 CONT. PNL

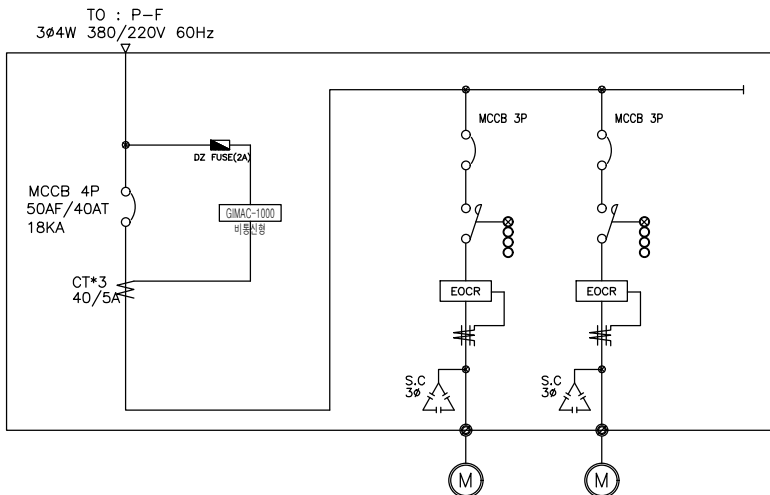

MOTOR CONTROL CENTER SCHEDULE	UNIT NO.	MAIN	1	2
	EQUIPMENT NO.		SP-1	SP-1
	SERVICE NAME		배수 펌프	배수 펌프
	CAPACITY (KW)		3ø 1.5kW	3ø 1.5kW
	MCCB (AF/AT)	50 40 50 20 50 20		
	MCCB TYPE	ABS 54c 18KA	ABS 53c 18KA	ABS 53c 18KA
	MAGNETIC CONTACTOR	88M	MC-12b	MC-12b
		88D(R)		
		88S		
	EOCR TYPE		DMP06i TB	DMP06i TB
	동작 전류 범위		0.5~6A	0.5~6A
	CT & A-METER	40/5A		
	CONDENSER(uF)		3ø 10uF	3ø 10uF
	Z.C.T		-	-
	POWER TB		3P 30A	3P 30A
	STAB CONNECTOR(sq)			
	CABLE(sq)	POWER	4 SQ	4 SQ
		CONDENSOR	4 SQ	4 SQ
	DOOR TYPE			
	SEQUENCE TYPE		3? ??	3? ??

동력 결선도

축척 : A1 : NONE
A3 : NONE

전력시설물종합설계업 제서울 E-1-055호
엔지니어링 활동주체 제06-378호
전기·정보통신 설계·감리 및 소방설계
JMM(주) 정 명 기 술 단
대표·기술사 이 정 환