NO	FROM	TO	전 원	CABLE SCHEDULE & CONDUIT		REMARK
1	S/S UT동	S/S R-Center	3Φ 3W 6.6kV	F-CV 150㎟ -1C x6L	(ELP 100ØX2)	
2	LV-7	LP-1F	3Φ 4W 380/220V	F-CV 50㎟ -1C x 4, E-25㎟	(70C)	
3	LV-7	LP-챔버	3Φ 4W 380/220V	F-CV 185㎟ -1C x 4, E-95㎟	(104C)	
4	LV-7	P-OAC-1	3Φ 4W 380/220V	F-CV 150㎟ -1C x 4, E-95㎟	(104C)	
5	LV-8	P-OAC-2	3Φ 4W 380/220V	F-CV 240㎟ -1C x 4, E-120㎟	(104C)	
6	LV-7	P-OAC-3	3Φ 4W 380/220V	F-CV 120㎟ -1C x 4, E-70㎟	(82C)	
7	LV-8	P-F	3Φ 4W 380/220V	F-CV 25㎟ -4C x 1, E-16㎟	(54C)	
8	P-A-4PP-5	IVR-2	3Φ 3W 440V	F-CV 240㎟ -1C x 3	(82C)	
9	LP-1F	LP-2F	3Φ 4W 380/220V	F-CV 10㎟ -4C x 1, E-10㎟	(42C)	
A1	LV-3204-1	P-A-2PP-1	3Φ 3W 220V	F-CV 240㎟ -1C x 3, E-120㎟	(104C)	
A2	LV-3204-1	P-A-2PP-2	3Φ 3W 220V	F-CV 185㎟ -1C x 3, E-95㎟	(104C)	
A3	LV-3204-2	P-C-2PP	3Φ 3W 220V	F-CV 35㎟ -1C x 3, E-25㎟	(54C)	
A4	LV-3204-1	P-D-2PP	3Φ 3W 220V	F-CV 35㎟ -1C x 3, E-25㎟	(54C)	
A5	LV-3204-2	P-E-2PP-1	3Φ 3W 220V	F-CV 300㎟ -1C x 3, E-150㎟	(104C)	
A6	LV-3204-2	P-E-2PP-2	3Φ 3W 220V	F-CV 240㎟ -1C x 3, E-120㎟	(104C)	
A7	LV-3204-1	P-EA-2PP	3Φ 3W 220V	F-CV 35㎟ -1C x 3, E-25㎟	(54C)	
A8	LV-3204-2	P-F-2PP	3Φ 3W 220V	F-CV 150㎟ -1C x 3, E-95㎟	(82C)	
A9	LV-3204-2	P-G-2PP	3Φ 3W 220V	F-CV 70㎟ -1C x 3, E-35㎟	(54C)	
A10	LV-3204-2	P-I-2PP	3Φ 3W 220V	F-CV 50㎟ -1C x 3, E-25㎟	(54C)	

NO	FROM	TO	전 원	CABLE SCHEDULE & CONDUIT		REMARK
B1	LV-8	P-A-3PP-1	3Φ 4W 380V	F-CV 120㎟ -1C x 4, E-70㎟	(82C)	
B2	LV-8	P-AC-3PP	3Φ 4W 380V	F-CV 35㎟ -1C x 4, E-25㎟	(54C)	
B3	LV-8	P-D-3PP	3Φ 4W 380V	F-CV 35㎟ -1C x 4, E-25㎟	(54C)	
B4	LV-8	P-E-3PP	3Φ 4W 380V	F-CV 120㎟ -1C x 4, E-70㎟	(82C)	
B5	LV-8	P-F-3PP	3Φ 4W 380V	F-CV 35㎟ -1C x 4, E-25㎟	(54C)	
B6	LV-8	P-G-3PP	3Φ 4W 380V	F-CV 120㎟ -1C x 4, E-70㎟	(82C)	
B7	LV-8	P-I-3PP	3Φ 4W 380V	F-CV 35㎟ -1C x 4, E-25㎟	(54C)	
C1	LV-4	P-A-4PP-1	3Φ 3W 440V	F-CV 240㎟ -1C x 3, E-120㎟ F-CV 240㎟ -1C x 3	(104C) (104C)	
C3	LV-5	P-A-4PP-3	3Φ 3W 440V	F-CV 300㎟ -1C x 3, E-150㎟	(104C)	
C4	LV-5	P-A-4PP-4	3Φ 3W 440V	F-CV 300㎟ -1C x 3, E-150㎟	(104C)	
C5	LV-4	P-A-4PP-5	3Φ 3W 440V	F-CV 300㎟ -1C x 3, E-150㎟	(104C)	
C7	LV-5	P-A-4PP-7	3Φ 3W 440V	F-CV 150㎟ -1C x 3, E-95㎟	(82C)	
C8	LV-1	P-AC-4PP-1	3Φ 3W 440V	F-CV 50㎟ -1C x 3, E-25㎟	(54C)	
C9	LV-5	P-C-4PP	3Φ 3W 440V	F-CV 35㎟ -1C x 3, E-25㎟	(54C)	
C10	LV-4	P-E-4PP	3Φ 3W 440V	F-CV 50㎟ -1C x 3, E-25㎟	(54C)	
C11	LV-5	P-F-4PP	3Φ 3W 440V	F-CV 300㎟ -1C x 3, E-150㎟	(104C)	
C12	LV-5	P-P-4PP	3Φ 3W 440V	F-CV 35㎟ -1C x 3, E -25㎟	(54C)	

NO	FROM	TO	전 원	CABLE SCHEDULE & CONDUIT		REMARK
D1	LV-8	P-A-3PP	3Φ 4W 380V	F-CV 120㎟ -1C x 4, E-70㎟	(82C)	
D2	LV-1	P-A-4PP-8	3Φ 4W 380V	F-CV 240㎟ -1C x 8, E-70㎟	(104C)	
D3	LV-7	P-C-3PP	3Φ 4W 380V	F-CV 185㎟ -1C x 4, E-70㎟	(104C)	
D4	LV-7	P-E-3PP-1	3Φ 4W 380V	F-CV 240㎟ -1C x 4, E-25㎟	(104C)	

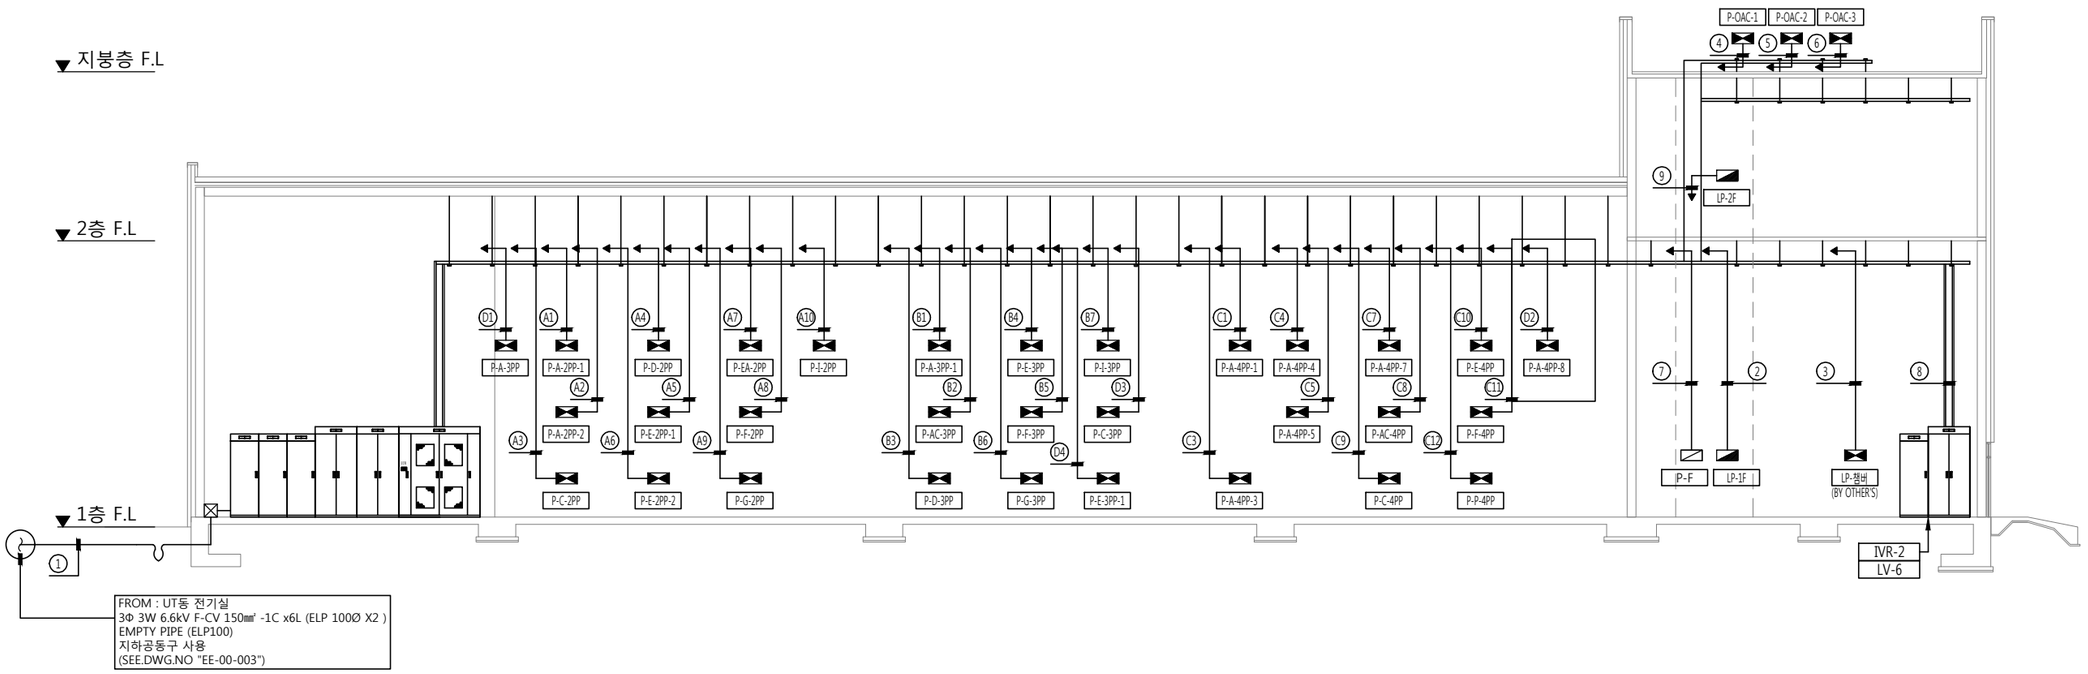

R-Center 전력간선설비 계통도

축척:A1 : 1/NONE
A3 : 1/NONE

전력시설물종합설계업 제서울 E-1-055호
엔지니어링 활동주체 제06-378호
전기,정보통신 설계,감리 및 소방설계
(주) 정 명 기 술 단
대표・기술사 이 정 환

PROJECT TITLE

LS Electric
R-Center 구축

PROJECT NUMBER

224001

DESIGN CONSULTANT

가 운 건 축
GAUN | Architects & Engineers
서울시 강남구 언주로 609, 10층 (논현동, 팍스타워)
Tel:82-2-3443-7799 Fax:82-2-3443-3807
www.gaun.co.kr

NOTES

KEY PLAN

NO.	DESCRIPTION	DATE

ISSUES & REVISIONS

BUILDING NAME

DRAWING TITLE

R-Center 지상1층
전기실 확대평면도

DRAWN		SCALE	A3 : 1/NONE A3 : 1/NONE
CHECK 1	안 동 식		
CHECK 2	이 은 진	DATE	2024.04
APPR	정 용 재		

DRAWING NO.

EE-02-001