
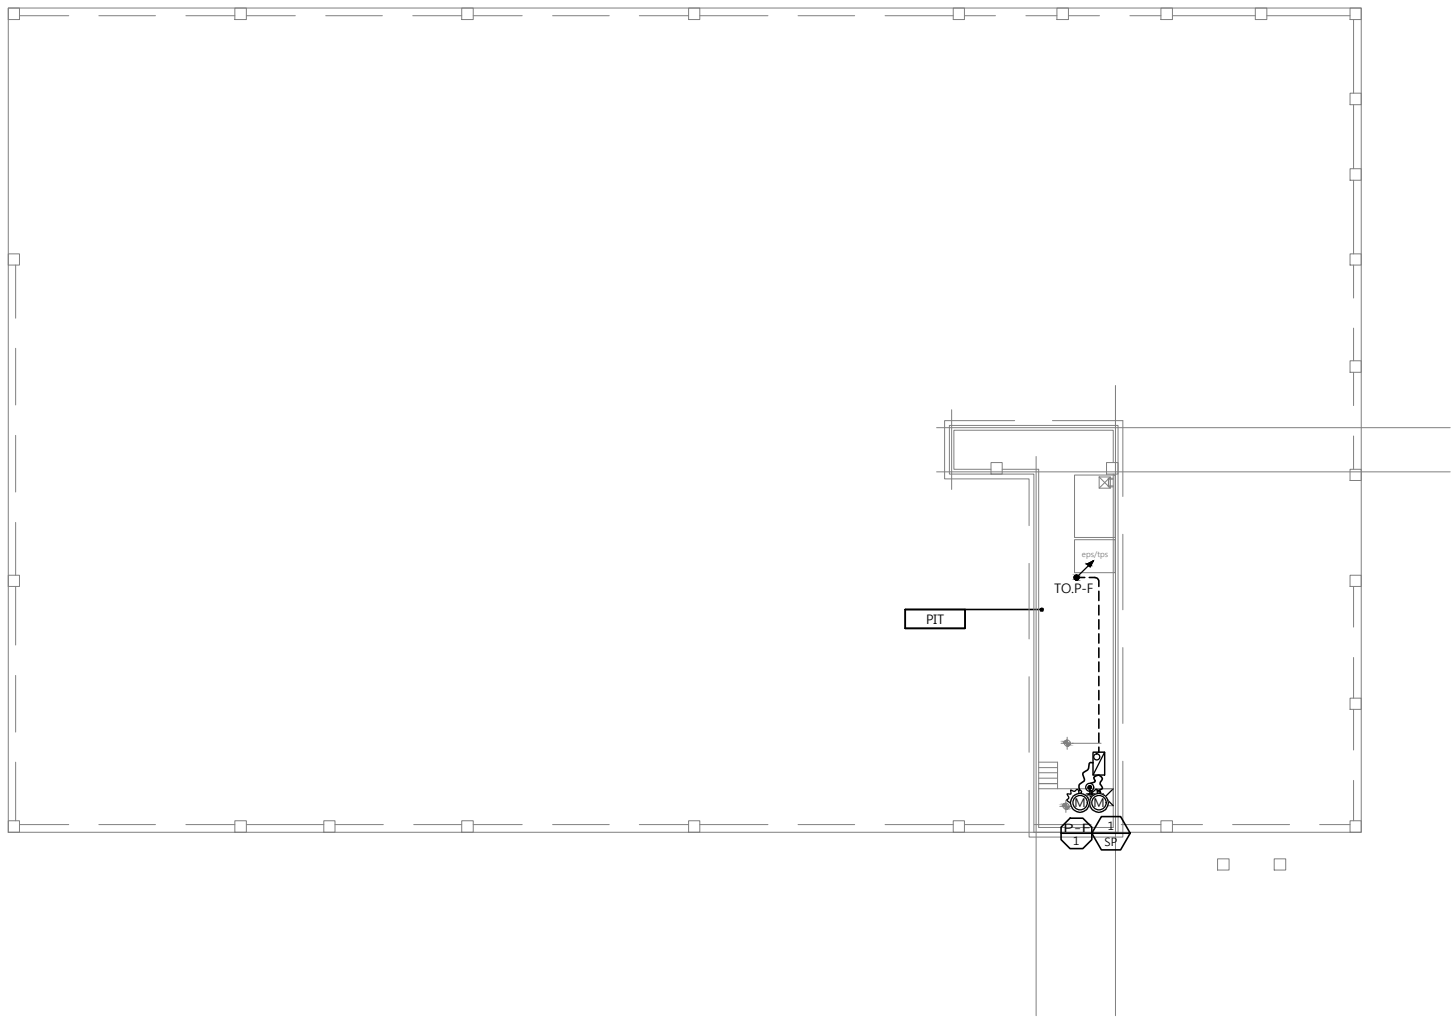
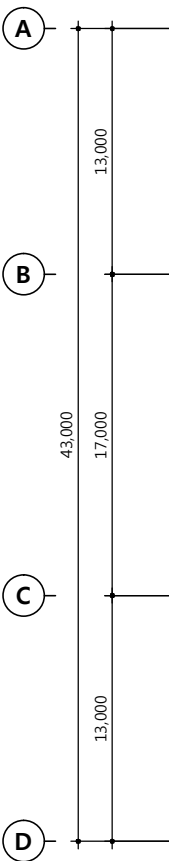


동력 설비 Cable Schedule							
PNL명	회로 번호	장비 번호	전압 방식	용량 (KW)	장비명	Cable & Conduit size	비고
P-F	1	1	3Ø 380V	1.5 x 2	배수 펌프 CONT. PNL	42C (F-CV 4C/10sq, E-10sq)	

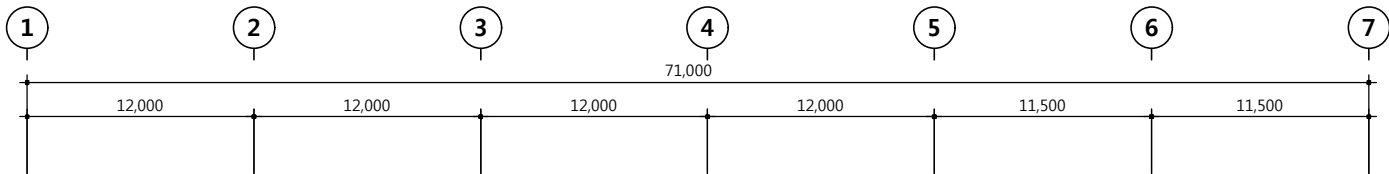

주기사항


- 배관 배선
—— : 슬라브 매입 배관 배선
- - - : 노출 배관 배선
— · — : 바닥 은폐 및 지중 매설 배관 배선
— · · — : CABLE TRAY내 배선
- 동력용 배관, 배선
—— : 16C (HFIX 2-2.5sq,E-2.5sq)
—— : 22C (HFIX 4-2.5sq,E-2.5sq)
- LEGEND
■ : 전등 전열용 분전반
□ : 비상용 분전반
■ : 동력용 분전반
⊙ : 복사히터 온도조절기용 J.B (전장속 설치)
⊙ : 전등 서킷 전원용 J.B (전장속 설치)
⊙_A : 자동문 전원용 J.B (전장속 설치)
⊙_B : 자동문 전원용 J.B (전장속 설치)
- PULL BOX SIZE
□_a : 150 x 150 x 100mm
□_b : 200 x 200 x 150mm
□_c : 300 x 300 x 200mm
□_d : 400 x 400 x 300mm
□_f : 500 x 500 x 300mm
- CABLE TRAY내 포설시 전선관을 제외한 CABLE만 포설한다.
- CABLE TRAY 및 노출배관의 지지행거는 1,500mm마다 설치한다.
- CABLE TRAY내 포설시 CV CABLE은 난연성 CABLE을 사용한다.
- 방화구획을 관통하는 부위에는 불연재의 방화재로 완전 방화구획이 되도록 차폐한다.
■ : 방화 구획 처리.
- 전기 배관이나 케이블 트레이, 버스 덕트 배관은 2.5m에 1개소씩 내진 면진체인가대 내진중형버팀대나 내진스프링행가를 설치 하는것을 기준으로 한다.
(내진설계 주기사항 및 상세도 참조)
- 간선 규격 및 기타 사항은 계통도 참조

실내기 / 환기유닛 전원 용량

장비 번호	전압 방식	용량 (KW)	장비 번호	전압 방식	용량 (KW)
23C IAC	1Ø 220V	0.02	83T IAC	1Ø 220V	0.053
32C IAC	1Ø 220V	0.02	100T IAC	1Ø 220V	0.069
52G IAC	1Ø 220V	0.02	130T IAC	1Ø 220V	0.097
52T IAC	1Ø 220V	0.025	130T IAC	1Ø 220V	0.97
60T IAC	1Ø 220V	0.03	290P IAC	1Ø 220V	0.40
72T IAC	1Ø 220V	0.047			
250 ERV	1Ø 220V	0.136	800 ERV	1Ø 220V	0.325
500 ERV	1Ø 220V	0.280	1000 ERV	1Ø 220V	0.454

- OUTLET BOX-리모콘 배관
—— E —— : 16C (EMPTY CONDUIT)
- 유선 리모콘 스위치 BOX (H:1,500mm)
가요전선관 시공 포함.
(결선,리모콘 스위치 설치는 업체 시공업자분)
- 냉,난방기기 및 환기유닛 전기설비공사 범위
- 실내기 전원선은 전기공사분임(배전반-실내기)
- 배전반~실내기 배관 배선은 전기공사분임
- 유선리모콘용 전선관 매립은 전기공사분임
- 냉,난방기기의 기계설비공사 범위
- 방진가대 공사는 냉난방업체 공사임
- 배관의 벽체관통 및 입상배관의 관통슬라브는 기계설비 공사임.

배수펌프 설치 상세도

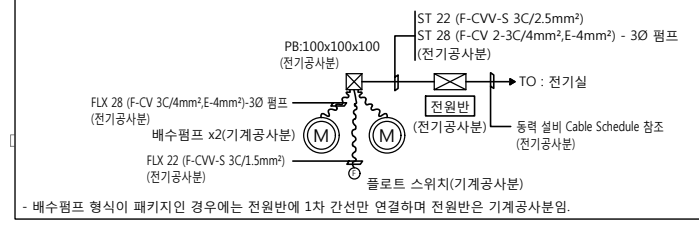

전력시설물종합설계업 제서울 E-1-055호
엔지니어링 활동주체 제06-378호
전기·정보통신 설계·감리 및 소방설계
JMM(주) 정명기술단
대표 · 기술사 이 정 환

PIT층 전력간선 및 동력 설비 평면도

축척:A1 : 1/200
A3 : 1/400

LS Electric
R-Center 구축

PROJECT TITLE

PROJECT NUMBER
224001

DESIGN CONSULTANT
가운 건축
GAUN | Architects & Engineers
서울시 강남구 연주로 609, 10층 (논현동, 파스타워)
Tel:82-2-3443-7799 Fax:82-2-3443-3807
www.gaun.co.kr

NOTES

KEY PLAN

NO. DESCRIPTION DATE

ISSUES & REVISIONS

BUILDING NAME

DRAWING TITLE
PIT층 전력간선 및 동력 설비 평면도

DRAWN
CHECK 1 안동식
CHECK 2 이은진
APPR 정용재

SCALE
A3 : 1/200
A3 : 1/400
DATE
2024.04

DRAWING NO.
EE-02-002