
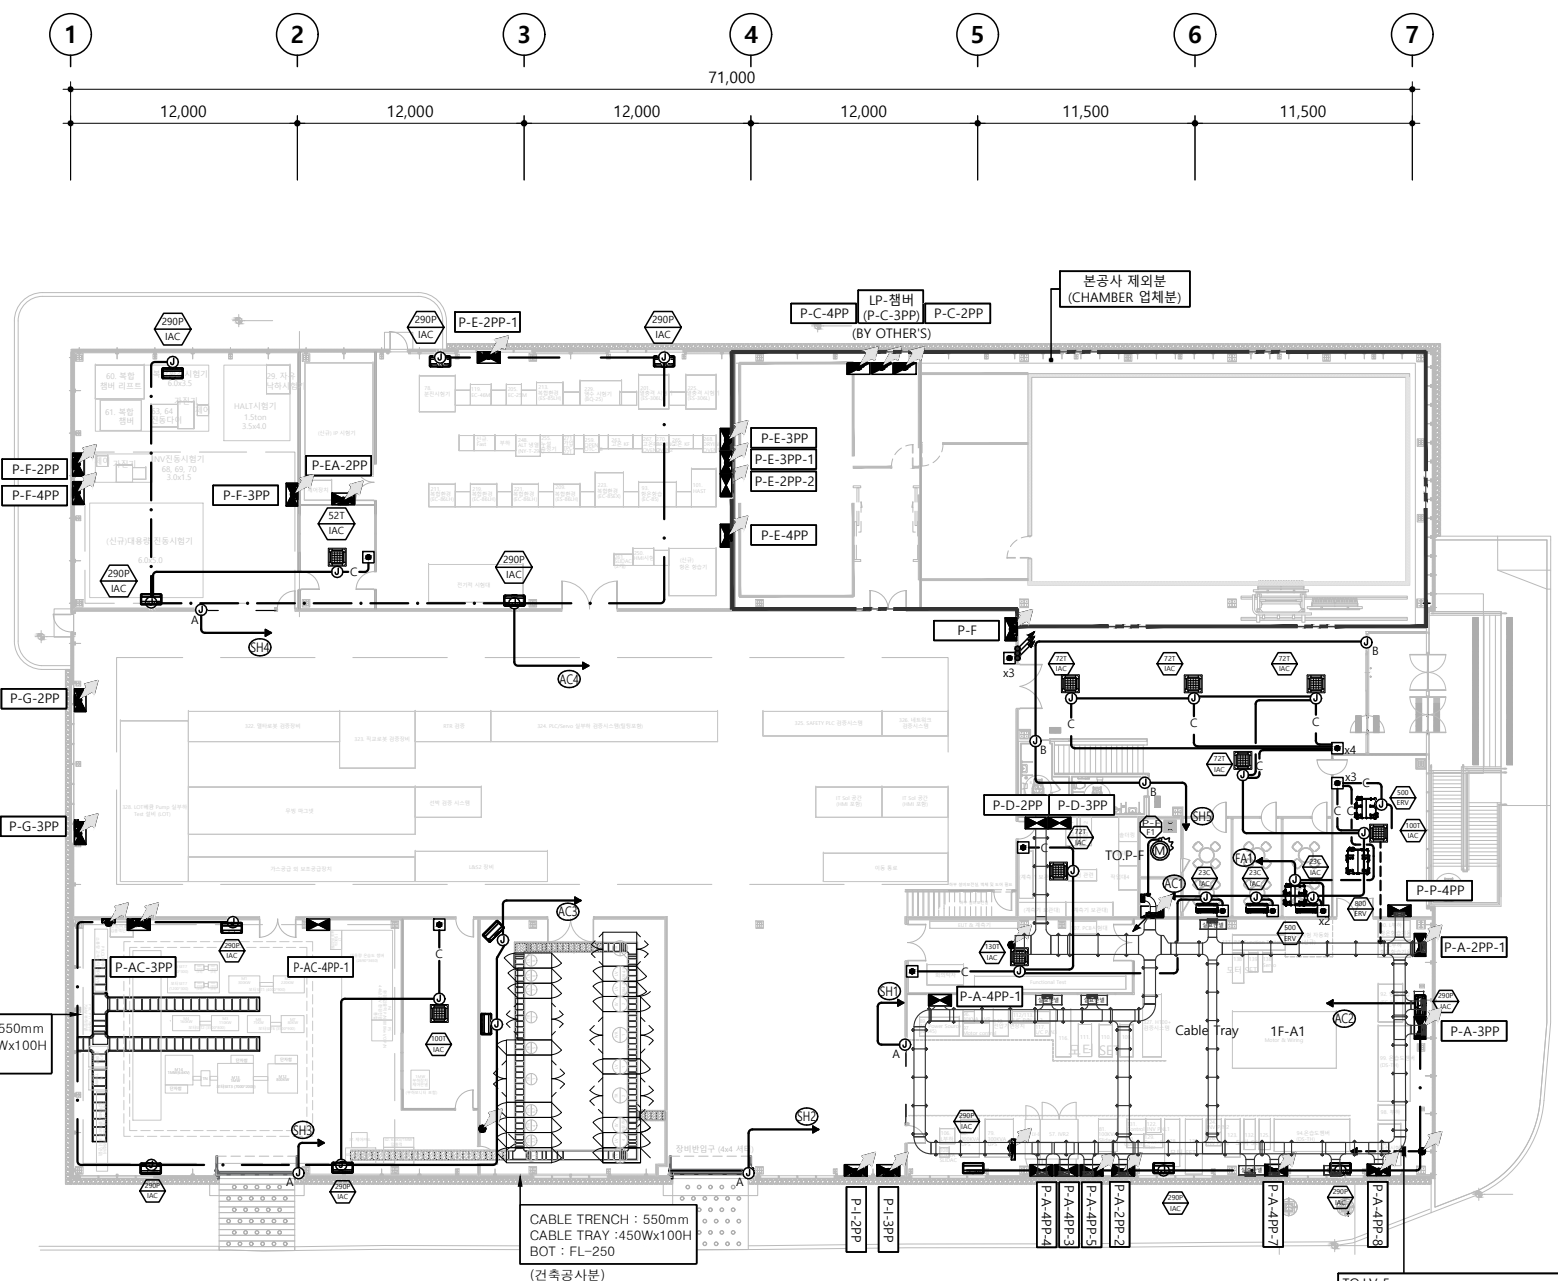


전력간선 설비 Cable Schedule		
From	To	CABLE SCHEDULE
LV-5	LV-R	F-CV 10sq * 3C (TRAY)
LV-7	P-F	F-CV 25sq * 4C (TRAY)
LV-5	P-C-4PP	F-CV 35sq * 1C * 3L (TRAY)
LV-5	P-P-4PP	F-CV 35sq * 1C * 3L (TRAY)
LV-3204-1	P-D-2PP	F-CV 35sq * 1C * 3L (TRAY)
LV-3204-1	P-EA-2PP	F-CV 35sq * 1C * 3L (TRAY)
LV-3204-2	P-C-2PP	F-CV 35sq * 1C * 3L (TRAY)
LV-8	P-AC-3PP	F-CV 35sq * 1C * 4L (TRAY)
LV-8	P-D-3PP	F-CV 35sq * 1C * 4L (TRAY)
LV-8	P-F-3PP	F-CV 35sq * 1C * 4L (TRAY)
LV-8	P-I-3PP	F-CV 35sq * 1C * 4L (TRAY)
LV-3204-2	P-I-2PP	F-CV 50sq * 1C * 3L (TRAY)
LV-4	P-E-4PP	F-CV 50sq * 1C * 3L (TRAY)
LV-7	LP-1F	F-CV 50sq * 1C * 4L (TRAY)
LV-3204-2	P-G-2PP	F-CV 70sq * 1C * 3L (TRAY)
LV-8	P-A-3PP	F-CV 120sq * 1C * 4L (TRAY)
LV-8	P-E-3PP	F-CV 120sq * 1C * 4L (TRAY)
LV-8	P-G-3PP	F-CV 120sq * 1C * 4L (TRAY)
LV-5	P-A-4PP-7	F-CV 150sq * 1C * 3L (TRAY)
LV-3204-2	P-F-2PP	F-CV 150sq * 1C * 3L (TRAY)
LV-3204-1	P-A-2PP-2	F-CV 185sq * 1C * 3L (TRAY)
LV-7	P-C-3PP	F-CV 185sq * 1C * 4L (TRAY)
LV-1	P-A-4PP-8	F-CV 240sq * 1C * 6L (TRAY)
LV-1	P-AC-4PP-1	F-CV 240sq * 1C * 3L (TRAY)
LV-4	P-A-4PP-1	F-CV 240sq * 1C * 6L (TRAY)
P-A-4PP-5	IVR-2	F-CV 240sq * 1C * 3L (TRAY)
LV-3204-1	P-A-2PP-1	F-CV 240sq * 1C * 3L (TRAY)
LV-3204-2	P-E-2PP-2	F-CV 240sq * 1C * 3L (TRAY)
LV-7	P-E-3PP-1	F-CV 240sq * 1C * 4L (TRAY)
LV-4	P-A-4PP-5	F-CV 300sq * 1C * 3L (TRAY)
LV-5	P-A-4PP-4	F-CV 300sq * 1C * 3L (TRAY)
LV-5	P-A-4PP-3	F-CV 300sq * 1C * 3L (TRAY)
LV-5	P-F-4PP	F-CV 300sq * 1C * 3L (TRAY)
LV-3204-2	P-E-2PP-1	F-CV 300sq * 1C * 3L (TRAY)

동력 설비 Cable Schedule					
PNL명	회로 번호	장비 번호	전압 방식	용량 (KW)	장비명
P-F	F1	2 SF	10 220V	0.214	SUPPLY FAN
					Cable & Conduit size
					28C (F-CV 2C/4sq, E-4sq)
					비고

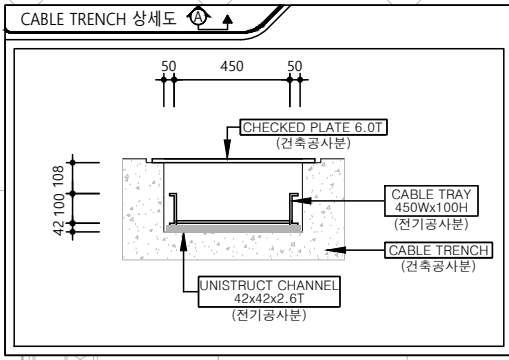

지상1층 전력간선 및 동력 설비 평면도
축척:A1 : 1/200
A3 : 1/400

- 주시사항
- 배관 배선
— : 슬라브 매입 배관 배선
- - : 노출 배관 배선
- . - : 바닥 은폐 및 지중 매설 배관 배선
- . . - : CABLE TRAY내 배선
 - 동력용 배관, 배선
— : 16C (HFIX 2-2.5sq.E-2.5sq)
- - - : 22C (HFIX 4-2.5sq.E-2.5sq)
 - LEGEND
[Symbol] : 전동 전열용 분전반
[Symbol] : 비상용 분전반
[Symbol] : 동력용 분전반
[Symbol] : 복사하터 온도조절기용 J.B (전장속 설치)
[Symbol] : 전동 서터 전원용 J.B (전장속 설치)
[Symbol] : 자동문 전원용 J.B (전장속 설치)
 - PULL BOX SIZE
[Symbol] : 150 x 150 x 100mm
[Symbol] : 200 x 200 x 150mm
[Symbol] : 300 x 300 x 200mm
[Symbol] : 400 x 400 x 300mm
[Symbol] : 500 x 500 x 300mm
 - CABLE TRAY내 포설시 전선관을 제외한 CABLE만 포설한다.
 - CABLE TRAY 및 노출배관의 지지행거는 1,500mm마다 설치한다.
 - CABLE TRAY내 포설시 CV CABLE은 난연성 CABLE을 사용한다.
 - 방화구획을 관통하는 부위에는 불연재의 방화재로 완전 방화구획이 되도록 차폐한다.
[Symbol] : 방화 구획 처리.
 - 전기 배관이나 케이블 트레이, 버스 덕트 배관은 2.5m에 1개소씩 내진 면진재인가대 내진중립버팀대나 내진스프링행거를 설치 하는것을 기준으로 한다.
(내진설계 주시사항 및 상세도 참조)
 - 간선 규격 및 기타 사항은 계통도 참조

실내기 / 환기유닛 전원 용량					
장비 번호	전압 방식	용량 (KW)	장비 번호	전압 방식	용량 (KW)
23C IAC	10 220V	0.02	83T IAC	10 220V	0.053
32C IAC	10 220V	0.02	100T IAC	10 220V	0.069
52G IAC	10 220V	0.02	130T IAC	10 220V	0.097
52T IAC	10 220V	0.025	130T IAC	10 220V	0.97
60T IAC	10 220V	0.03	290P IAC	10 220V	0.40
72T IAC	10 220V	0.047			
250 ERV	10 220V	0.136	800 ERV	10 220V	0.325
500 ERV	10 220V	0.280	1000 ERV	10 220V	0.454

- OUTLET BOX-리모콘 배관
— E — : 16C (EMPTY CONDUIT)
- 유선 리모콘 스위치 BOX (H:1,500mm)
가요전선관 시공 포함.
(결선, 리모콘 스위치 설치는 업체 시공업자분)
- 냉,난방기기 및 환기유닛 전기설비공사 범위
- 실내기 전원선은 전기공사분임(배전반-실내기)
- 배전반~실내기 배관, 배선은 전기공사분임
- 유선리모콘용 전선관 매립은 전기공사분임
- 냉,난방기기의 기계설비공사 범위
- 방진가드 공사는 냉난방업체 공사임
- 배관의 벽체관통 및 입상배관의 관통슬리브는 기계설비 공사임.

전력시설물중합설계업 제서울 E-1-055호
엔지니어링 활동주체 제06-378호
전기,정보통신,설계,감리 및 소방설계
JM(주) 정명기술단
대표: 기술사 이 정 환

LS Electric
R-Center 구축

PROJECT TITLE
224001

DESIGN CONSULTANT
가운 건축
GAUN I Architects & Engineers

서울시 강남구 연주로 609, 10층 (논현동, 파스타워)
Tel:82-2-3443-7799 Fax:82-2-3443-3807
www.gau.co.kr

NOTES

KEY PLAN

NO. DESCRIPTION DATE

ISSUES & REVISIONS

BUILDING NAME

DRAWING TITLE
지상1층 전력간선
및 동력 설비 평면도

DRAWN 안동식
CHECK 1 이은진
CHECK 2 정용재
APPR 정용재

SCALE
A3 : 1/200
A3 : 1/400
DATE
2024.04

DRAWING NO.
EE-02-003