
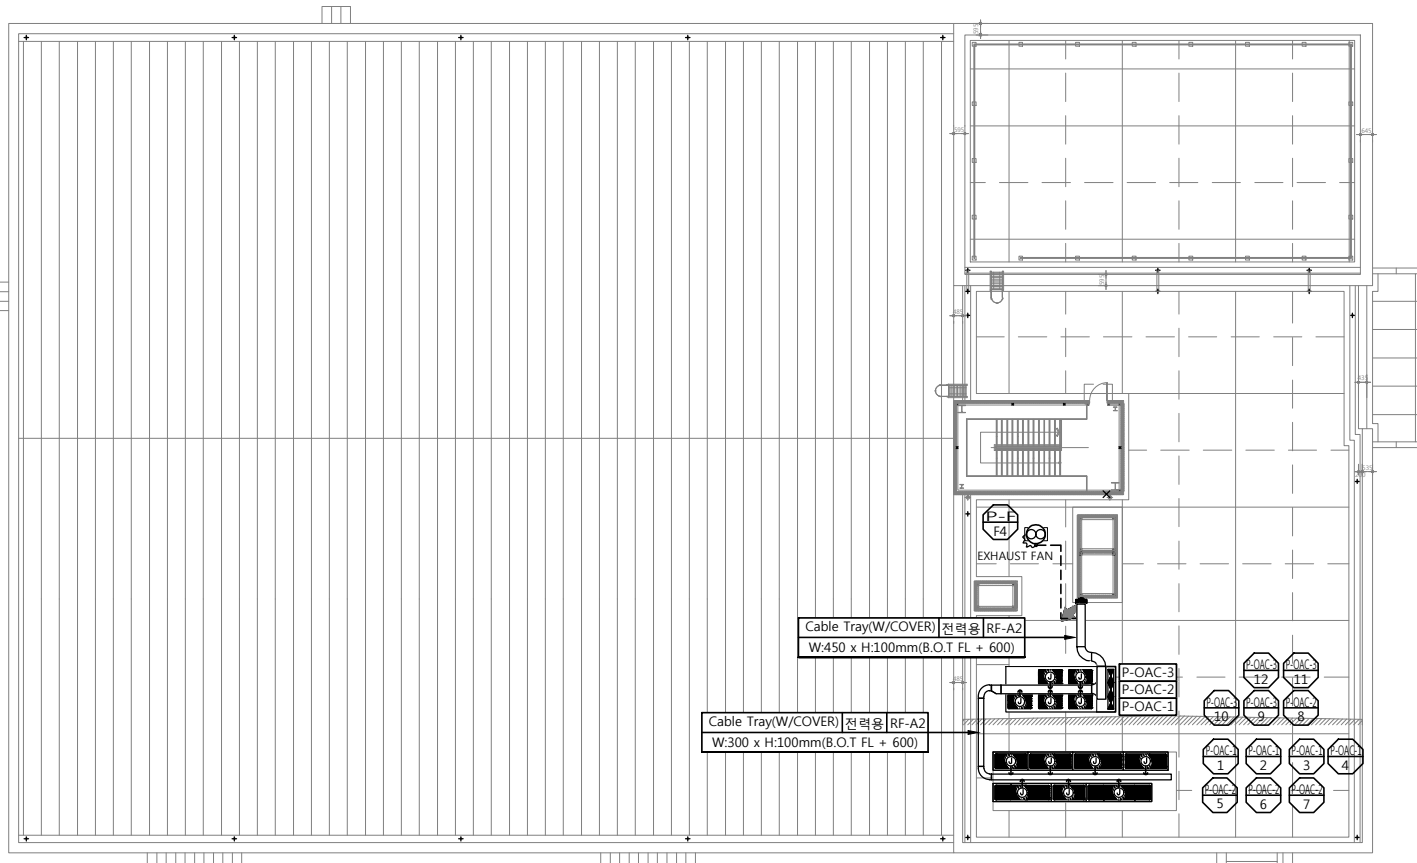
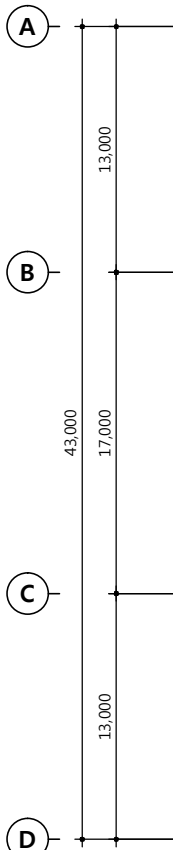


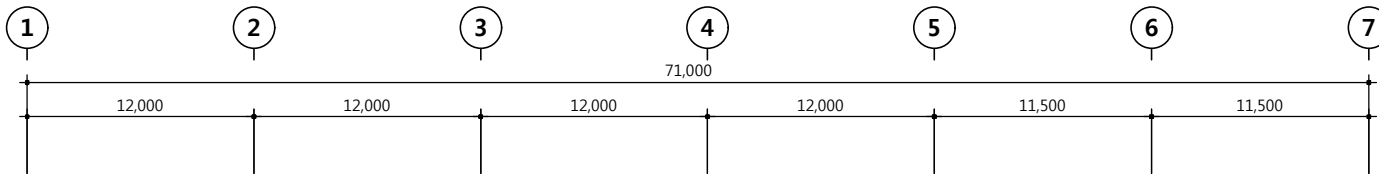

동력 설비 Cable Schedule						
PNL명	회로번호	장비번호	전압방식	용량(KW)	장비명	Cable & Conduit size
P-OAC-1	1	22 OAC	3Ø 4W 380/220V	25.3	시스템에어컨 실외기	42C (F-CV 4C/16sq, E-16sq)
	2	30 OAC	3Ø 4W 380/220V	42.2	시스템에어컨 실외기	70C (F-CV 4C/35sq, E-16sq)
	3	34 OAC	3Ø 4W 380/220V	46.4	시스템에어컨 실외기	70C (F-CV 4C/35sq, E-16sq)
	4	32 OAC	3Ø 4W 380/220V	21.7	시스템에어컨 실외기	42C (F-CV 4C/10sq, E-10sq)
P-OAC-2	5	42 OAC	3Ø 4W 380/220V	53.5	시스템에어컨 실외기	70C (F-CV 1C-4/50sq, E-25sq)
	6	24 OAC	3Ø 4W 380/220V	29.0	시스템에어컨 실외기	54C (F-CV 4C/25sq, E-16sq)
	7	48 OAC	3Ø 4W 380/220V	58.0	시스템에어컨 실외기	70C (F-CV 1C-4/50sq, E-25sq)
	8	1 ODU	3Ø 4W 380/220V	28.2	EHP 실외기	42C (F-CV 4C/10sq, E-10sq)
P-OAC-3	9	1 ODU	3Ø 4W 380/220V	28.2	EHP 실외기	42C (F-CV 4C/10sq, E-10sq)
	10	1 ODU	3Ø 4W 380/220V	28.2	EHP 실외기	42C (F-CV 4C/10sq, E-10sq)
	11	1 ODU	3Ø 4W 380/220V	28.2	EHP 실외기	42C (F-CV 4C/10sq, E-10sq)
	12	1 ODU	3Ø 4W 380/220V	28.2	EHP 실외기	42C (F-CV 4C/10sq, E-10sq)
P-F	P-F F4	1 TEF	1Ø 220V	0.4	EXHAUST FAN	28C (F-CV 2C/4sq, E-4sq)

전력간선 설비 Cable Schedule		
From	To	CABLE SCHEDULE
LV-7	P-OAC-3	F-CV 120sq * 1C *4L (TRAY)
LV-7	P-OAC-1	F-CV 150sq * 1C *4L (TRAY)
LV-8	P-OAC-2	F-CV 240sq * 1C *4L (TRAY)

지붕층 전력간선 및 동력 설비 평면도

축척:A1 : 1/200
A3 : 1/400

주기사항

- 배관 배선
— : 슬라브 매입 배관 배선
- - : 노출 배관 배선
- · - : 바닥 은폐 및 지중 매설 배관 배선
- · · - : CABLE TRAY내 배선
- 동력용 배관, 배선
— : 16C (HFIX 2-2.5sq,E-2.5sq)
- - - : 22C (HFIX 4-2.5sq,E-2.5sq)
- LEGEND
■ : 전동 전열용 분전반
□ : 비상용 분전반
■ : 동력용 분전반
⊙ : 복사히터 온도조절기용 J.B (전장속 설치)
⊙ : 천동 서타 전열용 J.B (전장속 설치)
⊙_A : 자동문 전열용 J.B (전장속 설치)
⊙_B : 자동문 전열용 J.B (전장속 설치)
- PULL BOX SIZE
□_a : 150 x 150 x 100mm
□_b : 200 x 200 x 150mm
□_c : 300 x 300 x 200mm
□_d : 400 x 400 x 300mm
□_f : 500 x 500 x 300mm
- CABLE TRAY내 포설시 전선관을 제외한 CABLE만 포설한다.
- CABLE TRAY 및 노출배관의 지지행거는 1,500mm마다 설치한다.
- CABLE TRAY내 포설시 CV CABLE은 난연성 CABLE을 사용한다.
- 방화구획을 관통하는 부위에는 불연재의 방화재로 완전 방화구획이 되도록 차폐한다.
■ : 방화 구획 처리.
- 전기 배관이나 케이블 트레이, 부스 덕트 배관은 2.5m에 1개소씩 내진 면진체인가대 내진중형버팀대나 내진스프링행가를 설치 하는것을 기준으로 한다.
(내진설계 주기사항 및 상세도 참조)
- 간선 규격 및 기타 사항은 계통도 참조

실내기 / 환기유닛 전열 용량

장비번호	전압방식	용량(KW)	장비번호	전압방식	용량(KW)
23C IAC	1Ø 220V	0.02	83T IAC	1Ø 220V	0.053
32C IAC	1Ø 220V	0.02	100T IAC	1Ø 220V	0.069
52G IAC	1Ø 220V	0.02	130T IAC	1Ø 220V	0.097
52T IAC	1Ø 220V	0.025	130T IAC	1Ø 220V	0.97
60T IAC	1Ø 220V	0.03	290P IAC	1Ø 220V	0.40
72T IAC	1Ø 220V	0.047			
250 ERV	1Ø 220V	0.136	800 ERV	1Ø 220V	0.325
500 ERV	1Ø 220V	0.280	1000 ERV	1Ø 220V	0.454

- OUTLET BOX-리모콘 배관
— E — : 16C (EMPTY CONDUIT)
- 유선 리모콘 스위치 BOX (H:1,500mm)
가요전선관 시공 포함.
(결선,리모콘 스위치 설치는 업체 시공업자분)
- 냉,난방기기 및 환기유닛 전기설비공사 범위
- 실내기 전열선은 전기공사분임(배전반-실내기)
- 배전반~실외기 배관 배선은 전기공사분임
- 유선리모콘용 전선관 매립은 전기공사분임
- 냉,난방기기의 기계설비공사 범위
- 방진가대 공사는 냉난방업체 공사임
- 배관의 벽체관통 및 입상배관의 관통슬리브는 기계설비 공사임.

전력시설물종합설계업 제서울 E-1-055호
엔지니어링 활동주체 제06-378호
전기·정보통신 설계·감리 및 소방설계
JMM(주) 정명기술단
대표·기술사 이 정 환

PROJECT TITLE

LS Electric
R-Center 구축

PROJECT NUMBER

224001

DESIGN CONSULTANT

가운 건축

GAUN | Architects & Engineers

서울시 강남구 연주로 609, 10층 (논현동, 파스타워)
Tel:82-2-3443-7799 Fax:82-2-3443-3807
www.gaun.co.kr

NOTES

KEY PLAN		
△		
△		
△		
△		
△		
△		
△		
△		
△		
△		
NO.	DESCRIPTION	DATE

ISSUES & REVISIONS		
BUILDING NAME		
DRAWING TITLE		
지붕층 전력간선 및 동력 설비 평면도		
DRAWN	CHECK 1	SCALE
	안 동 식	A3 : 1/200 A3 : 1/400
	CHECK 2	DATE
	이 은 진	2024.04
APPR	정 용 재	
DRAWING NO.		
EE-02-005		