


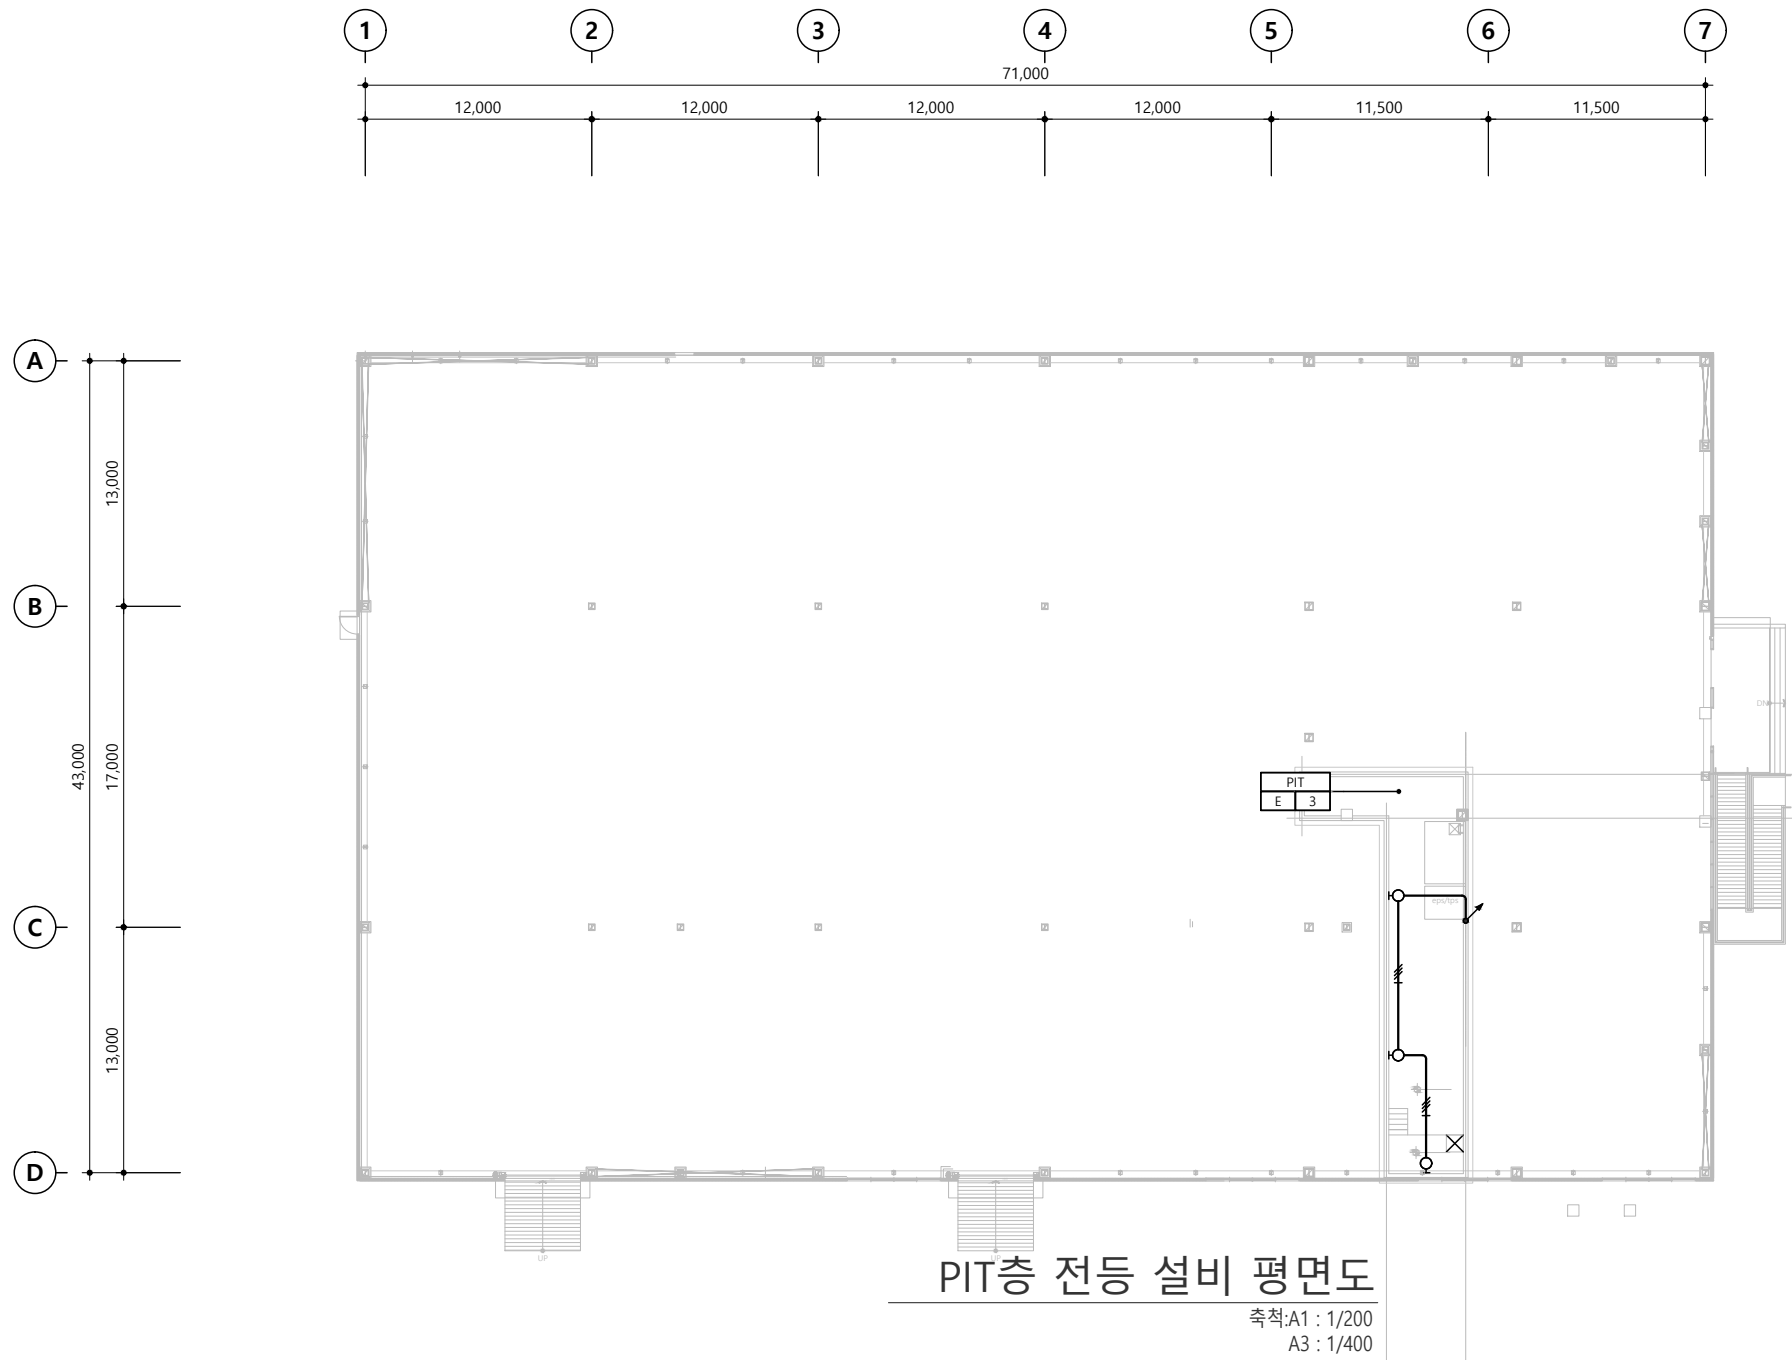

NOTE

1. 배관 배선

—

: 슬라브 매입 배관 배선

—

: 노출 배관 배선

—

: 바닥 은폐 및 지중 매설 배관 배선

—

: CABLE TRAY내 배선

2. 전등용 배관, 배선

—

: 16C (HFIX 2-2.5sq.E-2.5sq)

—

: 16C (HFIX 3-2.5sq.E-2.5sq)

—

: 22C (HFIX 4-2.5sq.E-2.5sq)

—

: 22C (HFIX 5-2.5sq.E-2.5sq)

—

: 22C (HFIX 6-2.5sq.E-2.5sq)

—

: 28C (HFIX 7-2.5sq.E-2.5sq)

—

: 28C (HFIX 8-2.5sq.E-2.5sq)

3. 전등 스위치용 배관, 배선

—

: 16C (HFIX 2-2.5sq)

—

: 16C (HFIX 3-2.5sq)

—

: 22C (HFIX 4-2.5sq)

—

: 22C (HFIX 5-2.5sq)

—

: 22C (HFIX 6-2.5sq)

4. 일괄소등 스위치

☒

: 일괄소등 스위치 (모듈내장)H:1,200

일괄소등 스위치는 "전기용품 안전관리법" 제5조 안전인증을 취득한 제품을 사용한다

조명기구 LEGEND

SYMBOL	TYPE	조명기구 상세도	비 고
	LED 40W (RACE-WAY)	"A"	
	LED 40W (매입등)	"B"	
	LED 40W (직부등)	"C"	
	LED 15W (다운라이트)	"D"	
	LED 20W (직부등)	"E"	
	LED 12W (광벽부등)	"F"	
	LED 4W (다운라이트)	"G"	
	LED 20W (벽부등)	"H"	
	LED 15W (투사등)	"I"	
	마이크로파 동작감지센서 자동스위치		

전력시설물종합설계업 제서울 E-1-055호
엔지니어링 활동주체 제06-378호
전기 정보통신 설계 감리 및 소방설계
JM(주) 정명기술단
대표·기술사 이 정 환

PROJECT TITLE

LS

LS Electric

R-Center 구축

PROJECT NUMBER

224001

DESIGN CONSULTANT

가운건축

GAUN | Architects & Engineers

서울시 강남구 연주로 609, 10층 (논현동, 박스타워)
Tel:82-2-3443-7799 Fax:82-2-3443-3807
www.g aun.co.kr

NOTES

KEY PLAN

△

△

△

△

△

△

△

△

△

NO.	DESCRIPTION	DATE
ISSUES & REVISIONS		
BUILDING NAME		
DRAWING TITLE		
PIT층 전등 설비 평면도		
DRAWN	SCALE	
CHECK 1 안 동 식	A3 : 1/200	
CHECK 2 이 은 진	A3 : 1/400	
APPR 정 용 재	DATE	2024.04
DRAWING NO.		
EE-03-002		