

NOTE

1. 배관 배선
- : 슬라브 매입 배관 배선
 - : 노출 배관 배선
 - : 바닥 온패 및 지중 매설 배관 배선
 - : CABLE TRAY내 배선
2. 전등용 배관, 배선
- : 16C (HFIX 2-2.5sq.E-2.5sq)
 - : 16C (HFIX 3-2.5sq.E-2.5sq)
 - : 22C (HFIX 4-2.5sq.E-2.5sq)
 - : 22C (HFIX 5-2.5sq.E-2.5sq)
 - : 22C (HFIX 6-2.5sq.E-2.5sq)
 - : 28C (HFIX 7-2.5sq.E-2.5sq)
 - : 28C (HFIX 8-2.5sq.E-2.5sq)
3. 전등 스위치용 배관, 배선
- : 16C (HFIX 2-2.5sq)
 - : 16C (HFIX 3-2.5sq)
 - : 22C (HFIX 4-2.5sq)
 - : 22C (HFIX 5-2.5sq)
 - : 22C (HFIX 6-2.5sq)
4. 일괄소등 스위치
- ☑ 일괄소등 스위치 (모듈내장)H:1,200
- 일괄소등 스위치는 "전기용품 안전관리법" 제5조 안전인증을 취득한 제품을 사용한다

조명기구 LEGEND

SYMBOL	TYPE	조명기구 상세도	비 고
	LED 40W (RACE-WAY)	"A"	
	LED 40W (매입등)	"B"	
	LED 40W (직부등)	"C"	
	LED 15W (다운라이트)	"D"	
	LED 20W (직부등)	"E"	
	LED 12W (광벽부등)	"F"	
	LED 4W (다운라이트)	"G"	
	LED 20W (벽부등)	"H"	
	LED 15W (투사등)	"I"	
	투광등	"J"	
	마이크로파 동작감지센서 자동스위치		


NO.	DESCRIPTION	DATE
-----	-------------	------

ISSUES & REVISIONS

지상1층 전등 설비 평면도

DRAWN	SCALE
CHECK 1 안 동 식	A3 : 1/200 A3 : 1/400
CHECK 2 이 은 진	DATE 2024.04
APPR 정 용 재	

EE-03-003

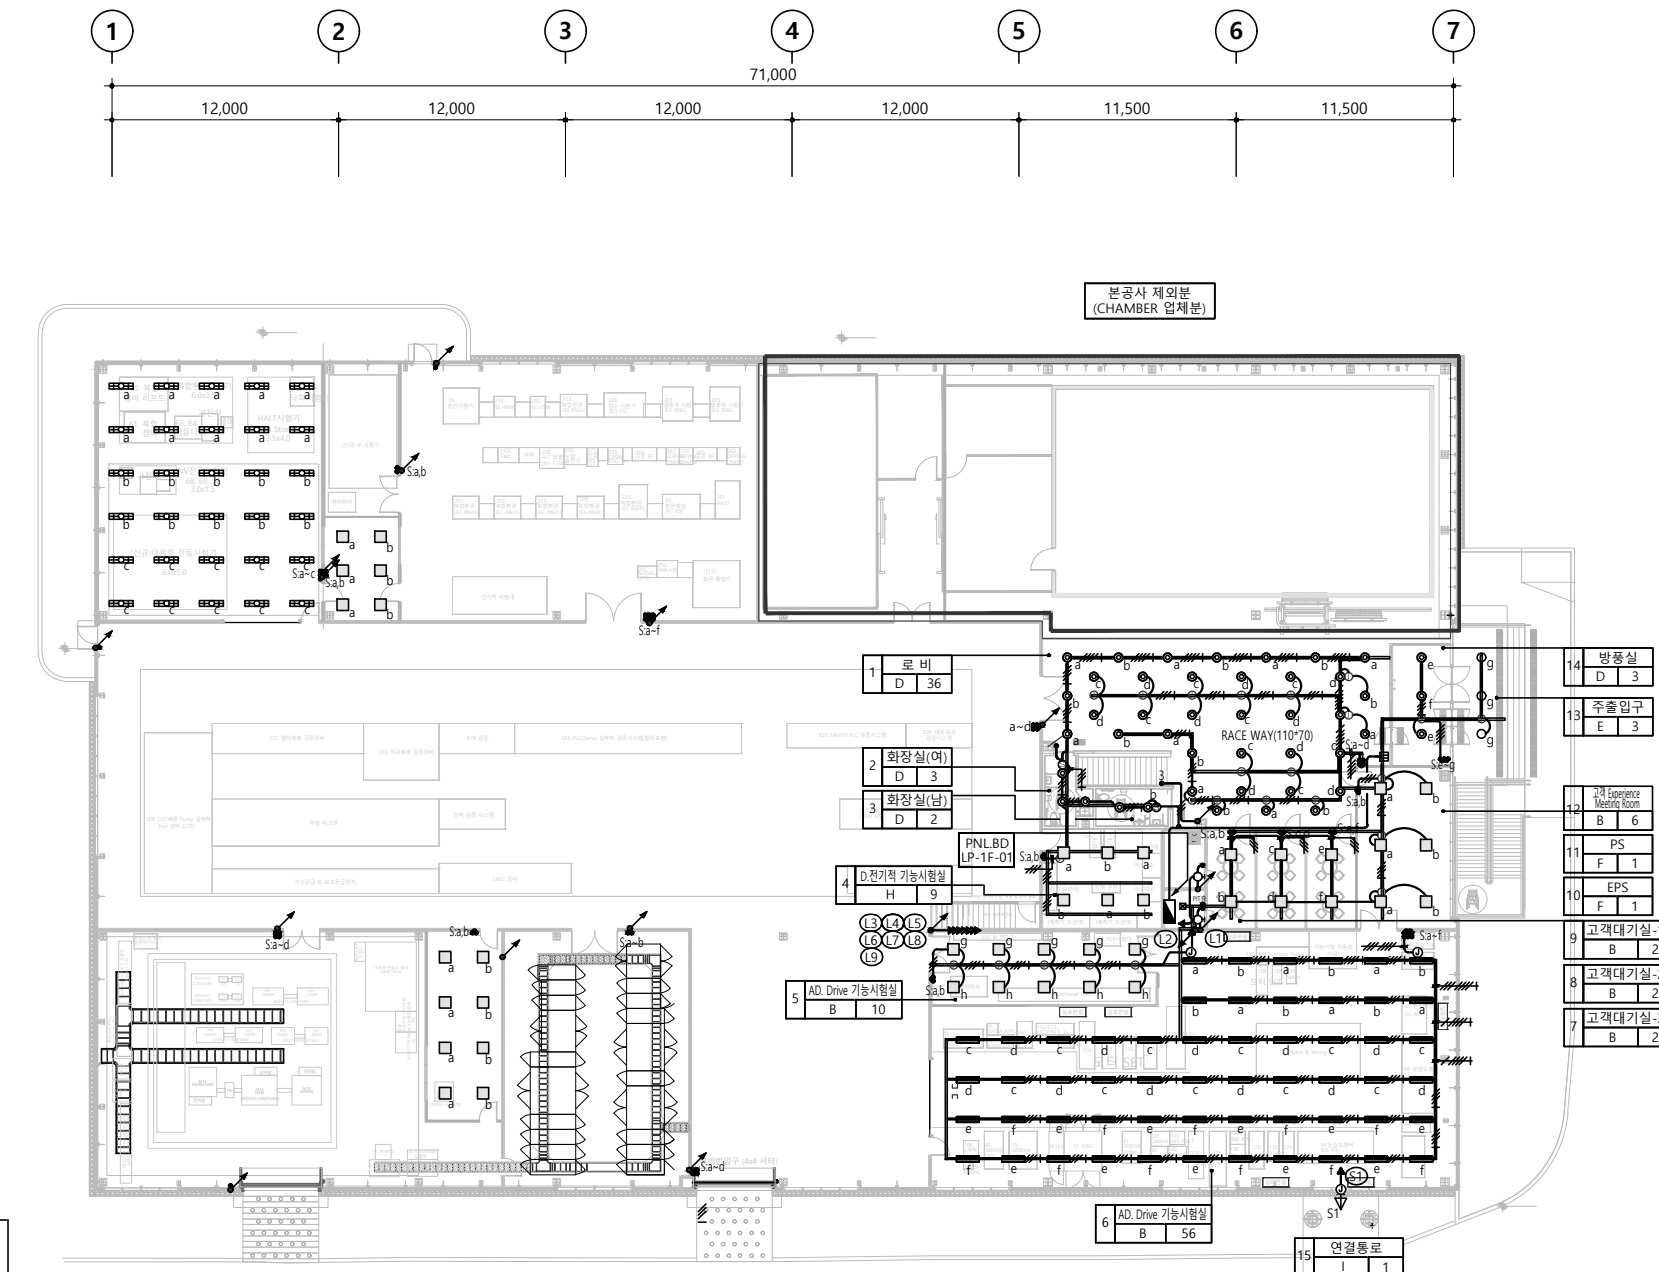

지상1층 전등 설비 평면도

축척:A1 : 1/200
A3 : 1/400

■ 조명기구 TYPE 및 수량(지상1층)

	실명	TYPE	EA
①	로비	D	36
②	화장실(여)	D	3
③	화장실(남)	D	2
④	D.전기적 기능 시험실	B	6
⑤	AD.DRIVE 기능 시험실(방음)	B	10
⑥	AD.DRIVE 기능 시험실	B	56
⑦	고객 대기실-1	B	2
⑧	고객대기실-2	B	2
⑨	고객대기실-3	B	2
⑩	EPS	F	1
⑪	PS	F	1
⑫	고객 Experience Meeting Room	B	6
⑬	주출입구	E	3
⑭	방풍실	D	3
⑮	연결통로	I	1

전력시설물종합설계업 제서울 E-1-055호
엔지니어링 활동주체 제06-378호
전기 정보통신 설계.감리 및 소방설계
JM(주) 정 명 기 술 단
대표 · 기술사 이 정 환