


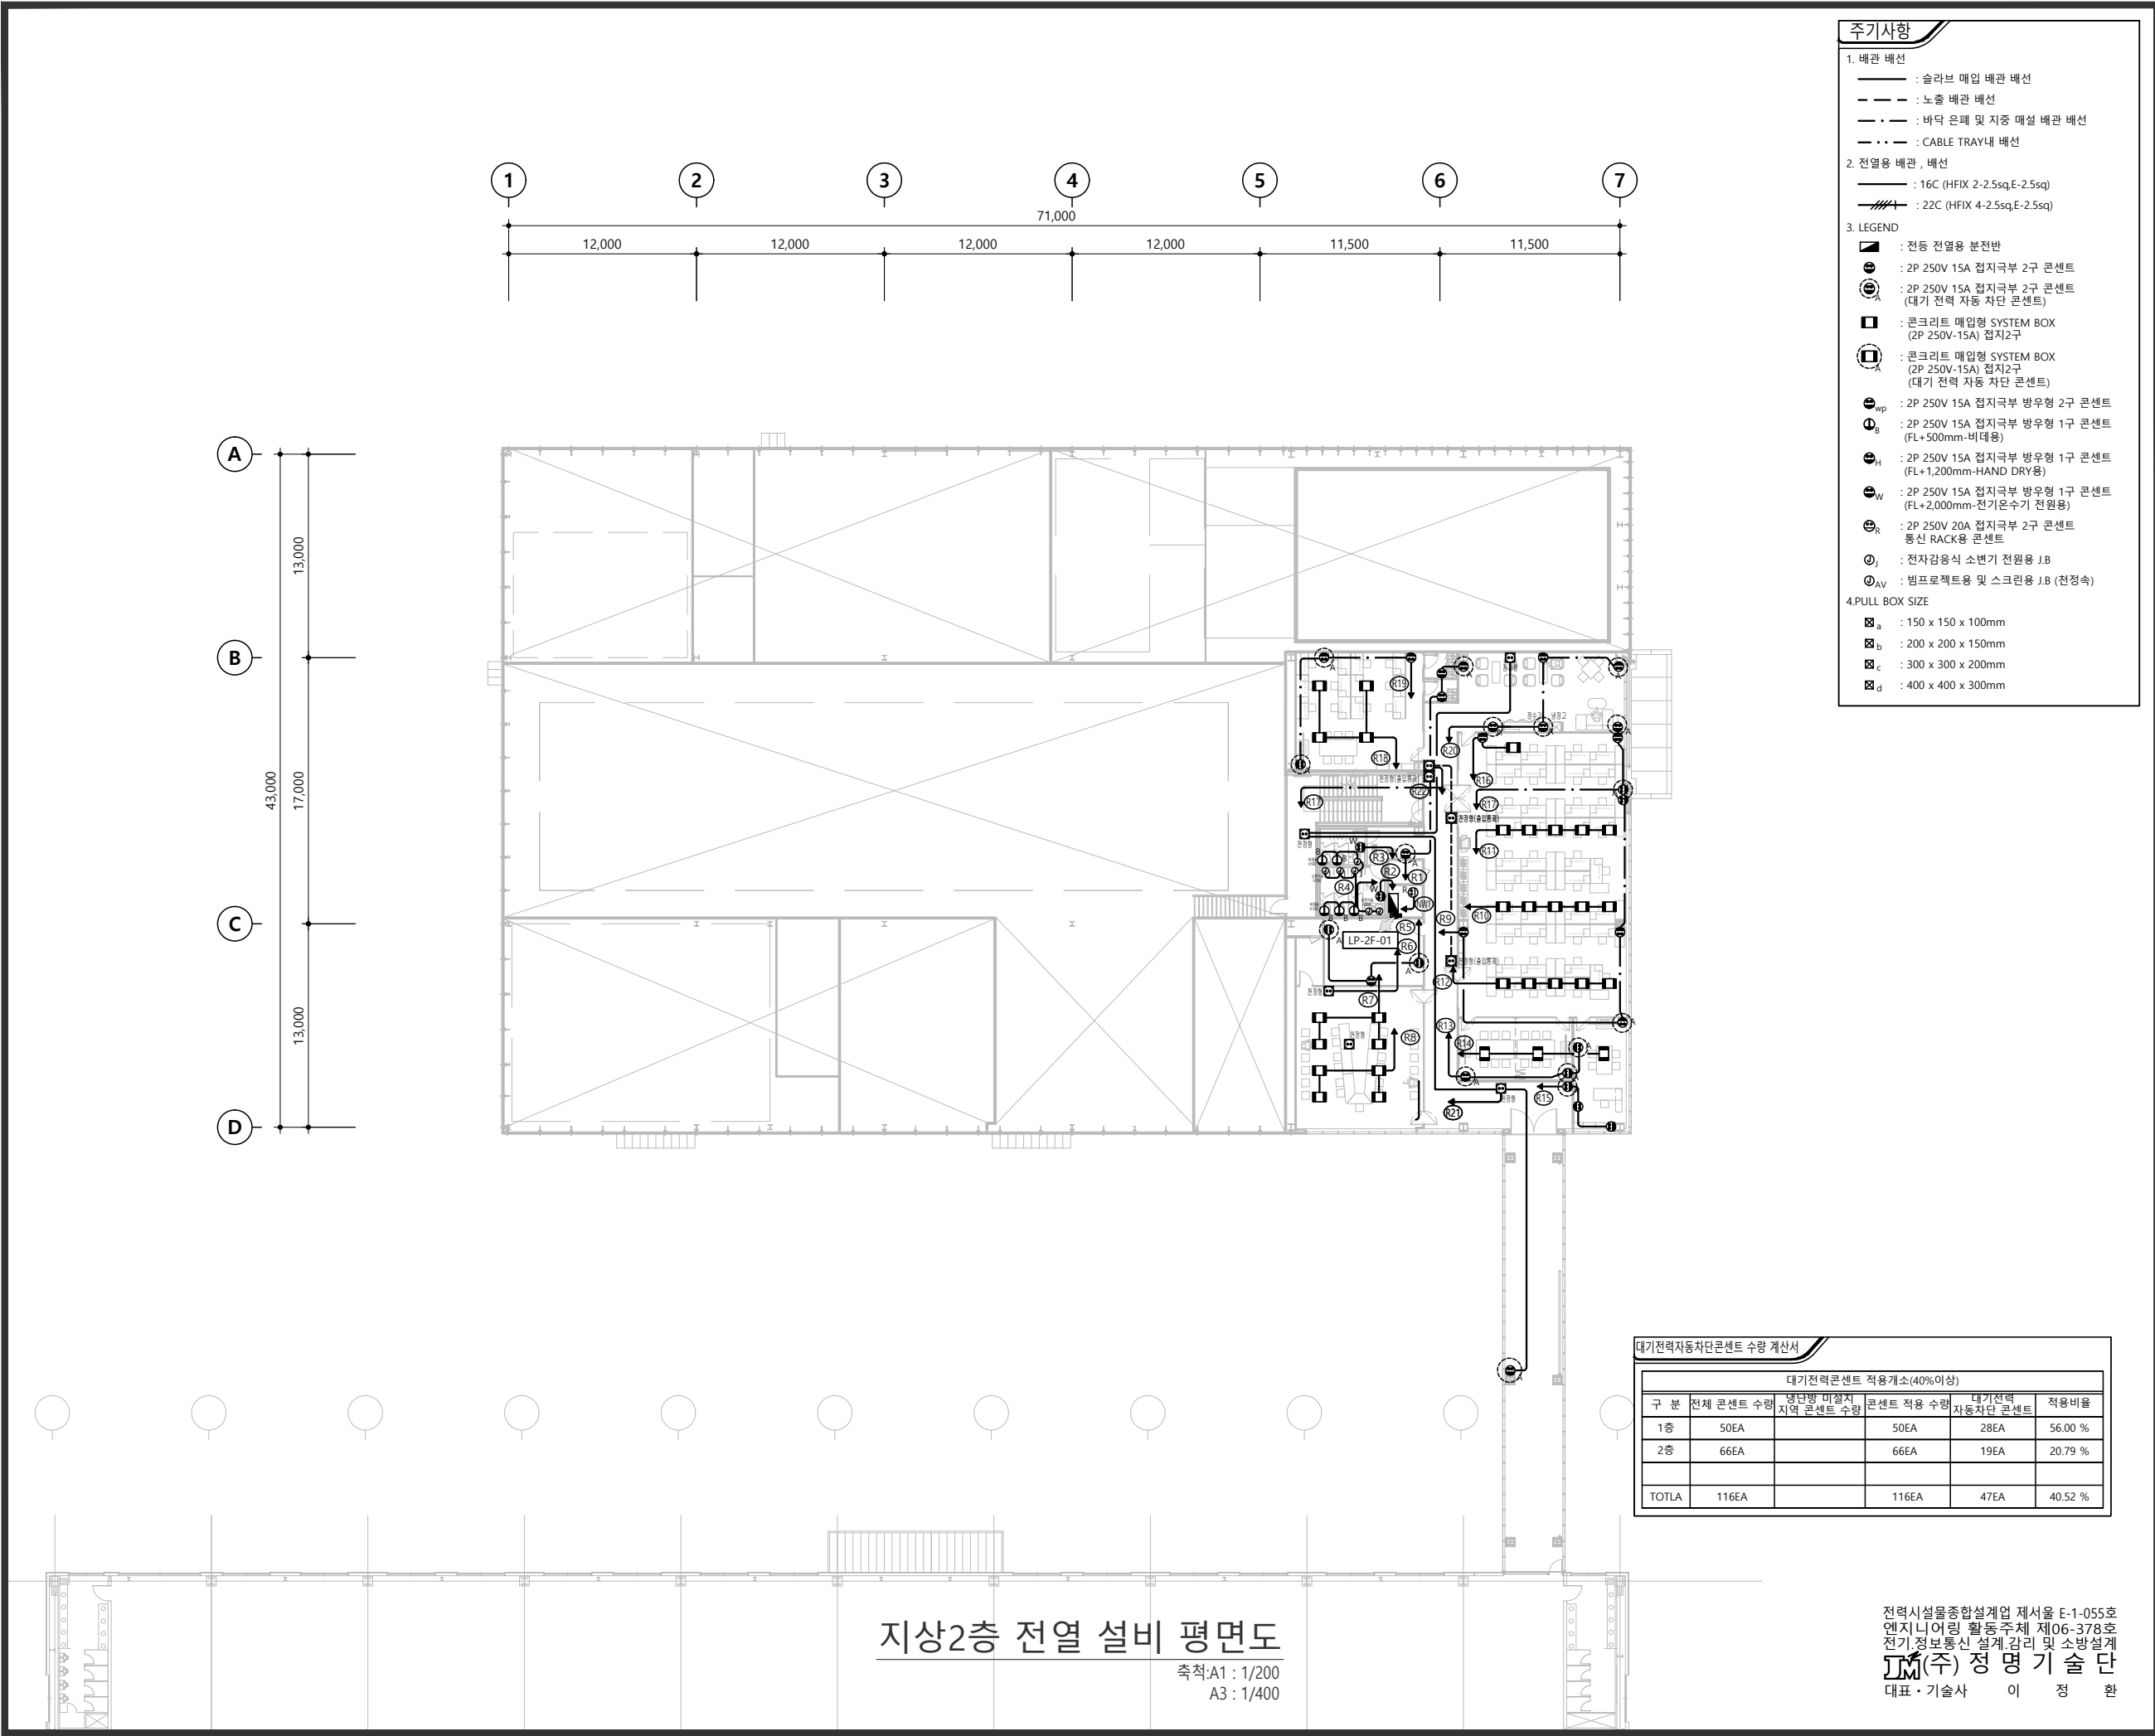

주기사항

1. 배관 배선
— : 슬라브 매입 배관 배선
- - : 노출 배관 배선
- · - : 바닥 은폐 및 지중 매설 배관 배선
- · · - : CABLE TRAY내 배선

2. 전열용 배관, 배선
— : 16C (HFIX 2-2.5sq,E-2.5sq)
- - - : 22C (HFIX 4-2.5sq,E-2.5sq)

3. LEGEND
☐ : 전등 전열용 분전반
⊙ : 2P 250V 15A 접지극부 2구 콘센트
⊙ : 2P 250V 15A 접지극부 2구 콘센트 (대기 전력 자동 차단 콘센트)
☐ : 콘크리트 매입형 SYSTEM BOX (2P 250V-15A) 접지2구
⊙ : 콘크리트 매입형 SYSTEM BOX (2P 250V-15A) 접지2구 (대기 전력 자동 차단 콘센트)
⊙_{WP} : 2P 250V 15A 접지극부 방우형 2구 콘센트
⊙_B : 2P 250V 15A 접지극부 방우형 1구 콘센트 (FL+500mm-비대용)
⊙_H : 2P 250V 15A 접지극부 방우형 1구 콘센트 (FL+1,200mm-HAND DRY용)
⊙_W : 2P 250V 15A 접지극부 방우형 1구 콘센트 (FL+2,000mm-전기온수기 전용용)
⊙_R : 2P 250V 20A 접지극부 2구 콘센트 통신 RACK용 콘센트
⊙_J : 전자감응식 소변기 전원용 J.B
⊙_{AV} : 빔프로젝트용 및 스크린용 J.B (천정속)

4.PULL BOX SIZE
☐_a : 150 x 150 x 100mm
☐_b : 200 x 200 x 150mm
☐_c : 300 x 300 x 200mm
☐_d : 400 x 400 x 300mm

대기전력자동차단콘센트 수량 계산서

대기전력콘센트 적용개소(40%이상)				
구 분	전체 콘센트 수량	명단별 미설치 지역 콘센트 수량	콘센트 적용 수량	대기전력 자동차단 콘센트 적용비율
1층	50EA		50EA	56.00 %
2층	66EA		66EA	19.79 %
TOTLA	116EA		116EA	40.52 %

지상2층 전열 설비 평면도

축척:A1 : 1/200
A3 : 1/400

전력시설물종합설계업 제서울 E-1-055호
엔지니어링 활동주체 제06-378호
전기·정보통신 설계·감리 및 소방설계
JM(주) 정명기술단
대표·기술사 이 정 환

PROJECT TITLE

LS

LS Electric

R-Center 구축

PROJECT NUMBER

224001

DESIGN CONSULTANT

가운 건축

GAUN | Architects & Engineers

서울시 강남구 연주로 609, 10층 (논현동, 파크타워)
Tel.82-2-3443-7799 Fax.82-2-3443-3807
www.gaun.co.kr

NOTES

KEY PLAN

△		
△		
△		
△		
△		
△		
△		
△		
NO.	DESCRIPTION	DATE

ISSUES & REVISIONS

BUILDING NAME

DRAWING TITLE

지상2층 전열 설비 평면도

DRAWN	SCALE
CHECK 1 안동식	A3 : 1/200 A3 : 1/400
CHECK 2 이은진	DATE
APPR 정용재	2024.04

DRAWING NO.

EE-04-002