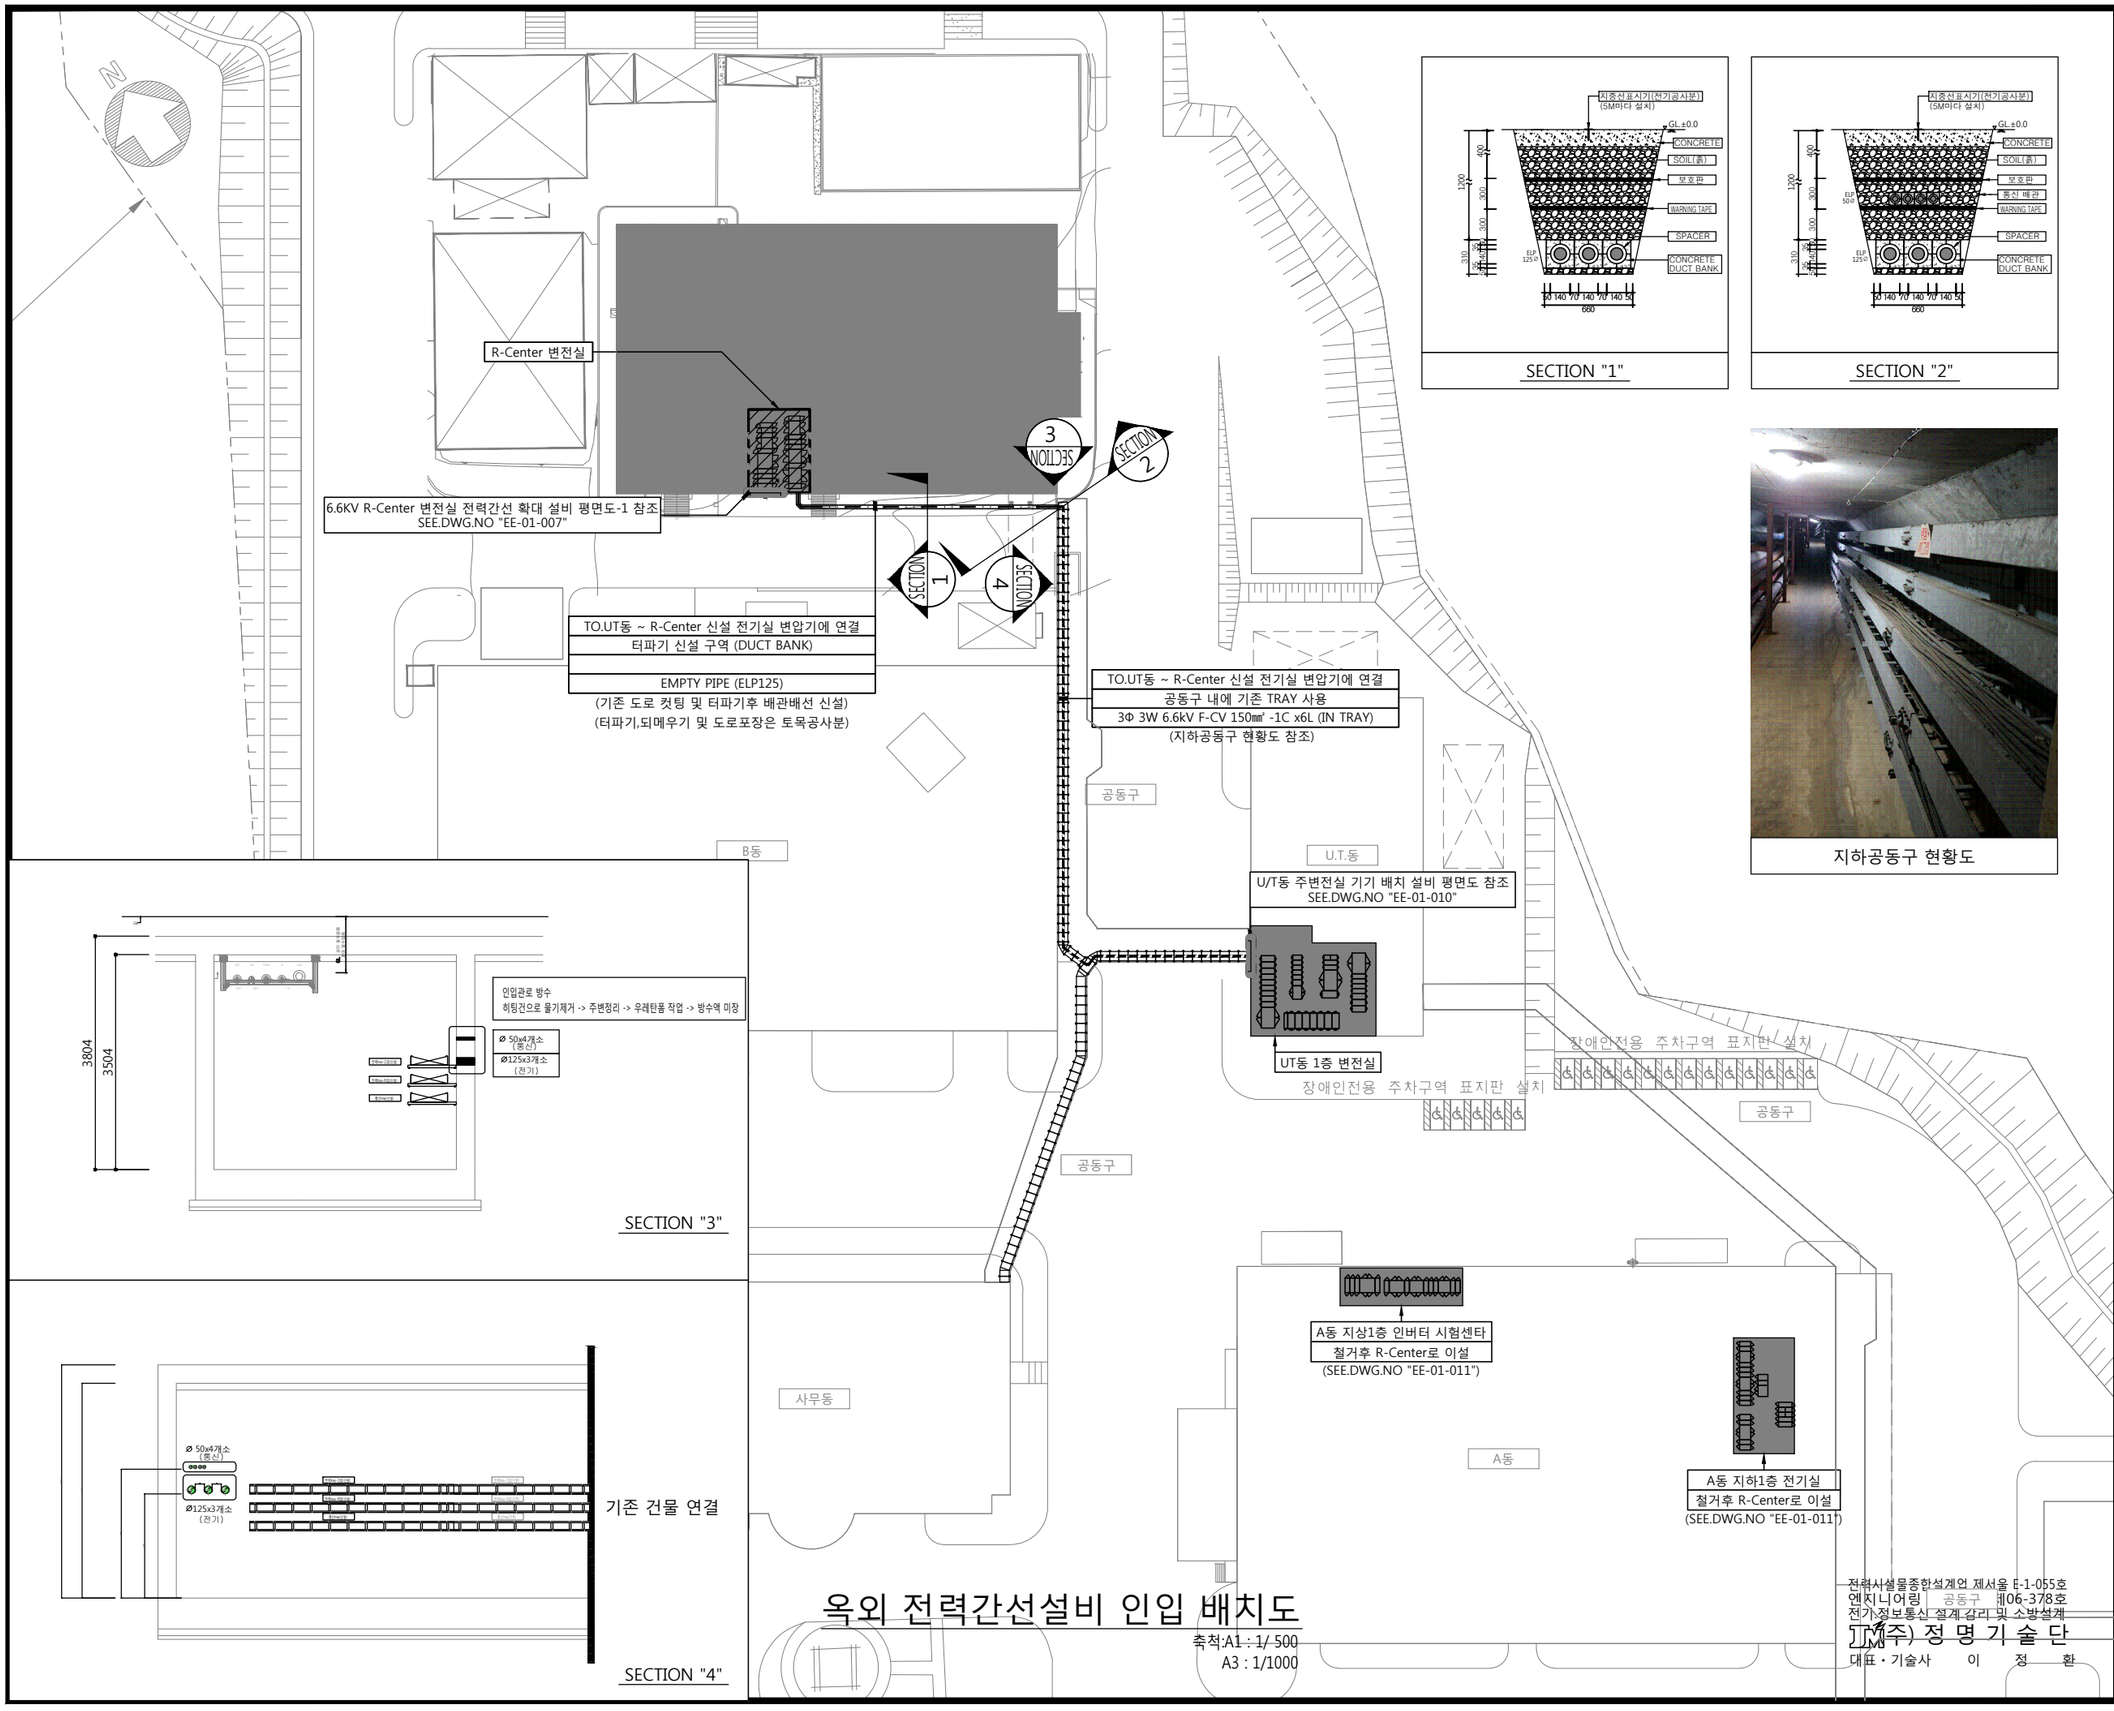


SECTION "1"

SECTION "2"

지하공동구 현황도

옥외 전력간선설비 인입 배치도

축척:A1 : 1/ 500
A3 : 1/1000

전력시설물종합설계업 제서울 E-1-055호
엔지니어링 공동구 제06-378호
전기정보통신 설계 감리 및 소방설계
(주)정명기술단
대표・기술사 이 정 환

PROJECT TITLE

LS Electric
R-Center 구축

PROJECT NUMBER

224001

DESIGN CONSULTANT

가 운 건 축
GAUN | Architects & Engineers
서울시 강남구 언주로 609, 10층 (논현동, 팍스타워)
Tel:82-2-3443-7799 Fax:82-2-3443-3807
www.gaun.co.kr

NOTES

KEY PLAN

NO.	DESCRIPTION	DATE

ISSUES & REVISIONS

BUILDING NAME

DRAWING TITLE

옥외 전력간선설비 인입 배치도

DRAWN		SCALE: A1 : 1/ 500, A3 : 1/1000
CHECK 1	안 동 식	
CHECK 2	이 은 진	DATE: 2024.04
APPR.	정 용 재	

DRAWING NO.

EE-00-003