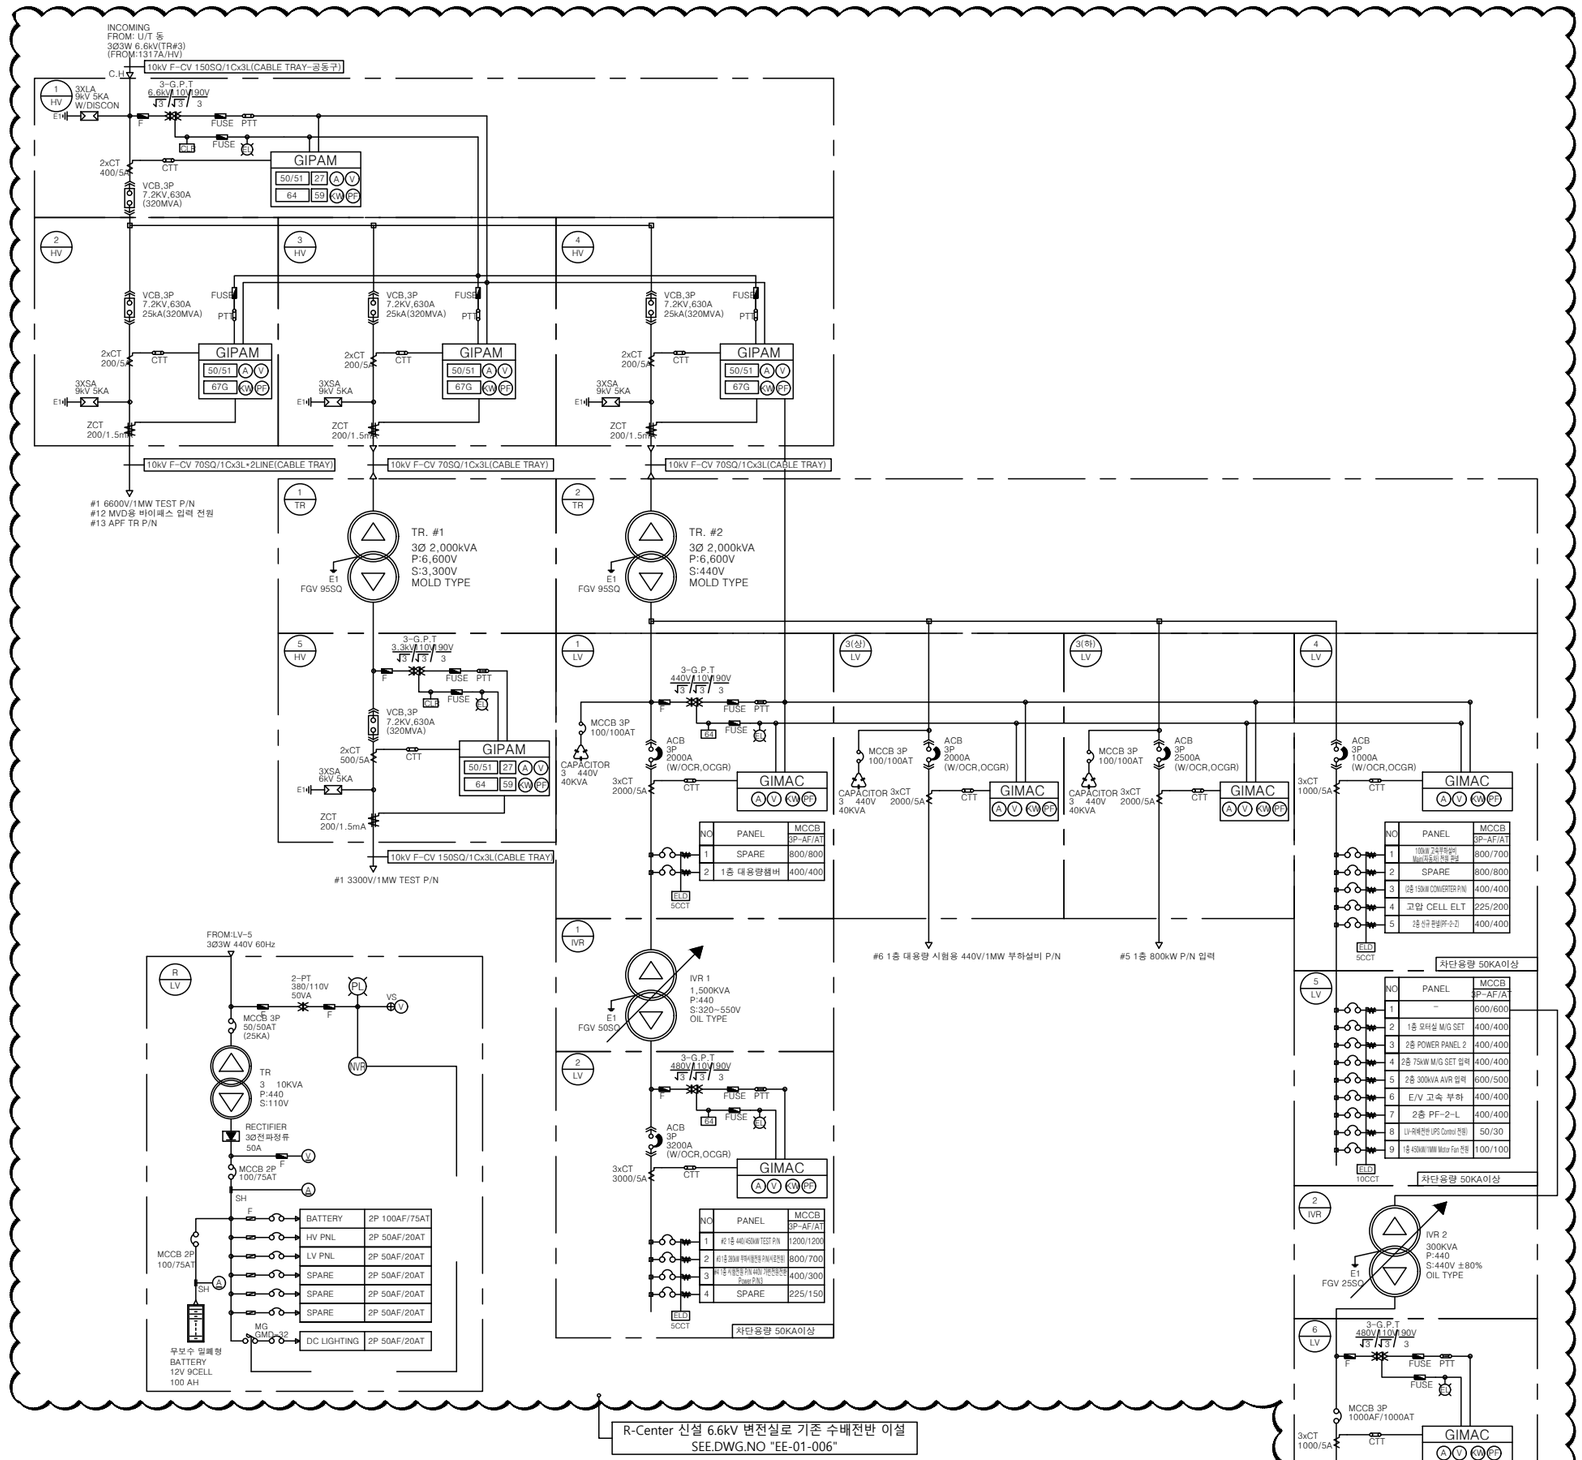



# 6.6kV 변전설비 단선결선도 - A동 지상1층 인버터 시험센터 변전실 (기존)

축척:A1 : NONE
A3 : NONE

전력시설물종합설계업 제서울 E-1-055호
엔지니어링 활동주체 제06-378호
전기,정보통신 설계,감리 및 소방설계
(주)정명기술단
대표・기술사 이 정 환

PROJECT TITLE

LS Electric
R-Center 구축

PROJECT NUMBER

224001

DESIGN CONSULTANT

가운건축

**GAUN** I Architects & Engineers

서울시 강남구 언주로 609, 10층 (논현동, 팍스타워)
Tel:82-2-3443-7799 Fax:82-2-3443-3807
www.gaun.co.kr

NOTES

1. 도면에 표기되지 않은 사항은 현장 확인 후 관계 법령의 테두리 내에서 시행하되 현장 감독관의 선승인을 득한후 시공하도록 한다.
2. [redacted] : 본공사에 해당함.

KEY PLAN

| NO. | DESCRIPTION | DATE |
|---|---|---|
| | | |
| | | |
| | | |
| | | |
| | | |
| | | |
| | | |
| | | |
| | | |

ISSUES & REVISIONS

BUILDING NAME

DRAWING TITLE

6.6kV 변전설비 단선결선도 -
A동 지상1층 인버터 시험센터 변전실
(기존)

| | | | |
|---|---|---|---|
| DRAWN | | SCALE | A1 : NONE<br>A3 : NONE |
| CHECK 1 | 안 동 식 | | |
| CHECK 2 | 이 은 진 | DATE | 2024.04 |
| APPR. | 정 용 재 | | |

DRAWING NO.

EE-01-003