

CABLE SCHEDULE

NO	CABLE & CONDUIT SIZE
(T)	28C (UTP 0.5mm/25Px1,CAT.5e)
(T1)	16C (UTP 0.5mm/4Px1, CAT.5e)
(T2)	16C (UTP 0.5mm/4Px2, CAT.5e)
(T3)	22C (UTP 0.5mm/4Px3, CAT.5e)
(T4)	22C (UTP 0.5mm/4Px4, CAT.5e)
(T5)	28C (UTP 0.5mm/4Px5, CAT.5e)
(T6)	28C (UTP 0.5mm/4Px6, CAT.5e)
(F)	ELP 100Ø (F/O CABLE S.M 12CORE)
(F1)	F/O CABLE S.M 2CORE
(F2)	F/O CABLE S.M 4CORE
(F3)	F/O CABLE S.M 8CORE
(F4)	F/O CABLE S.M 12CORE
(E1)	28C (EMPTY CONDUIT)
(E2)	36C (EMPTY CONDUIT)
(G1)	16C (F-GV 1 - 6sq)
(G2)	22C (F-GV 1 - 16sq)

주기사항

- 층간 방화 구획 처리.
- CABLE TRAY내 배관,배선시 전선관을 제외한 CABLE만 포설한다.
- CABLE TRAY내 공통 접지선은 1-GV 16sq로 한다.
- CABLE TRAY 통신용과 공용임
- 방화구획을 관통하는 부위에는 불연재의 방화재로 완전 방화구획이 되도록 차폐한다.
- SYMBOL
 - LAN OUTLET 2PORT
 - LAN OUTLET 1PORT
 - LAN OUTLET(TEL) 1PORT
 - 전화 단자함(Intermediate Terminal Board)
 - 광 OUTLET
 - SYSTEM BOX(LAN) 2PORT
 - SYSTEM BOX(LAN) 1PORT, (광) 1PORT
 - 무선 AP

LS Electric
R-Center 구축PROJECT NUMBER
624001

DESIGN CONSULTANT

가운 건축

GAUN I Architects & Engineers

서울시 강남구 연주로 141길 6. 5층 (논현동, 백향빌딩)
Tel:82-2-3443-7799 Fax:82-2-3443-3807
www.gaun.co.kr

NOTES

KEY PLAN

▲		
▲		
▲		
▲		
▲		
▲		
▲		
▲		
NO.	DESCRIPTION	DATE

ISSUES & REVISIONS

BUILDING NAME

DRAWING TITLE

정보통신설비 계통도

DRAWN	SCALE
CHECK 1 안동식	A3 : 1/NONE A3 : 1/NONE
CHECK 2 이은진	DATE
APPR 정용재	2024.04
DRAWING NO.	


ET-01-001

▼ 지붕층 F.L

▼ 2층 F.L

▼ 1층 F.L

▼ PIT층 F.L

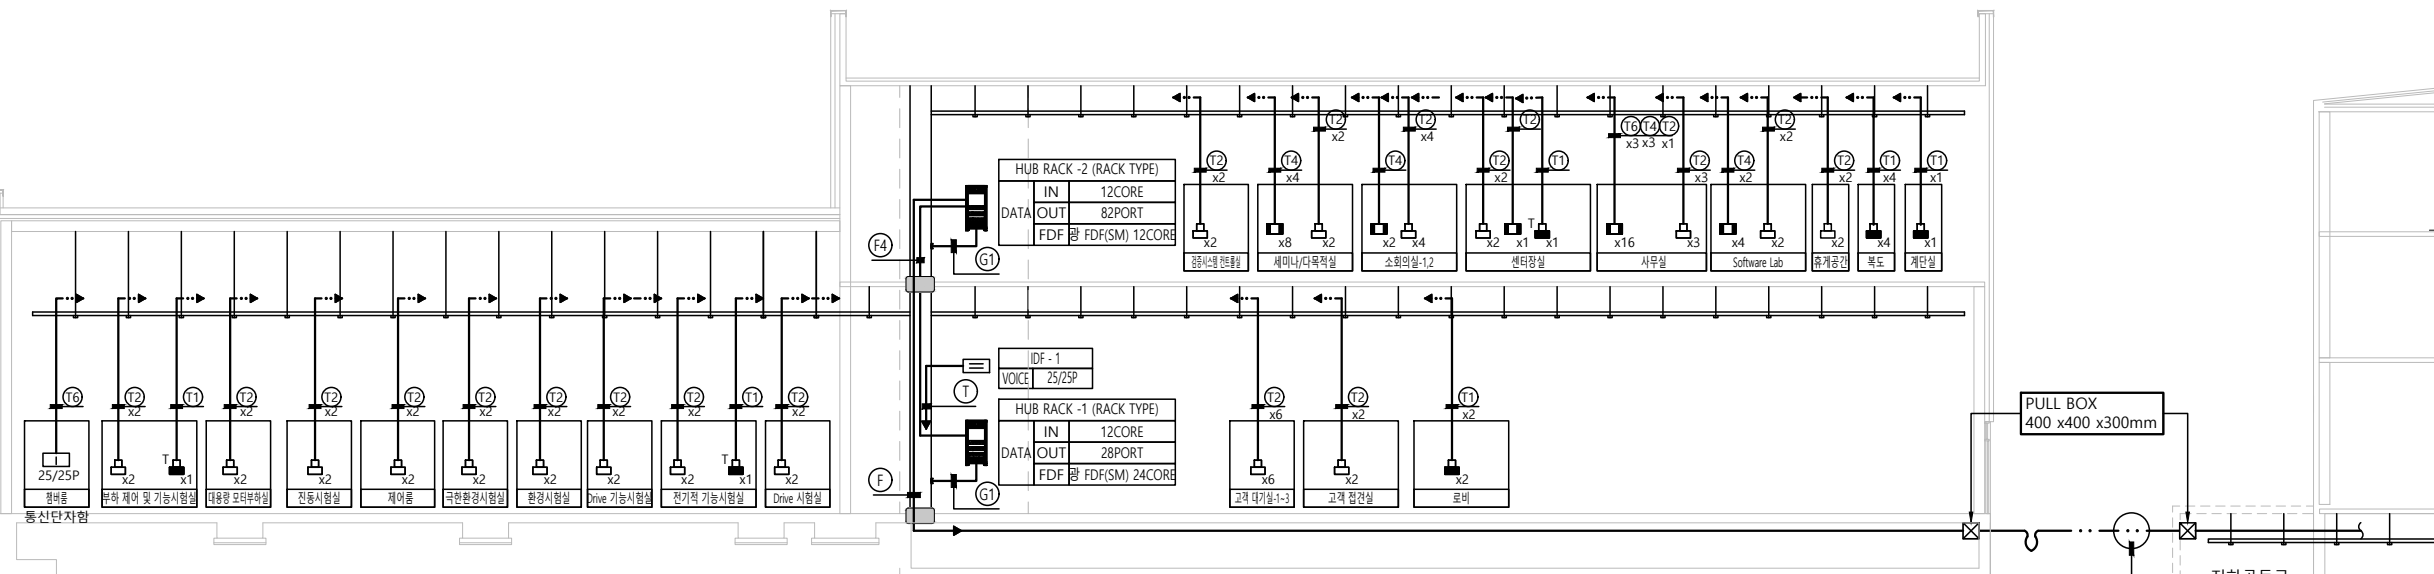

ELP 50Ø	FROM : 사무동 지상1층 통신실 UTP 0.5mm/25Px1,CAT.5 FROM : 사무동 지상2층 전산실 FIBER OPTICAL S.M 12CORE EMPTY PIPE (ELP50)
---------	---

(옥외 정보통신 인입 배치도 참조)

정보통신설비 계통도

축척:A1 : 1/NONE
A3 : 1/NONE전력시설물종합설계업 제서울 E-1-055호
엔지니어링 활동주체 제06-378호
전기·정보통신 설계·강리 및 소방설계
정명기술(주) 정명기술
대표·기술사 이정환엔지니어링활동주체신고증 신고번호:제 06-378호
기술부분:통신 정보처리 전문분야:정보통신
정명기술(주) 정명기술
통신선로산업기사 김근식