


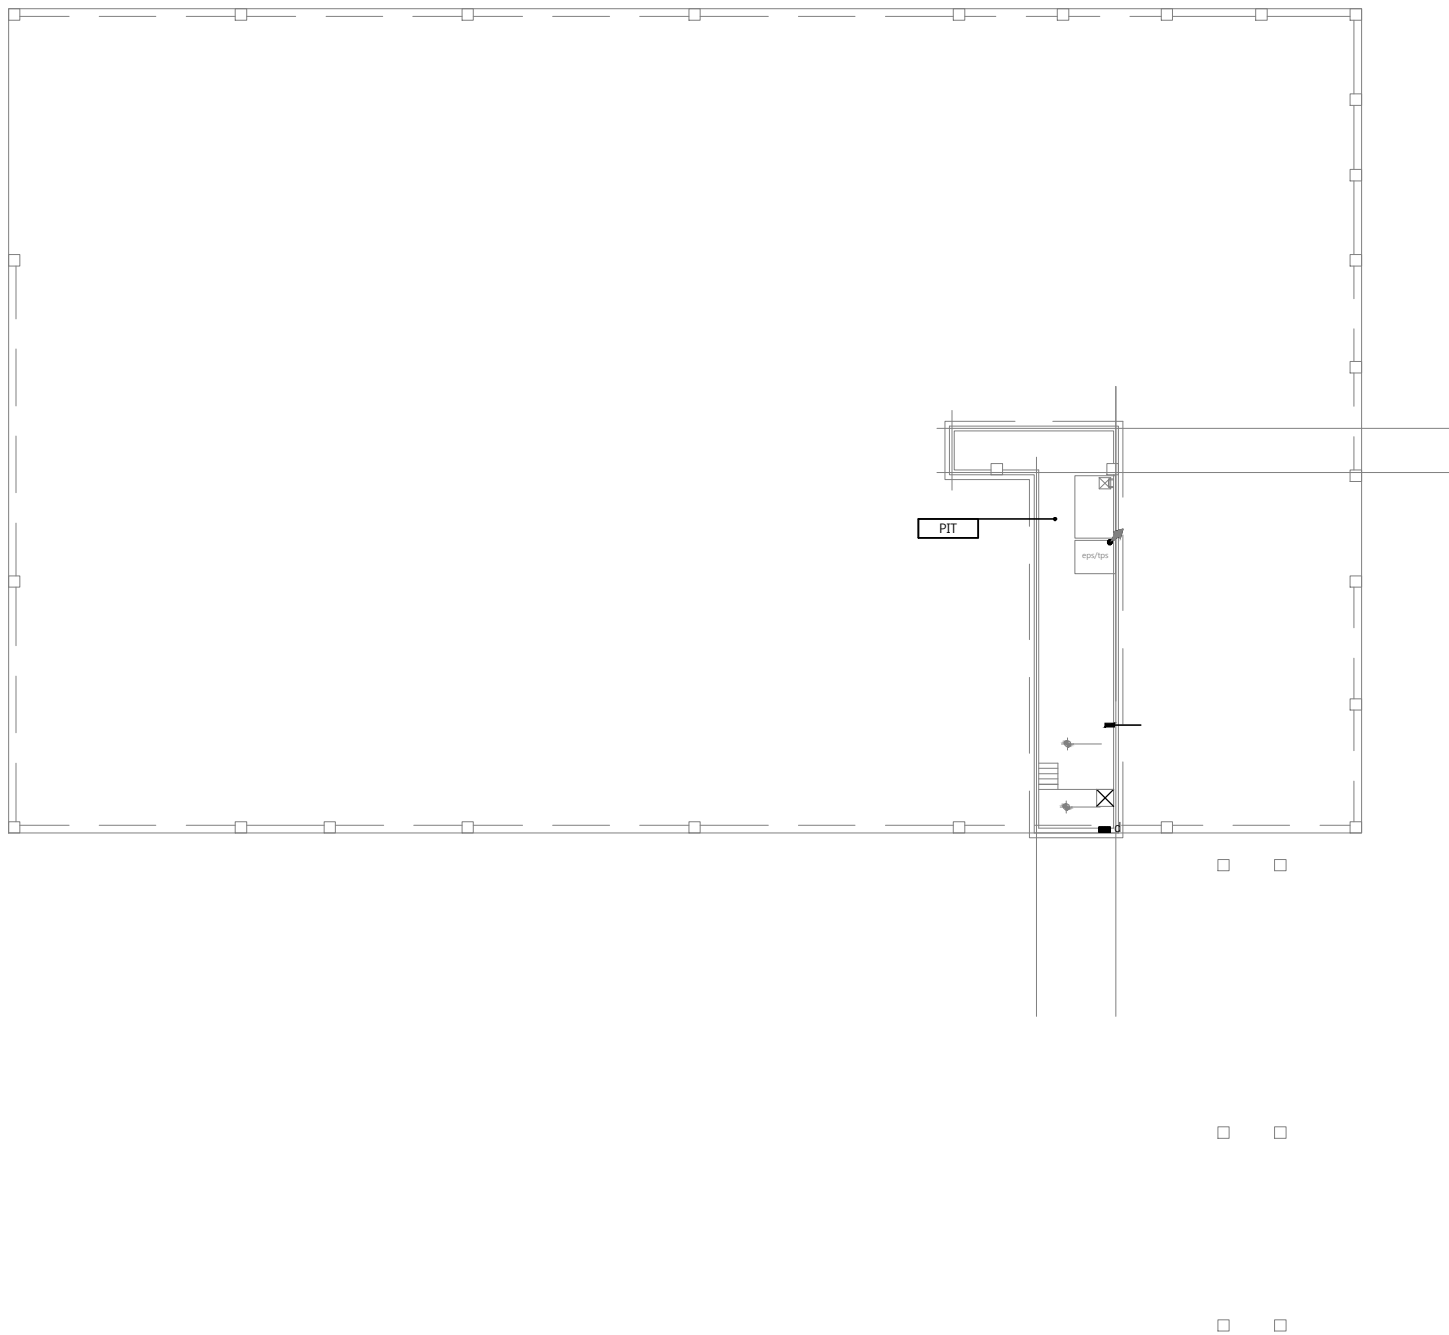

PIT층 정보통신설비 평면도

축척:A1 : 1/200
A3 : 1/400

주기사항

1. 배관, 배선
—— 슬라브 매입 배관 배선
---- 노출 배관 배선
--- 바닥 은폐 및 지중 매설 배관 배선
--- DUCT 및 TRAY내 배선

2. 통신용 배관, 배선
-T --- : 16C (UTP 0.5mm/4Px2, CAT.5e)
-T --- : 22C (UTP 0.5mm/4Px3, CAT.5e)
-T --- : 22C (UTP 0.5mm/4Px4, CAT.5e)
-T --- : 28C (UTP 0.5mm/4Px6, CAT.5e)
-T --- : 28C (UTP 0.5mm/4Px8, CAT.5e)
---FO--- : 16C (FIBER OPTICAL S.M 2CORE)
---CC--- : 16C (FIBER OPTICAL S.M 4CORE)

3. LEGEND
□ : LAN OUTLET 2PORT
□ : SYSTEM BOX(LAN) 2PORT
□ : SYSTEM BOX(LAN) 1PORT, (광) 1PORT
□ : LAN OUTLET(TEL) 1PORT
□ : 광 OUTLET
⊙ : 무선 AP
⊙ : CCTV
□ : 전화 단자함(Intermediate Terminal Board)
□_a : PULL BOX SIZE 150 x 150 x 100mm
□_b : PULL BOX SIZE 200 x 200 x 150mm
□_c : PULL BOX SIZE 300 x 300 x 200mm
□_d : PULL BOX SIZE 400 x 400 x 300mm

4. CABLE TRAY내 포설시 전선관을 제외한 CABLE만 포설한다.
5. CABLE TRAY 및 노출 배관 배선의 지지행거는 1,500mm마다 설치한다.
6. CABLE TRAY 내 접지선은 F-GV 16sq x 1를 사용한다.
7. 간선 규격 및 기타 사항은 계통도 참조.

전력시설물종합설계업 제서울 E-1-055호
엔지니어링 활동주체 제06-378호
전기 정보통신 설계 감리 및 소방설계
JM(주) 정 명 기 술 단
대표 · 기술사 이 정 환

엔지니어링활동주체신고증 신고번호제 06-378호
기술분·통신 정보처리 전문분야 정보통신
JM(주) 정 명 기 술 단
통신선로산업기사 김 근 식

PROJECT TITLE

LS Electric
R-Center 구축

PROJECT NUMBER

624001

DESIGN CONSULTANT

가운 건축

GAUN | Architects & Engineers

서울시 강남구 연주로 141길 6 5층 (논현동, 백향빌딩)
Tel:82-2-3443-7799 Fax:82-2-3443-3807
www.gaun.co.kr

NOTES

KEY PLAN

△		
△		
△		
△		
△		
△		
△		
△		
△		
NO.	DESCRIPTION	DATE

ISSUES & REVISIONS

BUILDING NAME

DRAWING TITLE

PIT층
정보통신설비 평면도

DRAWN	SCALE
CHECK 1 안 동 식	A3 : 1/200 A3 : 1/400
CHECK 2 이 은 진	DATE
APPR 정 용 재	2024.04

DRAWING NO.

ET-01-002