


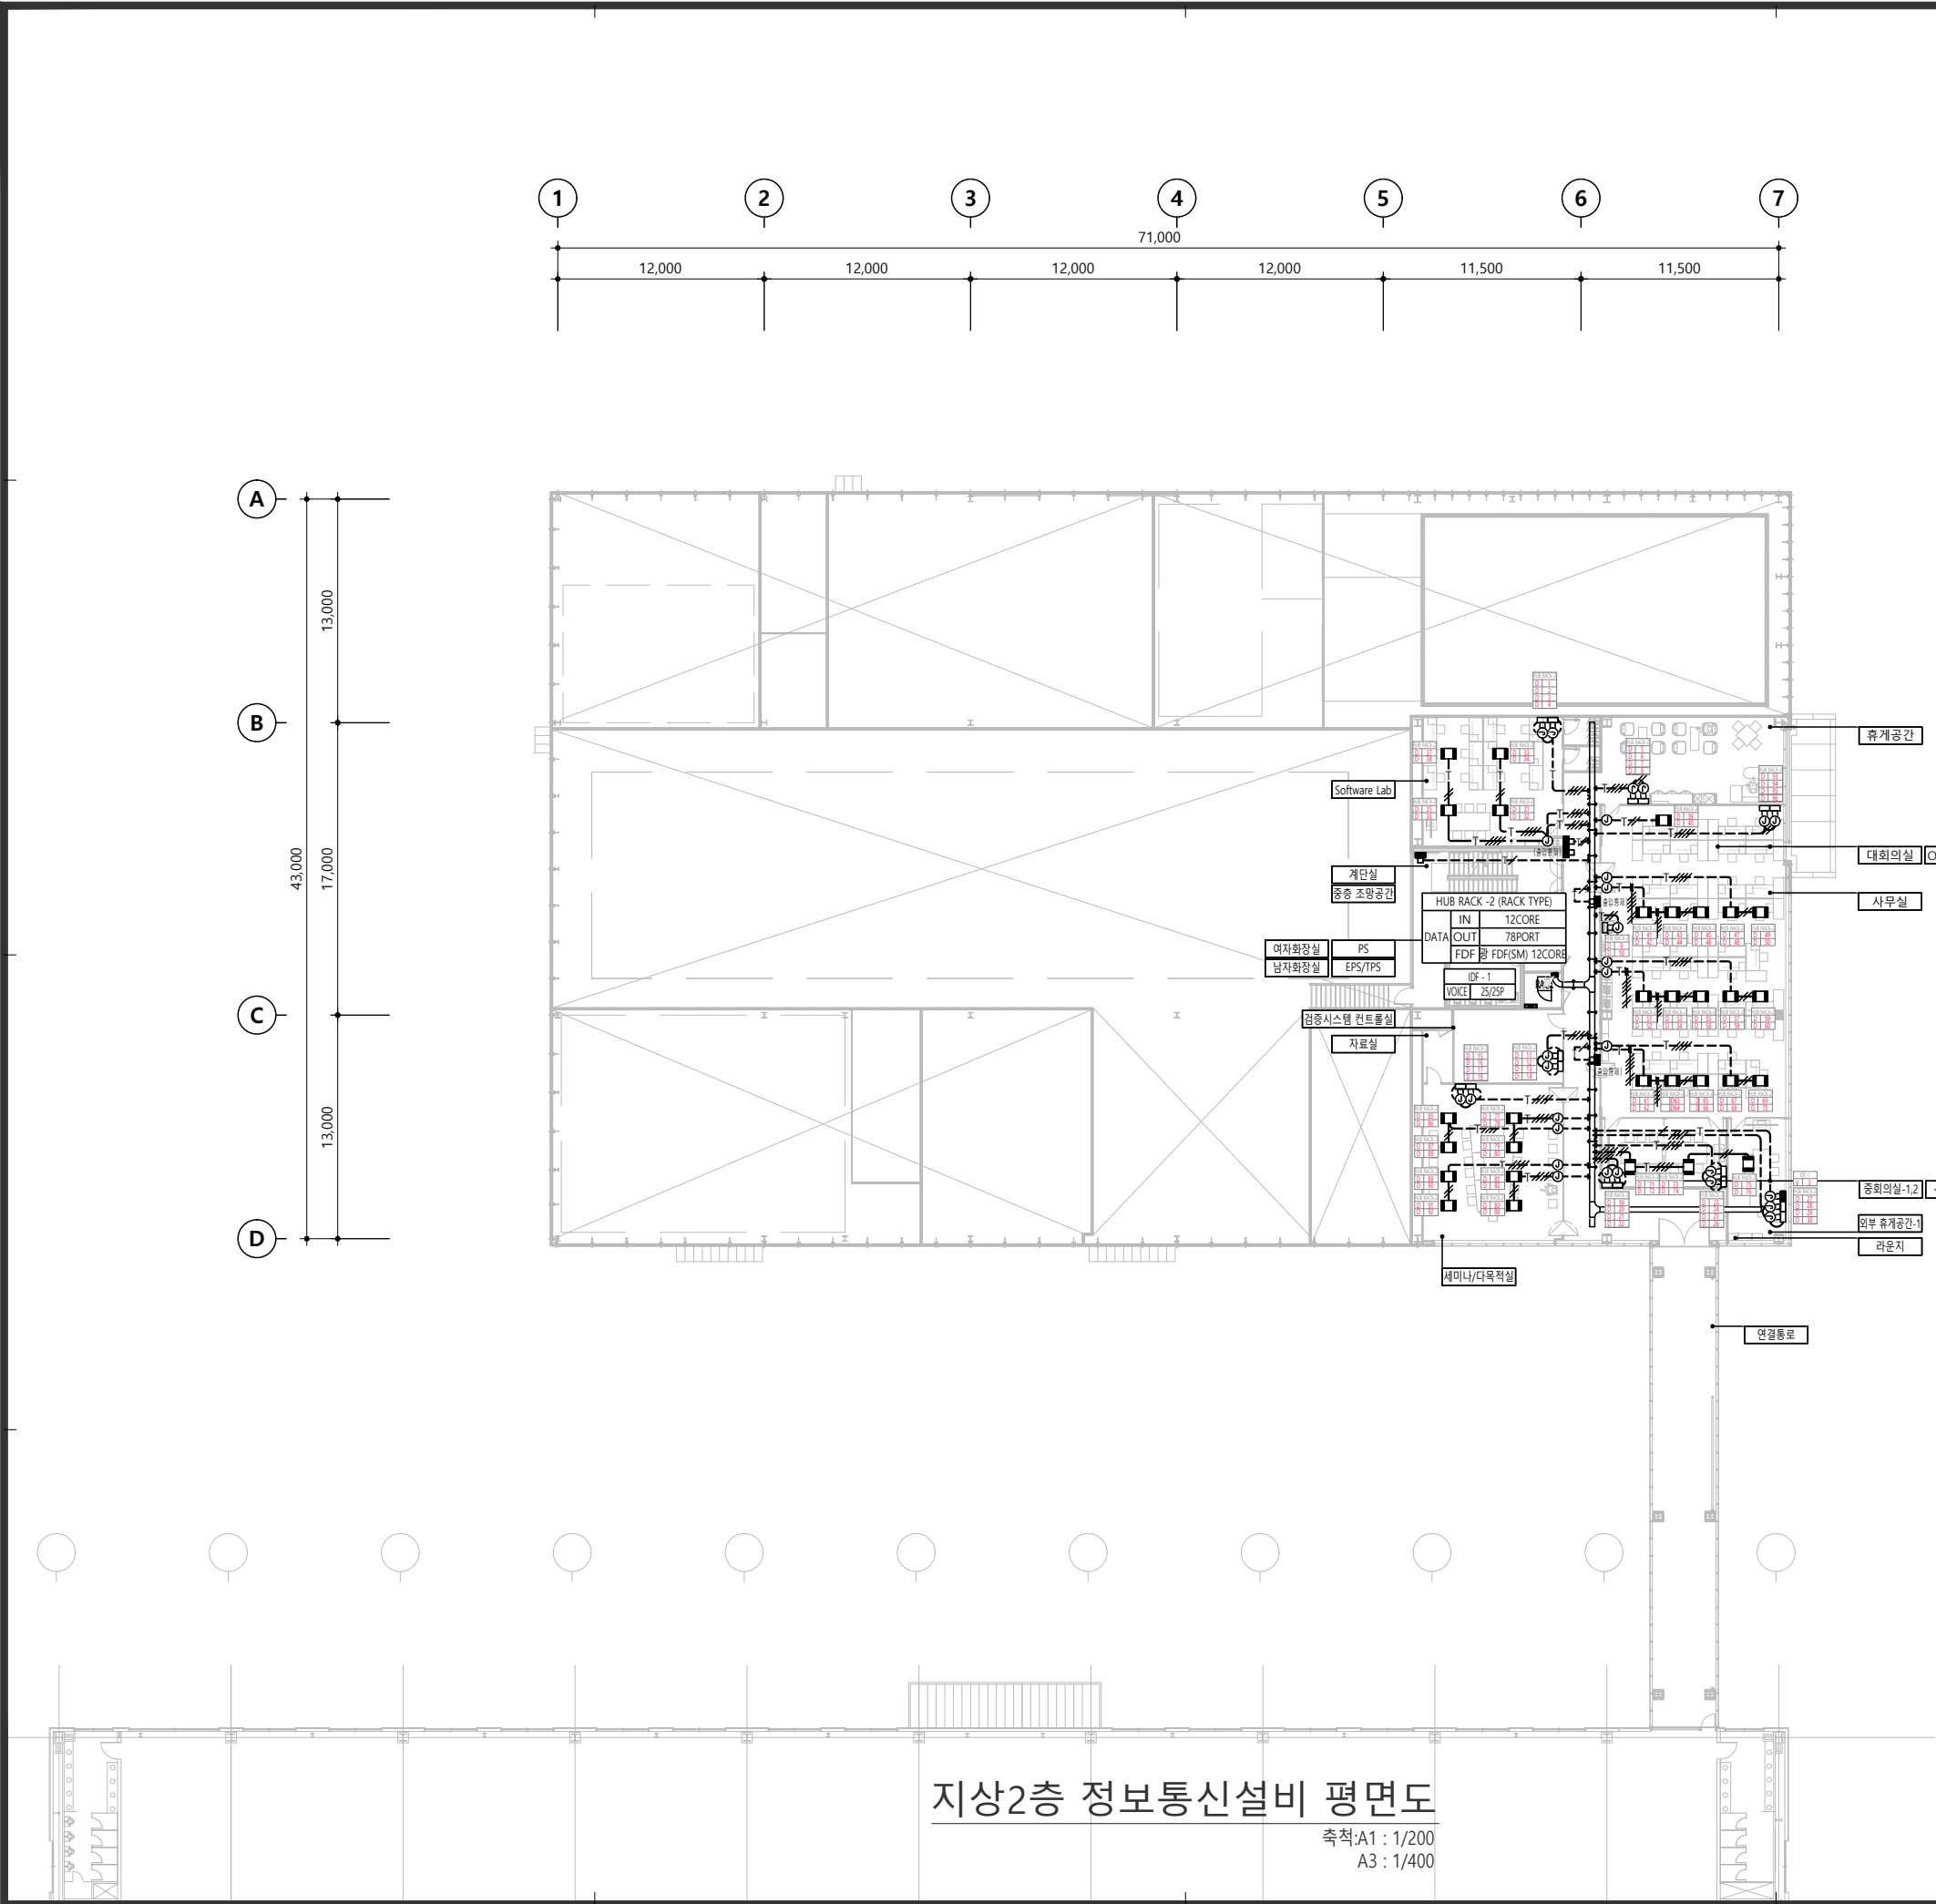

- 주기사항**
1. 배관, 배선
—— 슬라브 매입 배관 배선
---- 노출 배관 배선
--- 바닥 은폐 및 지중 매설 배관 배선
--- DUCT 및 TRAY내 배선
2. 통신용 배관, 배선
-T- : 16C (UTP 0.5mm/4Px2, CAT.5e)
-T- : 22C (UTP 0.5mm/4Px3, CAT.5e)
-T- : 22C (UTP 0.5mm/4Px4, CAT.5e)
-T- : 28C (UTP 0.5mm/4Px6, CAT.5e)
-T- : 28C (UTP 0.5mm/4Px8, CAT.5e)
-FO- : 16C (FIBER OPTICAL S.M 2CORE)
-CC- : 16C (FIBER OPTICAL S.M 4CORE)
3. LEGEND
□ : LAN OUTLET 2PORT
□ : SYSTEM BOX(LAN) 2PORT
□ : SYSTEM BOX(LAN) 1PORT, (광) 1PORT
□ : LAN OUTLET(TEL) 1PORT
□ : 광 OUTLET
○ : 무선 AP
□ : CCTV
□ : 전화 단자함(Intermediate Terminal Board)
□_a : PULL BOX SIZE 150 x 150 x 100mm
□_b : PULL BOX SIZE 200 x 200 x 150mm
□_c : PULL BOX SIZE 300 x 300 x 200mm
□_d : PULL BOX SIZE 400 x 400 x 300mm
4. CABLE TRAY내 포설시 전선관을 제외한 CABLE만 포설한다.
5. CABLE TRAY 및 노출 배관 배선의 지지행거는 1,500mm마다 설치한다.
6. CABLE TRAY 내 접지선은 F-GV 16sq x 1를 사용한다.
7. 간선 규격 및 기타 사항은 계통도 참조.

PROJECT TITLE

LS Electric
R-Center 구축

PROJECT NUMBER

624001

DESIGN CONSULTANT

가운 건축
GAUN I Architects & Engineers
서울시 강남구 연주로 141길 6. 5층 (논현동, 백랑빌딩)
Tel:82-2-3443-7799 Fax:82-2-3443-3807
www.gاون.co.kr

NOTES

KEY PLAN

△		
△		
△		
△		
△		
△		
△		
△		
△		
NO.	DESCRIPTION	DATE

ISSUES & REVISIONS

BUILDING NAME

DRAWING TITLE

지상2층
정보통신설비 평면도

DRAWN	SCALE
CHECK 1 안동식	A3 : 1/200 A3 : 1/400
CHECK 2 이은진	DATE
APPR 정용재	2024.04

DRAWING NO.

ET-01-004

지상2층 정보통신설비 평면도
축척:A1 : 1/200
A3 : 1/400

전력시설물종합설계업 제서울 E-1-055호
엔지니어링 활동주체 제06-378호
전기정보통신설계감리 및 소방설계
JM(주) 정명기술단
대표·기술사 이정환

엔지니어링활동주체신고증 신고번호제 06-378호
기술부분:통신·정보처리 전문분야:정보통신
JM(주) 정명기술단
통신선로산업기사 김근식