

PROJECT TITLE

LS Electric
R-Center 구축

PROJECT NUMBER

624001

DESIGN CONSULTANT

가운 건축

GAUN | Architects & Engineers

서울시 강남구 연주로 141길 6 5층 (논현동, 백향빌딩)
Tel: 82-2-3443-7799 Fax: 82-2-3443-3807
www.gaun.co.kr

NOTES

KEY PLAN

△		
△		
△		
△		
△		
△		
△		
△		
NO.	DESCRIPTION	DATE

ISSUES & REVISIONS

BUILDING NAME

DRAWING TITLE


사무동 지상1층
정보통신 설비 평면도

DRAWN	SCALE
CHECK 1 안 동 식	A3 : 1/150 A3 : 1/300
CHECK 2 이 은 진	DATE
APPR 정 용 재	2024.04

DRAWING NO.

ET-01-006

60,000								
6,000	6,000	6,000	7,500	9,000	7,500	6,000	6,000	6,000

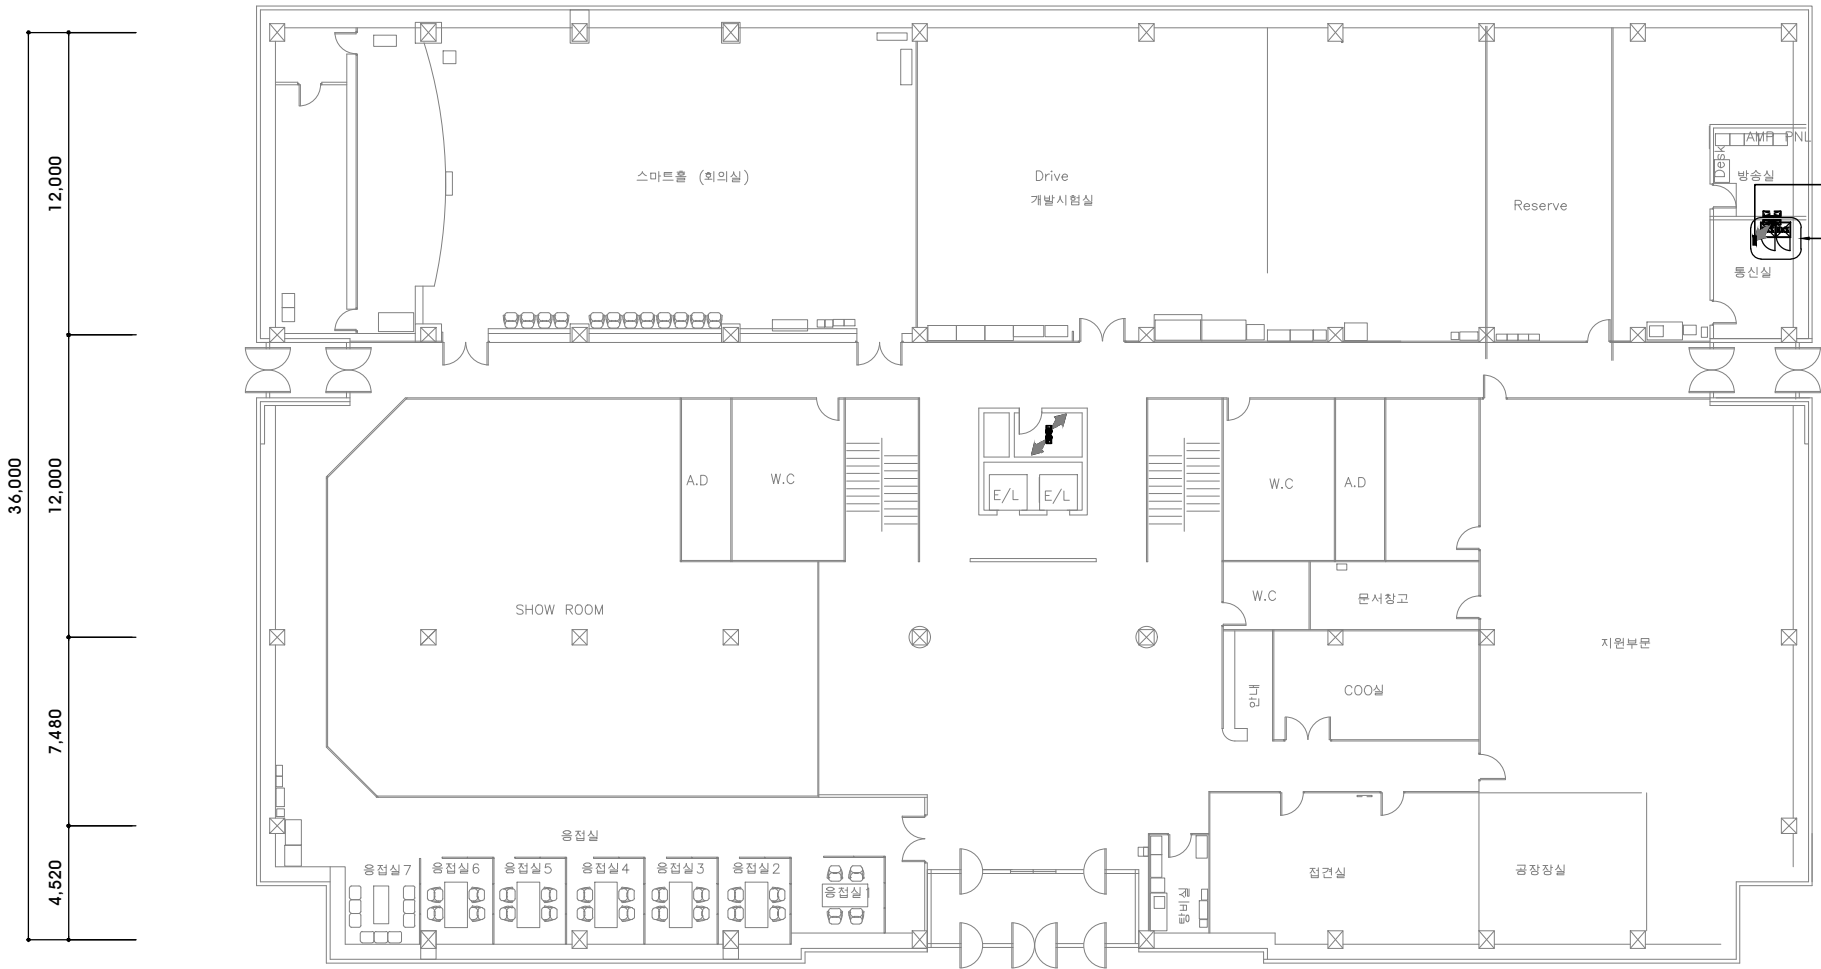

TO : 사무동 지상1층 통신실
UTP 0.5mm/25Px1,CAT.5 (28C)
바닥 약세스플로어속 노출배관배선

기존 통신실 IDF RACK
110 BLOCK 25Px1EA 신설

사무동 지상1층 정보통신 설비 평면도

축척:A1 : 1/150
A3 : 1/300

전력시설물종합설계업 제서울 E-1-055호
엔지니어링 활동주체 제06-378호
전기정보통신 설계·감리 및 소방설계
JM(주) 정명기술단
대표·기술사 이 정 환

엔지니어링활동주체신고증 신고번호제 06-378호
기술분야:통신·정보처리,전문분야:정보통신
JM(주) 정명기술단
통신선로산업기사 김 근 식