


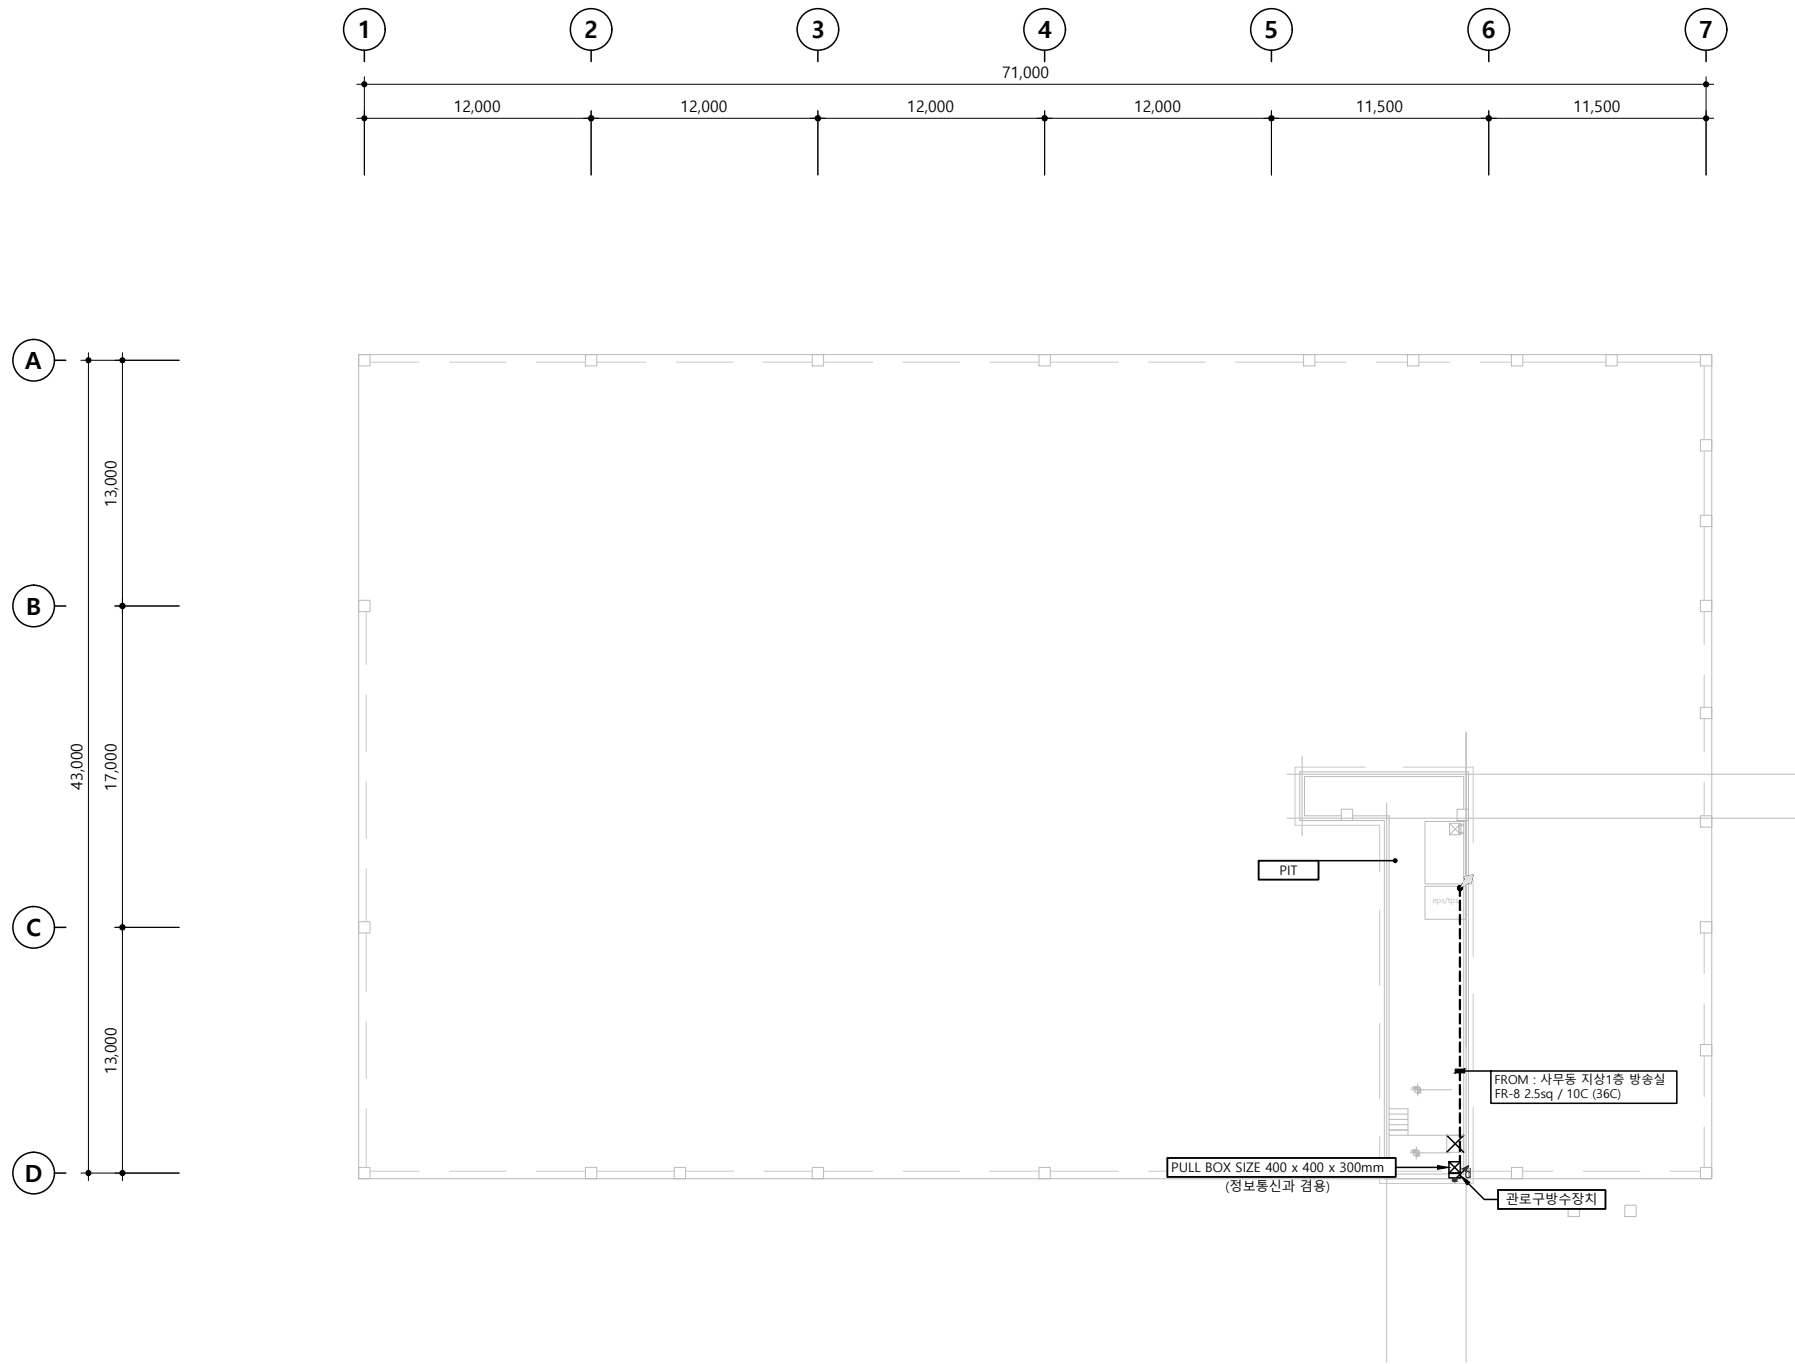

PIT층 방송 설비 평면도

축척:A1 : 1/200
A3 : 1/400

NOTE

1. 배관 배선

: 슬라브 매입 배관 배선

: 노출 배관 배선

: 바닥 은폐 및 지중 매설 배관 배선

: CABLE TRAY내 배선

2. 방송용 배관, 배선

— S — : 16C (HFIX 2-1.5sq)

— S // — : 16C (HFIX 3-1.5sq)

— S /// — : 16C (HFIX 4-1.5sq)

3. LEGEND

■ : SPEAKER 단자함

⊙ : 스피커 천정형 (3W)
(SPEAKER-CEILING TYPE)

⊙ : 월형형 SPEAKER (3W)
(SPEAKER-WALL BRACKET TYPE)

⊙ : 월형형 SPEAKER (10W)
(SPEAKER-WALL BRACKET TYPE)

☒_a : PULL BOX SIZE 150 x 150 x 100mm

☒_b : PULL BOX SIZE 200 x 200 x 150mm

☒_c : PULL BOX SIZE 300 x 300 x 200mm

☒_d : PULL BOX SIZE 400 x 400 x 300mm

4. 간선 규격 및 기타 사항은 계통도 참조.

PROJECT TITLE

LS Electric
R-Center 구축

PROJECT NUMBER

624001

DESIGN CONSULTANT

가운 건축
GAUN | Architects & Engineers

서울시 강남구 연주로 141길 6. 5층 (논현동, 백향빌딩)
Tel.82-2-3443-7799 Fax.82-2-3443-3807
www.gaun.co.kr

NOTES

KEY PLAN		
△		
△		
△		
△		
△		
△		
△		
△		
NO.	DESCRIPTION	DATE

ISSUES & REVISIONS		
BUILDING NAME		
DRAWING TITLE		
PIT층 방송 설비 평면도		
DRAWN	SCALE	A3 : 1/200 A3 : 1/400
CHECK 1 안 동 식	DATE	2024.04
CHECK 2 이 은 진		
APPR 정 용 재		
DRAWING NO.		
ET-02-002		

전력시설물종합설계업 제서울 E-1-055호
엔지니어링 활동주체 제06-378호
전기 정보통신 설계 감리 및 소방설계
JM(주) 정 명 기 술 단
대표·기술사 이 정 환

엔지니어링활동주체신고증 신고번호제 06-378호
기술부분·통신 정보처리 전문분야·정보통신
JM(주) 정 명 기 술 단
통신선로산업기사 김 근 식