


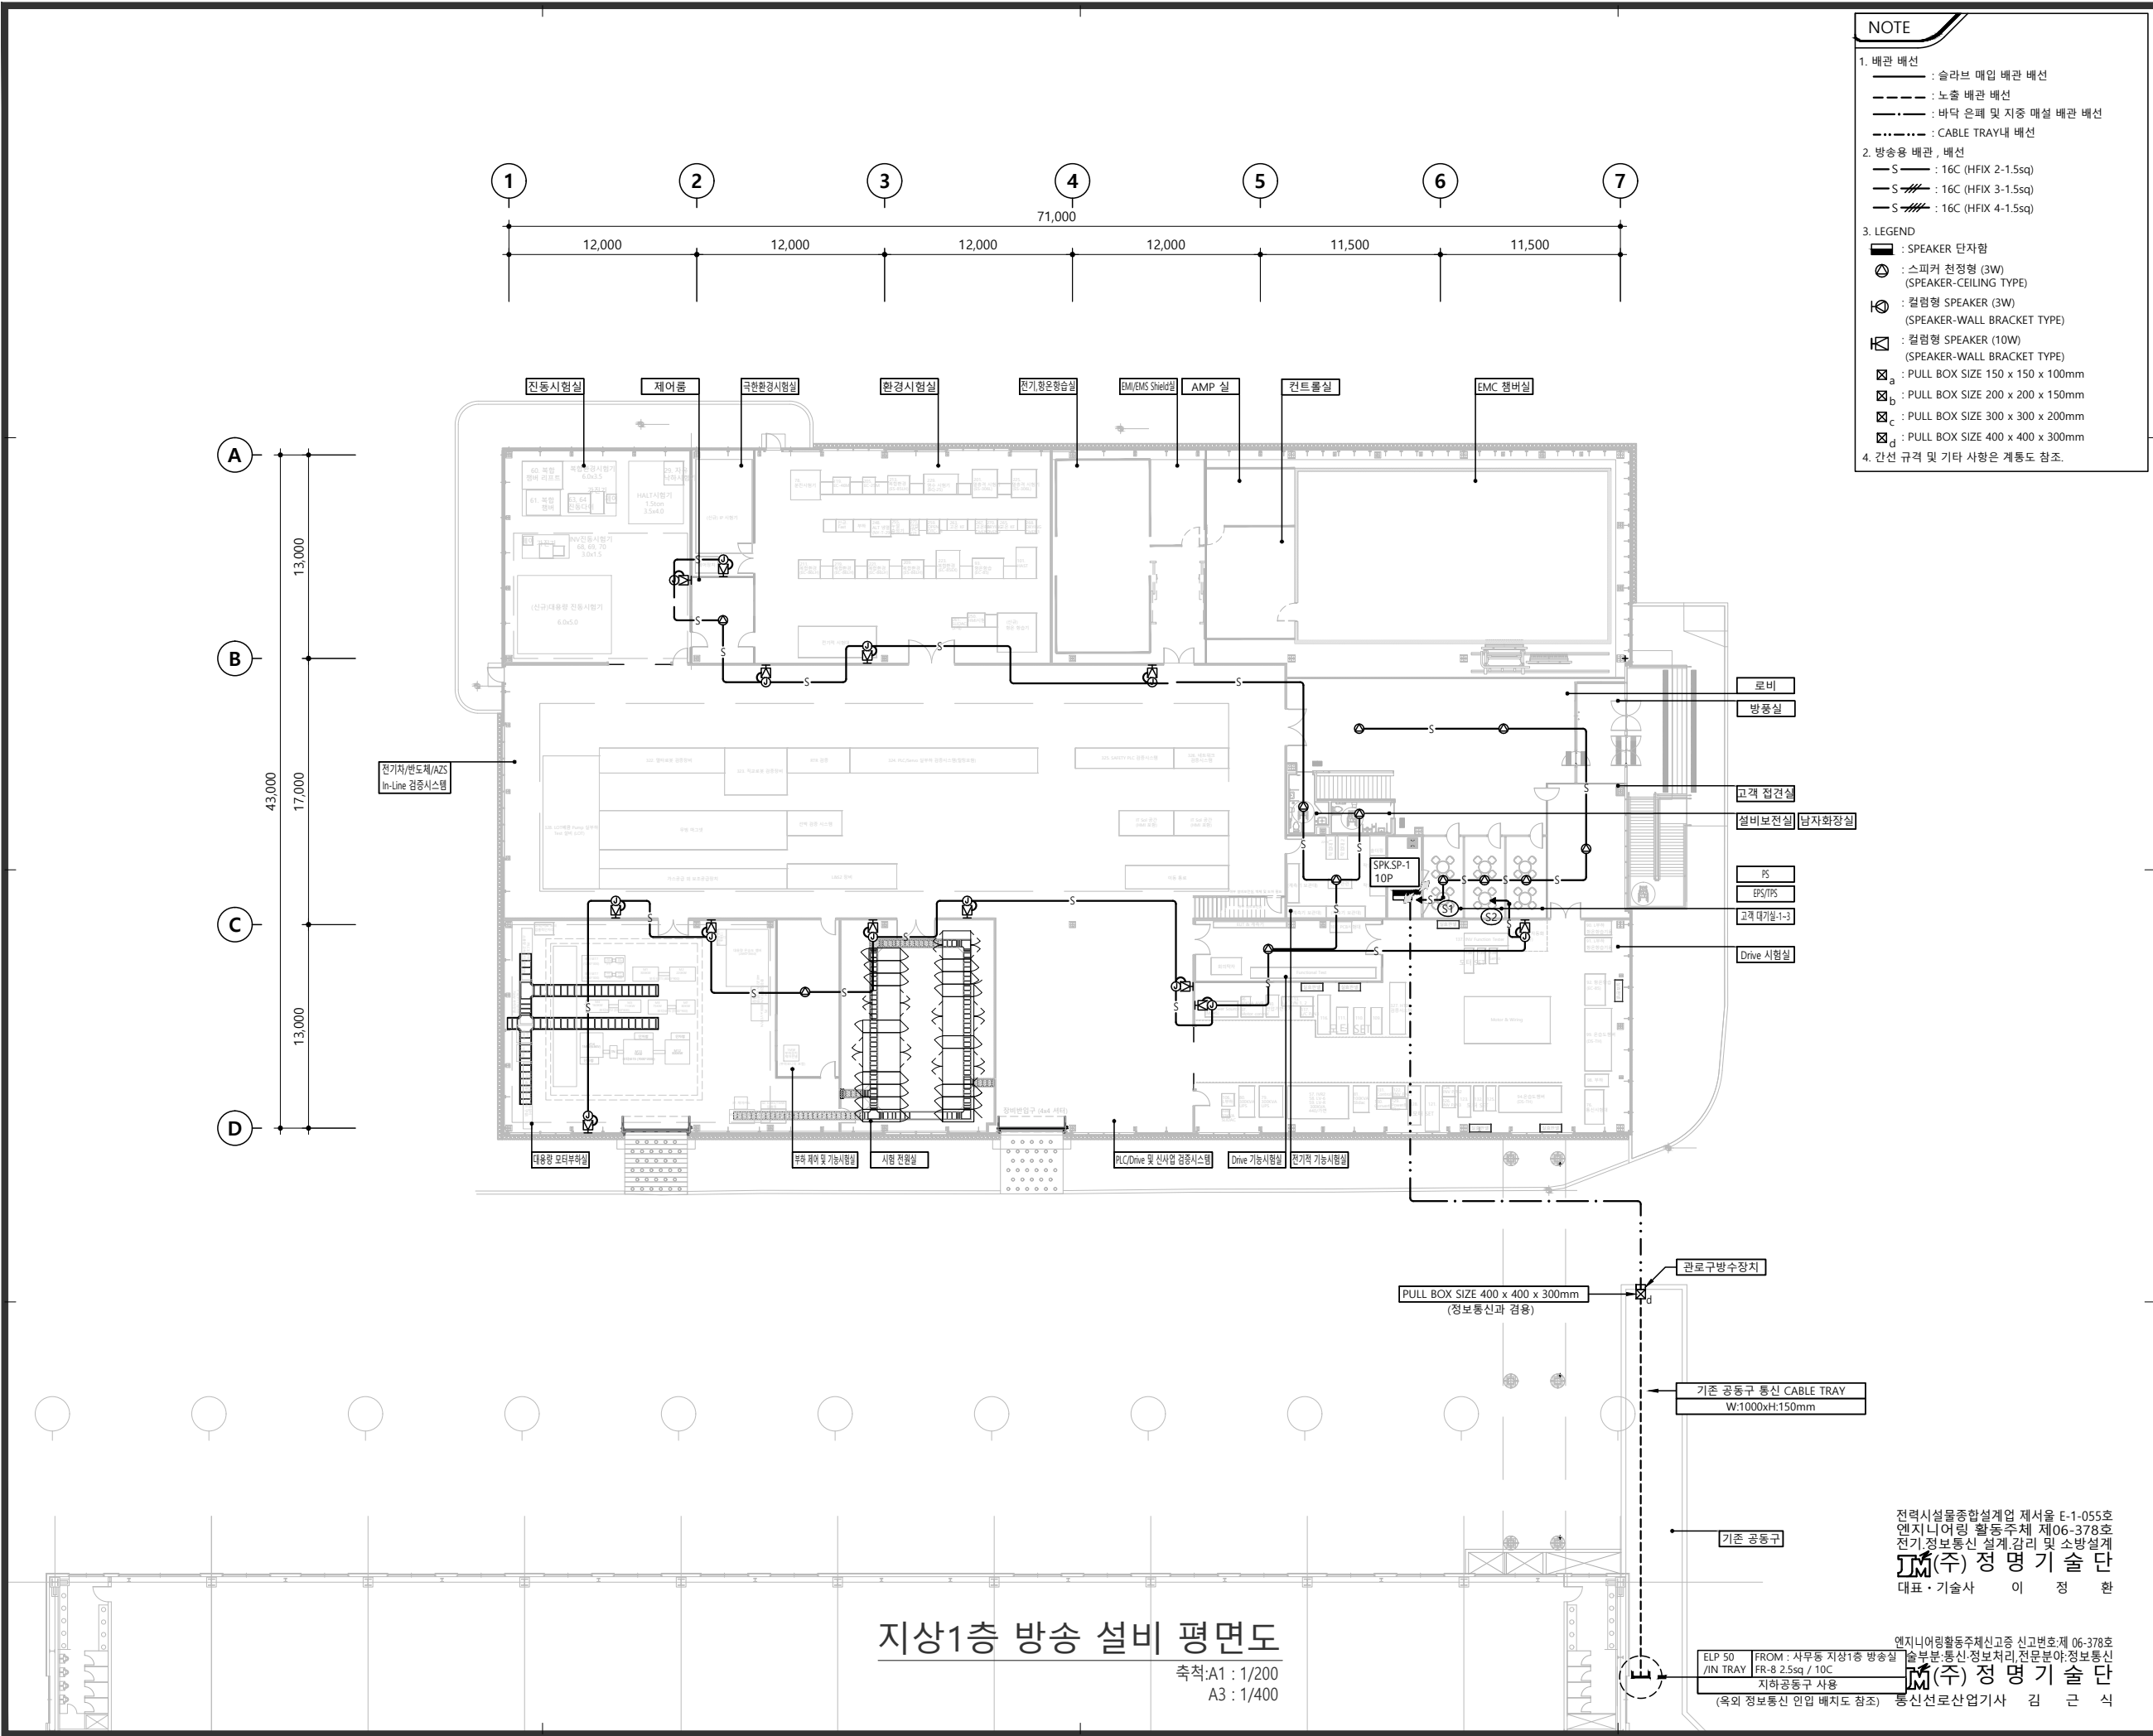

NOTE

1. 배관 배선

2. 방송용 배관, 배선

3. LEGEND

4. 간선 규격 및 기타 사항은 계통도 참조.

PROJECT TITLE

LS Electric
R-Center 구축

PROJECT NUMBER

624001

DESIGN CONSULTANT

가운 건축
GAUN | Architects & Engineers

서울시 강남구 연주로 141길 6. 5층 (논현동, 백향빌딩)
Tel.82-2-3443-7799 Fax.82-2-3443-3807
www.gaun.co.kr

NOTES

KEY PLAN

NO.

DESCRIPTION

DATE

ISSUES & REVISIONS

BUILDING NAME

DRAWING TITLE

지상1층 방송 설비 평면도

DRAWN

CHECK 1

CHECK 2

APPR

DRAWING NO.

SCALE

A3 : 1/200
A3 : 1/400

DATE

2024.04

ET-02-003