


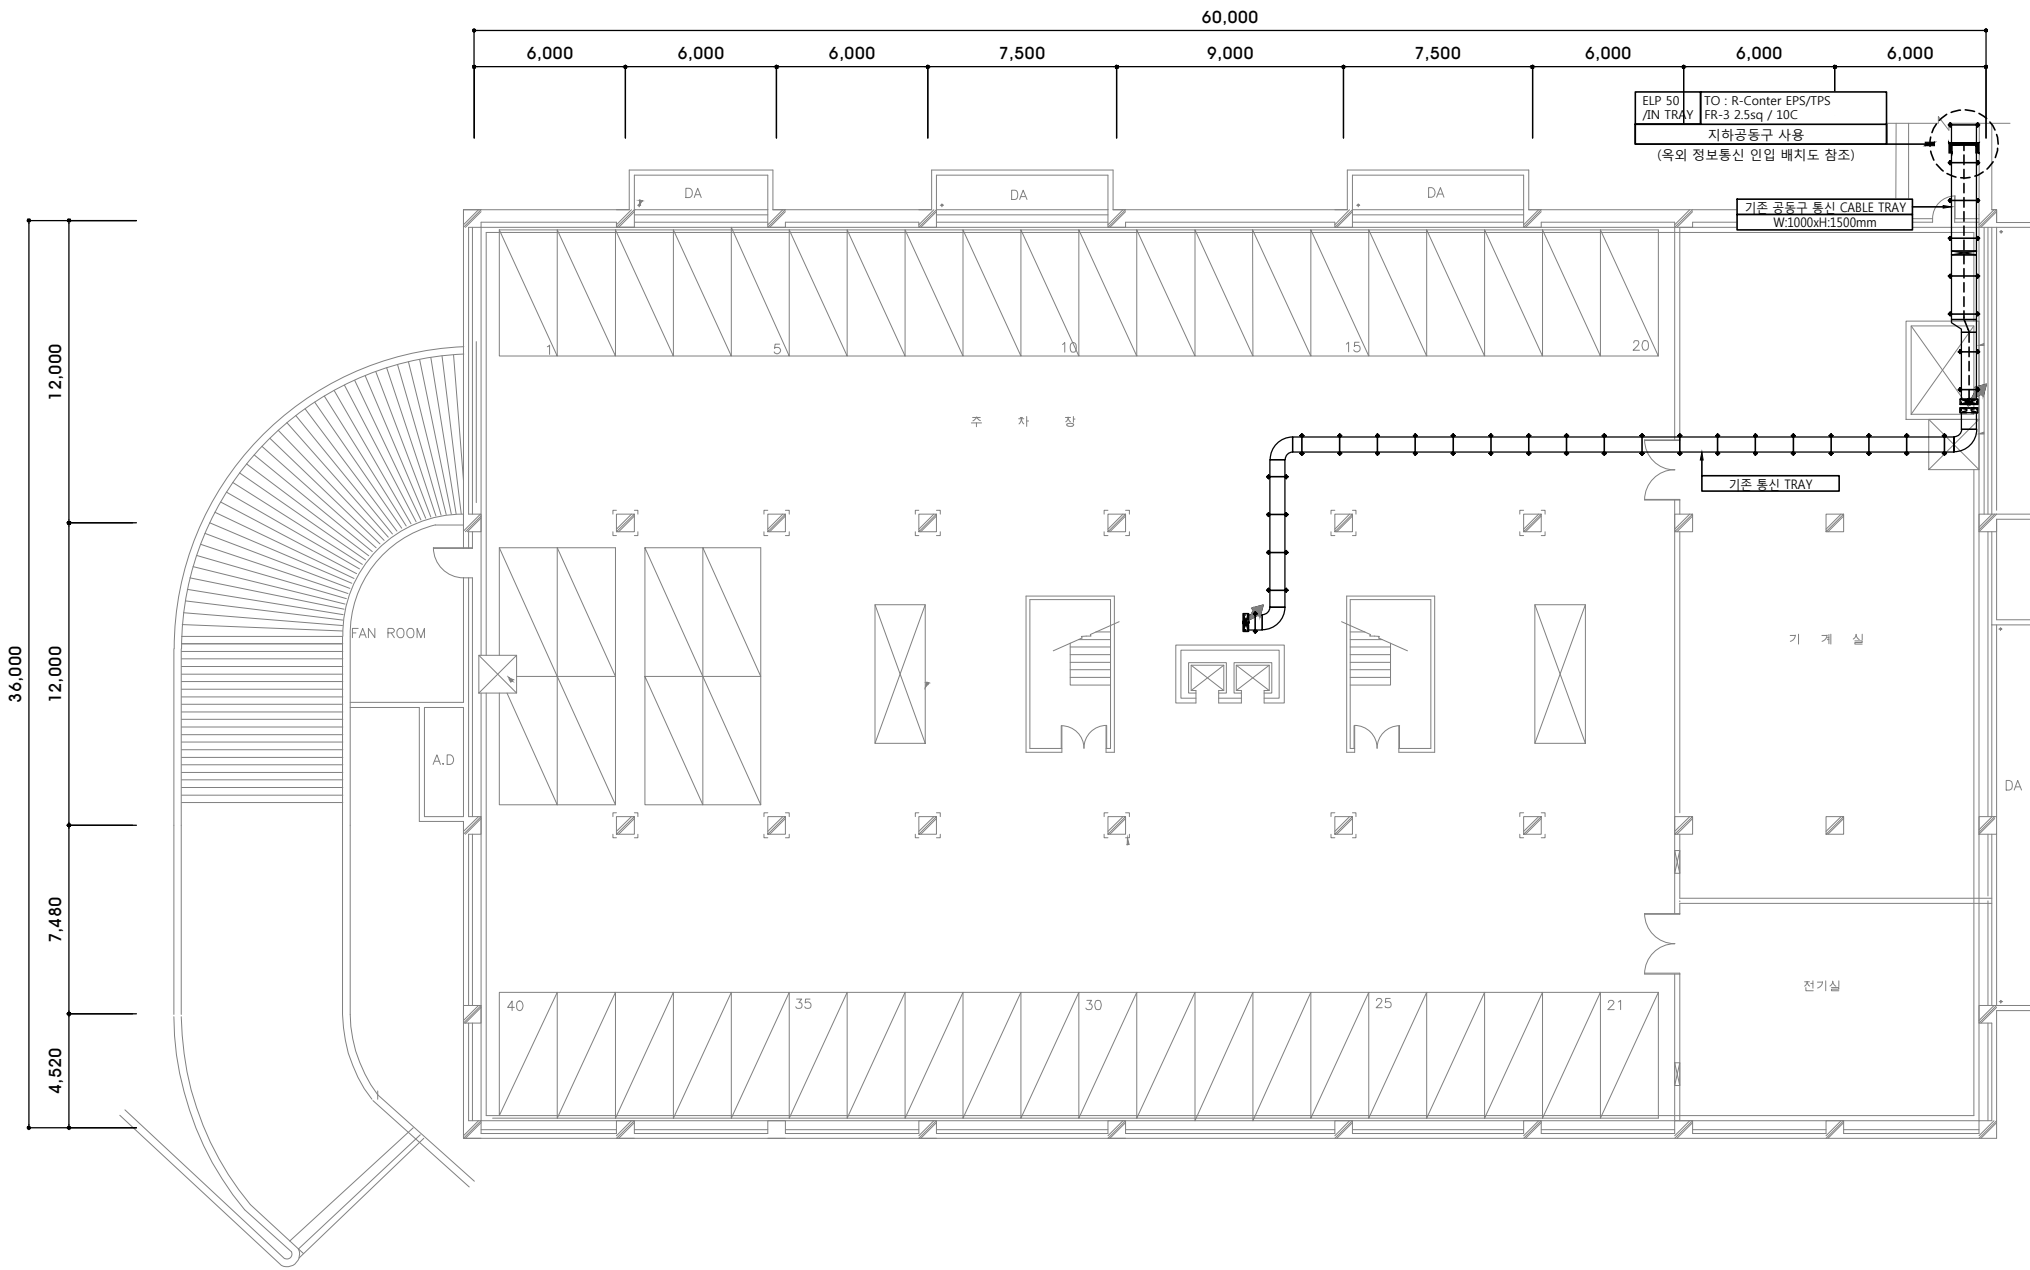

NOTE

- 배관 배선
—— : 슬라브 매입 배관 배선
----- : 노출 배관 배선
- · - · - : 바닥 은폐 및 지중 매설 배관 배선
- · · · · : CABLE TRAY내 배선
- 방송용 배관, 배선
— S — : 16C (HFIX 2-1.5sq)
— S // : 16C (HFIX 3-1.5sq)
— S /// : 16C (HFIX 4-1.5sq)
- LEGEND
■ : SPEAKER 단자함
⊙ : 스피커 천정형 (3W) (SPEAKER-CEILING TYPE)
⊙ : 컬럼형 SPEAKER (3W) (SPEAKER-WALL BRACKET TYPE)
⊙ : 컬럼형 SPEAKER (10W) (SPEAKER-WALL BRACKET TYPE)
⊠_a : PULL BOX SIZE 150 x 150 x 100mm
⊠_b : PULL BOX SIZE 200 x 200 x 150mm
⊠_c : PULL BOX SIZE 300 x 300 x 200mm
⊠_d : PULL BOX SIZE 400 x 400 x 300mm
- 간선 규격 및 기타 사항은 계통도 참조.

PROJECT TITLE

LS Electric
R-Center 구축

PROJECT NUMBER

624001

DESIGN CONSULTANT

가운 건축
GAUN I Architects & Engineers

서울시 강남구 연주로 141길 6 5층 (논현동, 백향빌딩)
Tel:82-2-3443-7799 Fax:82-2-3443-3807
www.gaun.co.kr

NOTES

KEY PLAN



NO.

DESCRIPTION

DATE

ISSUES & REVISIONS

BUILDING NAME

DRAWING TITLE

사무동 지하1층
방송 설비 평면도

DRAWN

CHECK 1 안동식

CHECK 2 이은진

APPR 정용재

DRAWING NO.

SCALE

A3 : 1/150
A3 : 1/300

DATE

2024.04

ET-02-005

사무동 지하1층 방송 설비 평면도

축척:A1 : 1/150
A3 : 1/300

전력시설물종합설계업 제서울 E-1-055호
엔지니어링 활동주체 제06-378호
전기정보통신 설계감리 및 소방설계
JM(주) 정명기술단
대표·기술사 이정환

엔지니어링활동주체신고증 신고번호제 06-378호
기술분야:통신 정보처리 전문분야:정보통신
JM(주) 정명기술단
통신선로산업기사 김근식