

PROJECT TITLE

LS Electric
R-Center 구축

PROJECT NUMBER

624001

DESIGN CONSULTANT

가운 건축

GAUN | Architects & Engineers

서울시 강남구 언주로 141길 6 5층 (논현동, 백향빌딩)
Tel:82-2-3443-7799 Fax:82-2-3443-3807
www.gaun.co.kr

NOTES

KEY PLAN

△		
△		
△		
△		
△		
△		
△		
△		
NO.	DESCRIPTION	DATE

ISSUES & REVISIONS

BUILDING NAME


DRAWING TITLE

통합배선설비 구성도

DRAWN	SCALE
CHECK 1 안 동 식	A3 : 1/NONE A3 : 1/NONE
CHECK 2 이 은 진	DATE
APPR 정 용 재	2024.04
DRAWING NO.	ET-03-001

엔지니어링활동주체신고증 신고번호제 E-1-055호
엔지니어링 활동주체 제06-378호
전기정보통신 설계·감리 및 소방설계
JM(주) 정 명 기 술 단
대표·기술사 이 정 환

엔지니어링활동주체신고증 신고번호제 06-378호
기술분야:통신·정보처리,전문분야:정보통신
JM(주) 정 명 기 술 단
통신선로산업기사 김 근 식

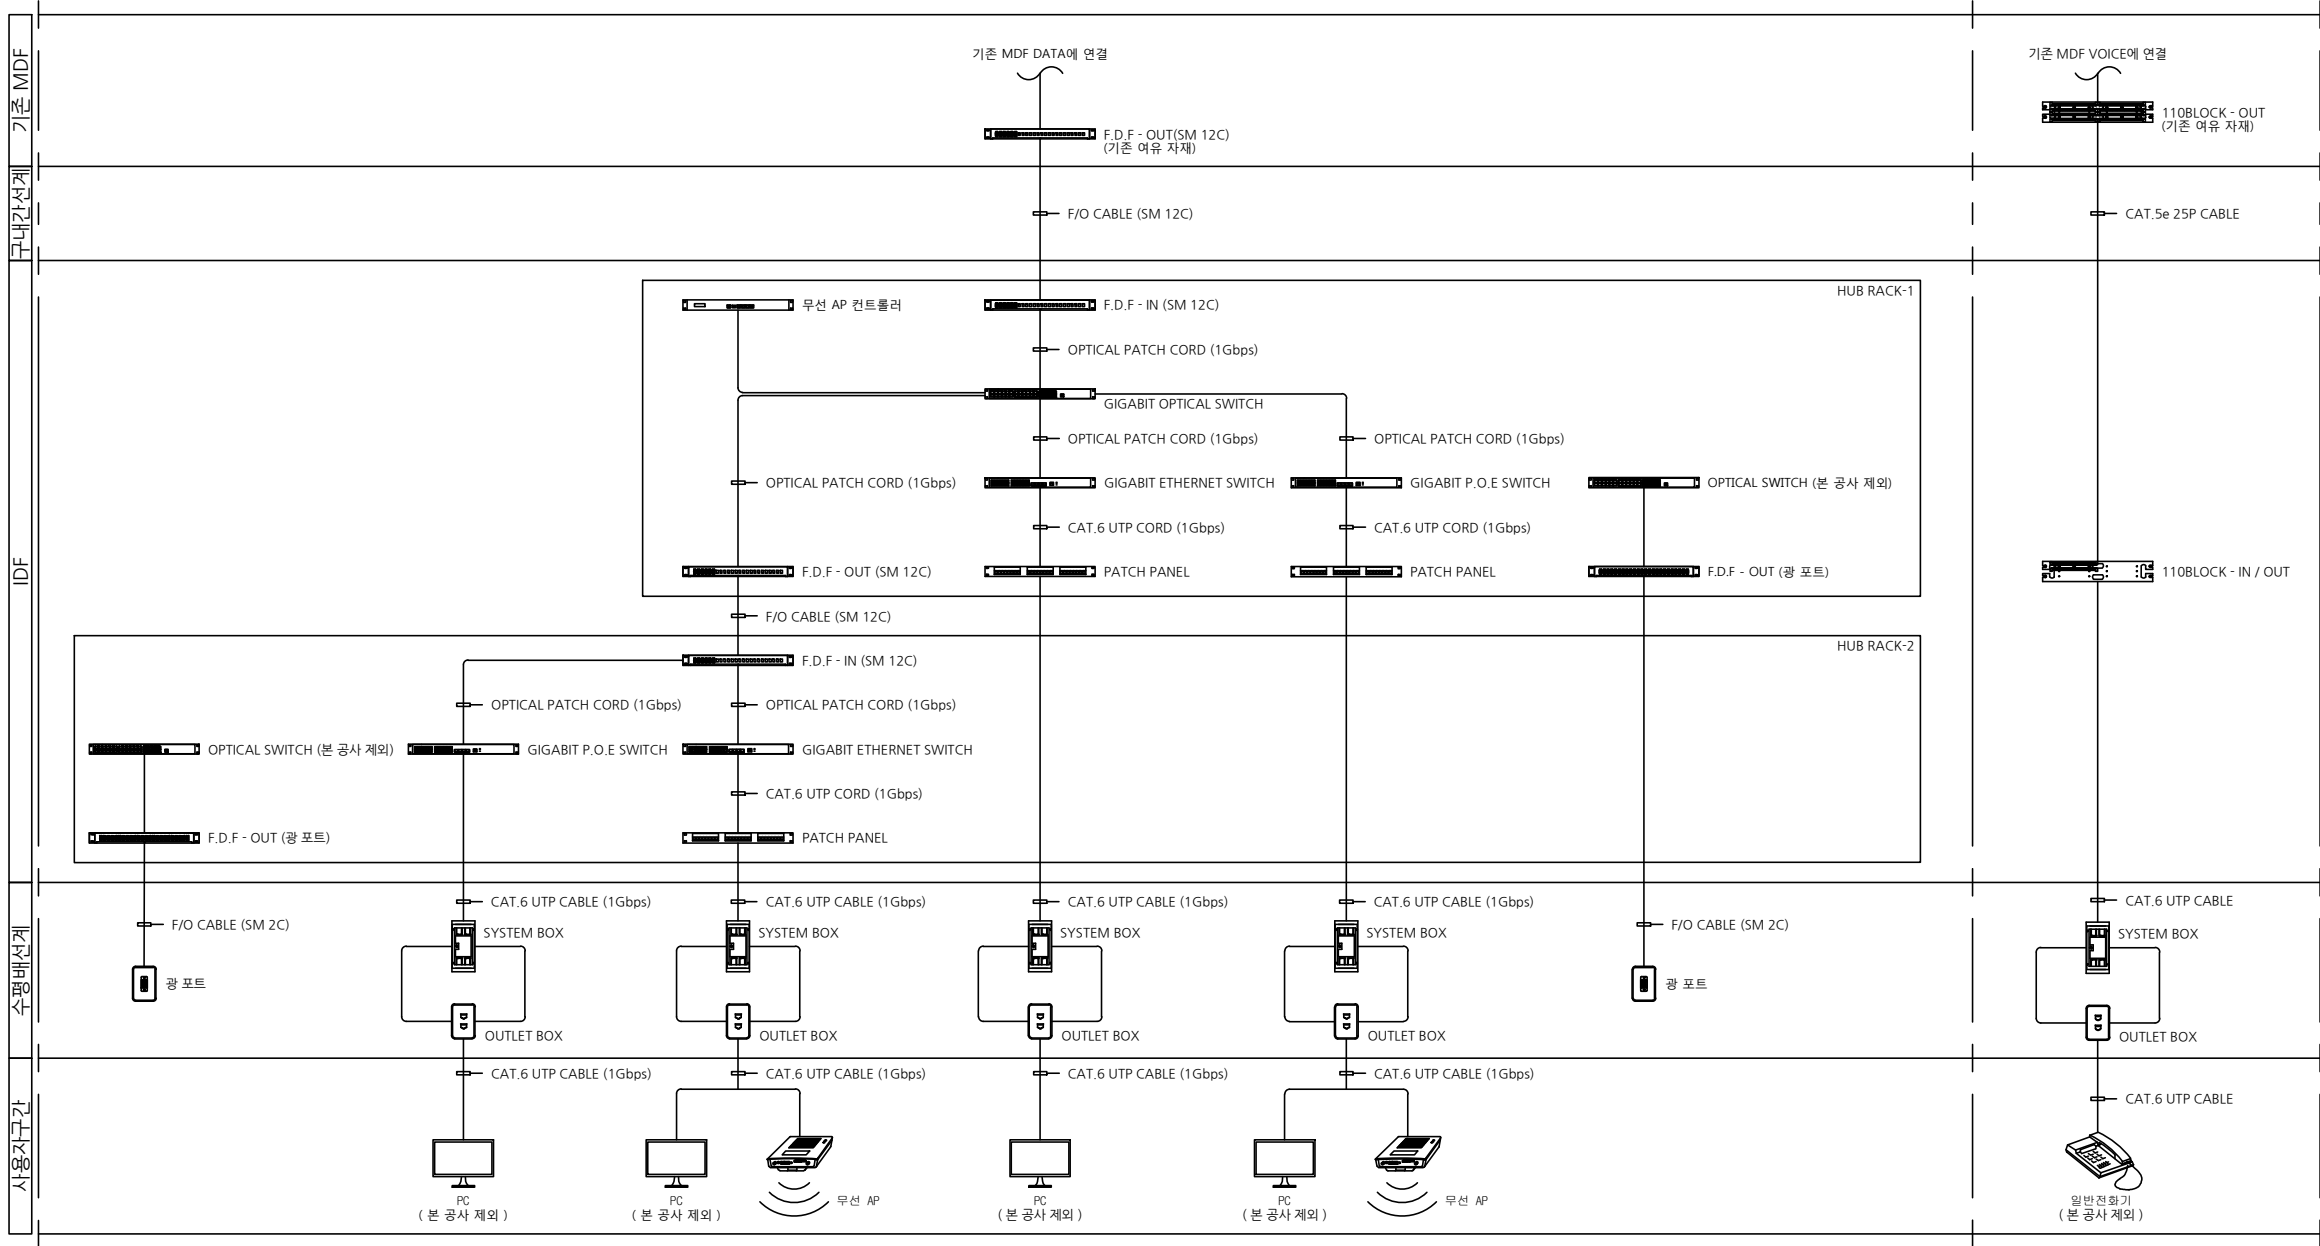

통합배선설비 구성도
축척:A1 : 1/NONE
A3 : 1/NONE