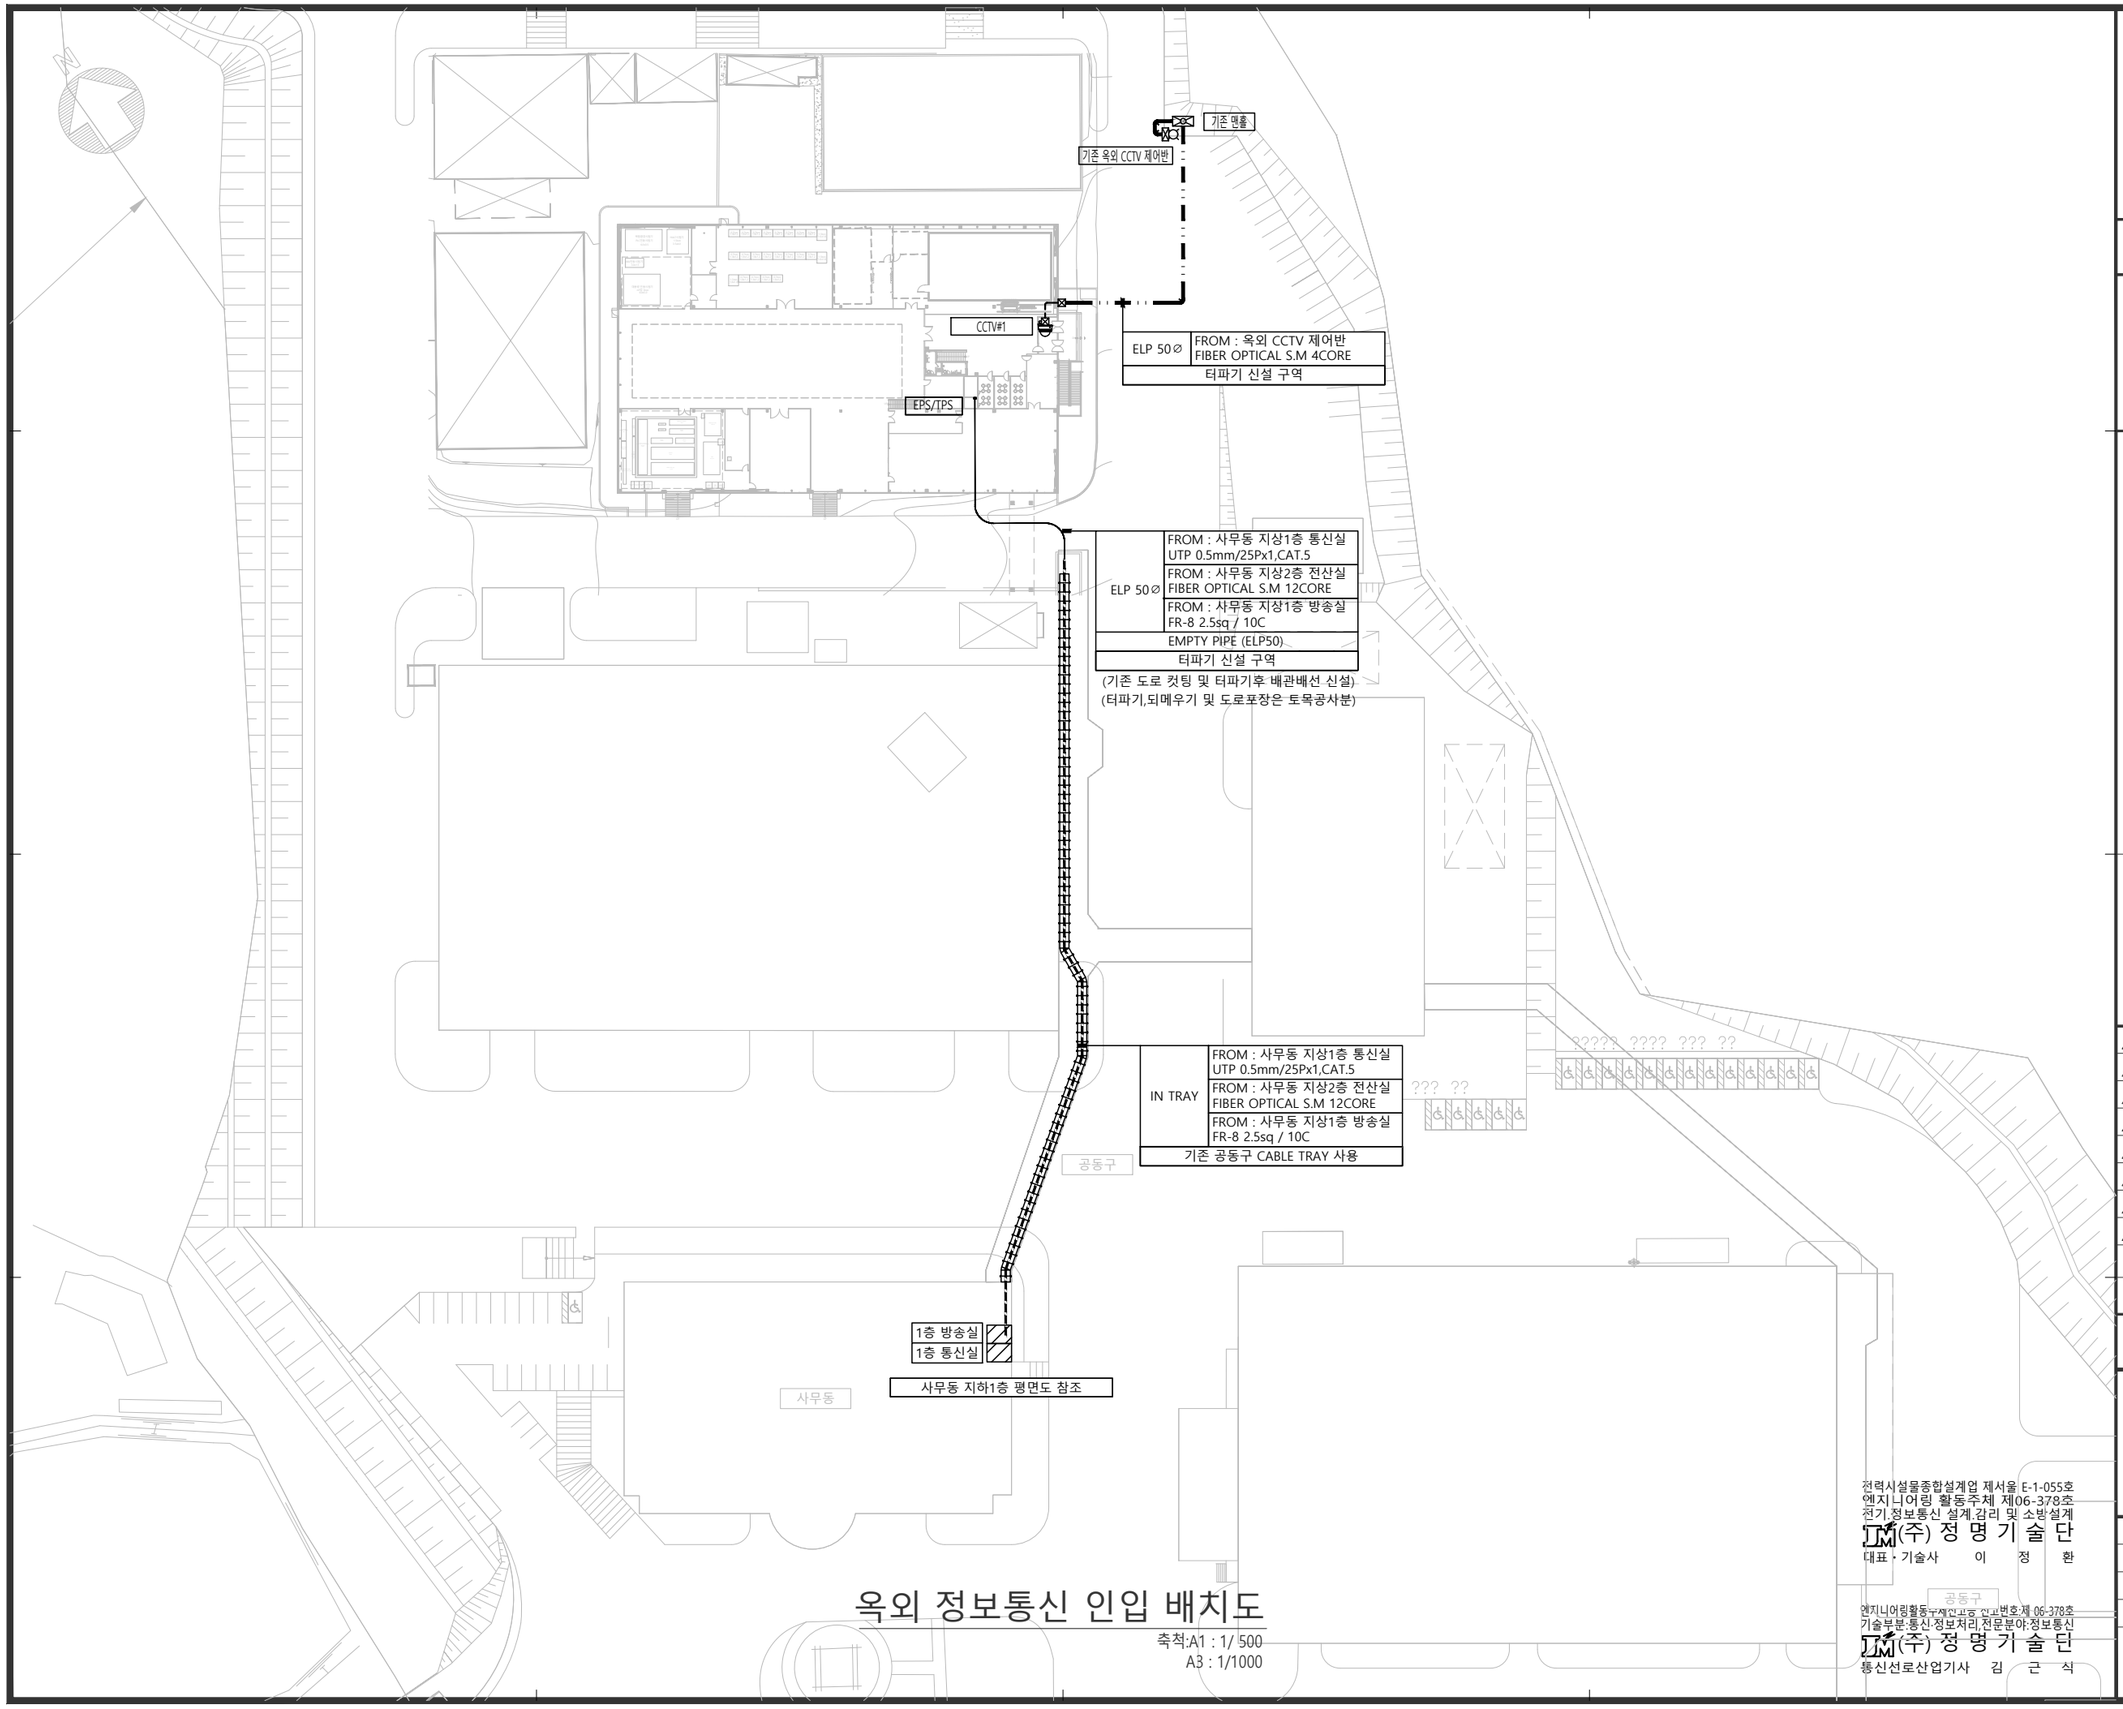


옥외 정보통신 인입 배치도

측척:A1 : 1/ 500
A3 : 1/1000

전력시설물종합설계업 제서울 E-1-055호
엔지니어링 활동주체 제06-378호
전기,정보통신 설계,감리 및 소방설계
(주) 정 명 기 술 단
대표 · 기술사 이 정 환

엔지니어링활동주체업고등 인고 번호제 06-378호
기술부분·통신·정보처리,전문분야·정보통신
(주) 정 명 기 술 단
통신선로산업기사 김 근 식

PROJECT TITLE
LS Electric
R-Center 구축

PROJECT NUMBER
624001

DESIGN CONSULTANT
가 운 건 축
GAUN I Architects & Engineers
서울시 강남구 언주로 141길 6, 5층 (논현동, 백향빌딩)
Tel:82-2-3443-7799 Fax:82-2-3443-3807
www.gaun.co.kr

NOTES

KEY PLAN

NO.	DESCRIPTION	DATE

ISSUES & REVISIONS

BUILDING NAME

DRAWING TITLE
옥외 정보통신 인입 배치도

DRAWN		SCALE	A3 : 1/500 A3 : 1/1000
CHECK 1	안 동 식		
CHECK 2	이 은 진	DATE	2024.04
APPR.	정 용 재		

DRAWING NO.
ET-00-003